



智脉共生：大钟寺AI产业集聚区生物黏菌路网更新概念方案 · 总平面图

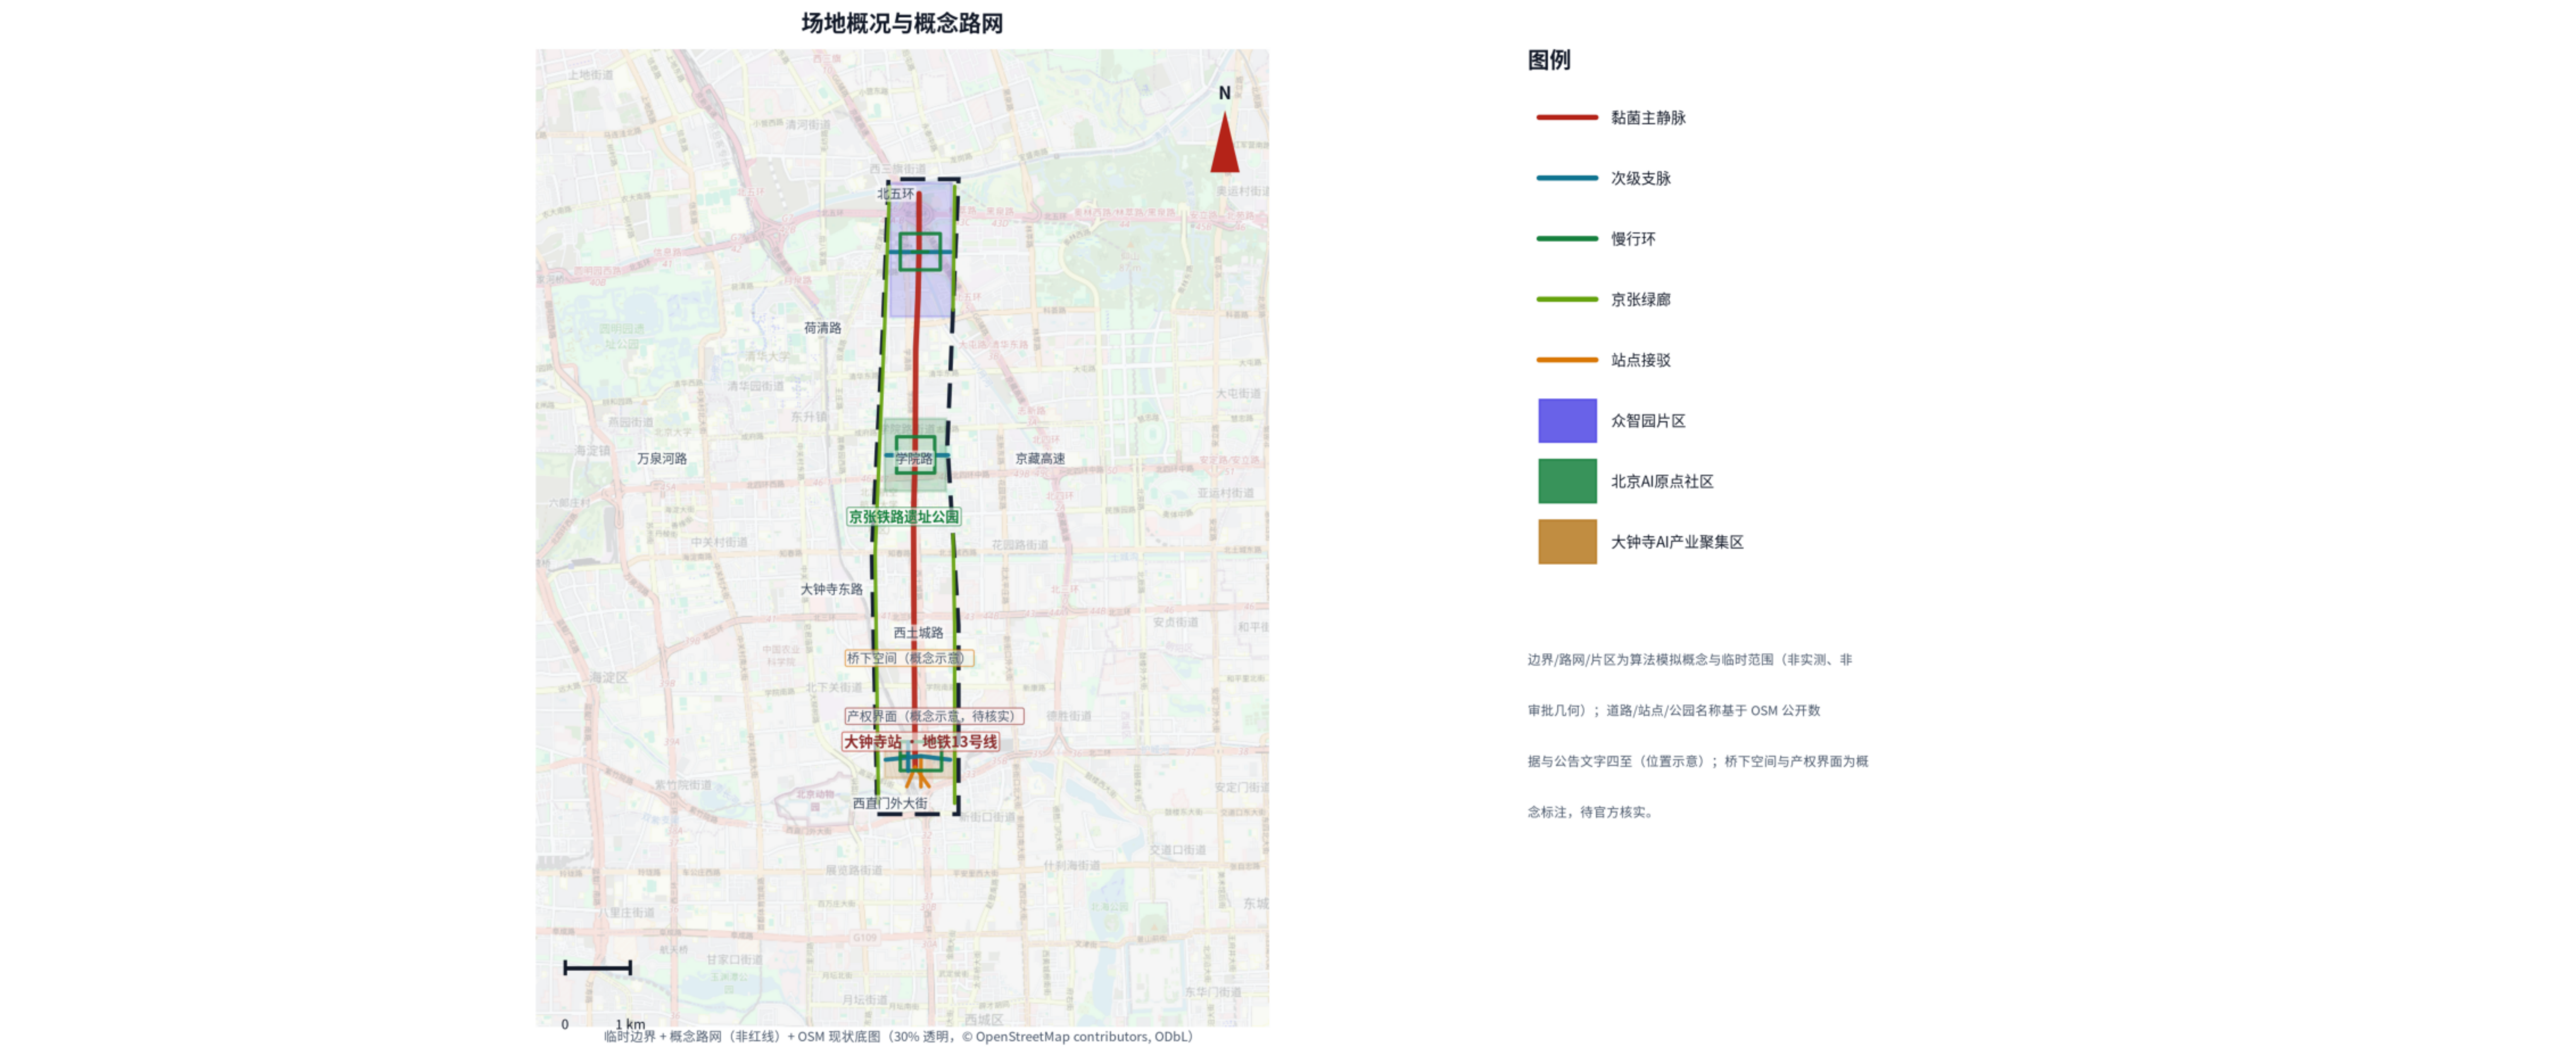

方法：生物黏菌自适应网络 + NSGA-II 多目标优化

真实 Physarum 167 边骨架 (方法验证)

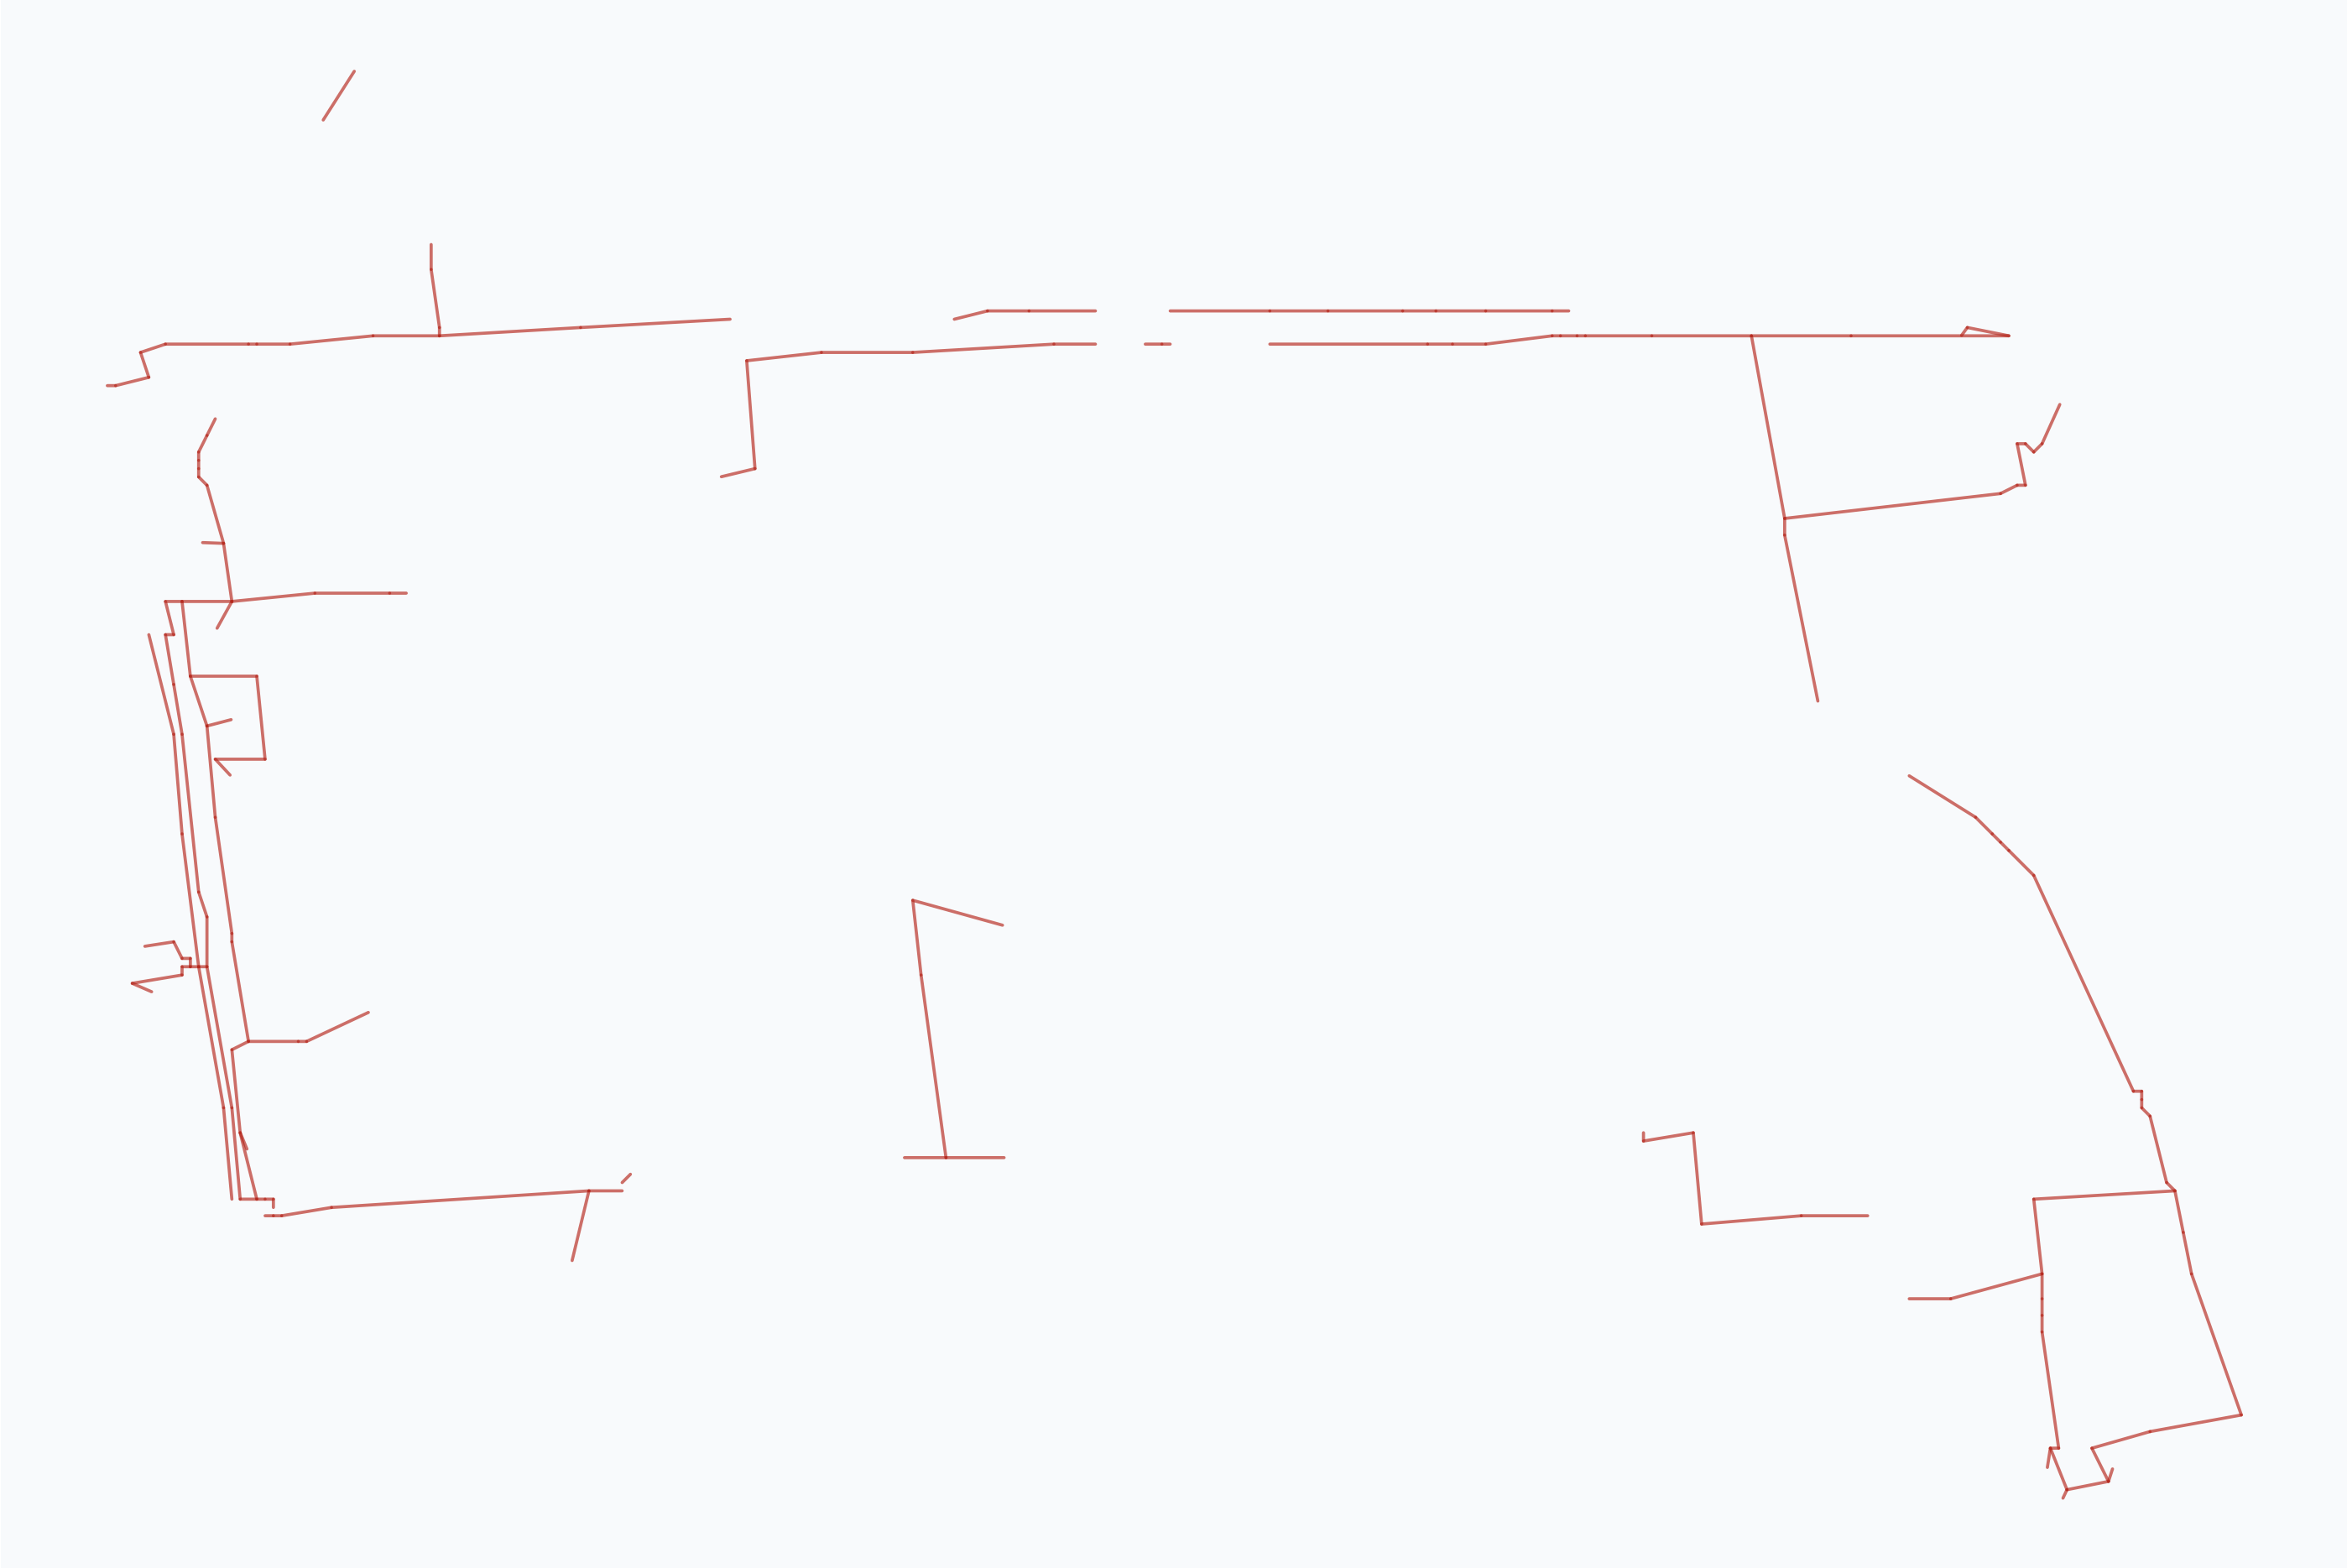

核心指标复算 (同屏同级 · 场外方法验证)

OFF-SITE 场外 · 非场地正式几何


0	19.20	167
遗产硬穿越	最优效率	网络边数
g1 硬约束 · 场外	Run7 冻结 2.802 · 基线 1.143 · 场外	真实黏菌骨架 · 场外

方法验证证据 (真实 Physarum 运行) : 167 边网络 / 效率 19.20 / 遗产目标 f3=f2 (退化为造价, 非场地内独立遗产合规结论)

三处重点区域与全球标杆案例

全球标杆案例（公开信息）

案例	地点	核心做法（公开报道）	借鉴/警示
Sidewalk Labs Quayside	多伦多	传感网络、数据信托试点（2017–2020）	数据治理 / 隐私警示
马斯达尔城	阿布扎比	低排放街区、被动降温、PRT 试点	低碳街区 + 接驳
松岛 IBD	仁川	填海新城、U-City 传感	新基建预留
阿姆斯特丹	荷兰	政企民协作、living lab	渐进更新 + 治理
雄安新区	河北	CIM 数字孪生、蓝绿网络、管廊	数字孪生 + 蓝绿

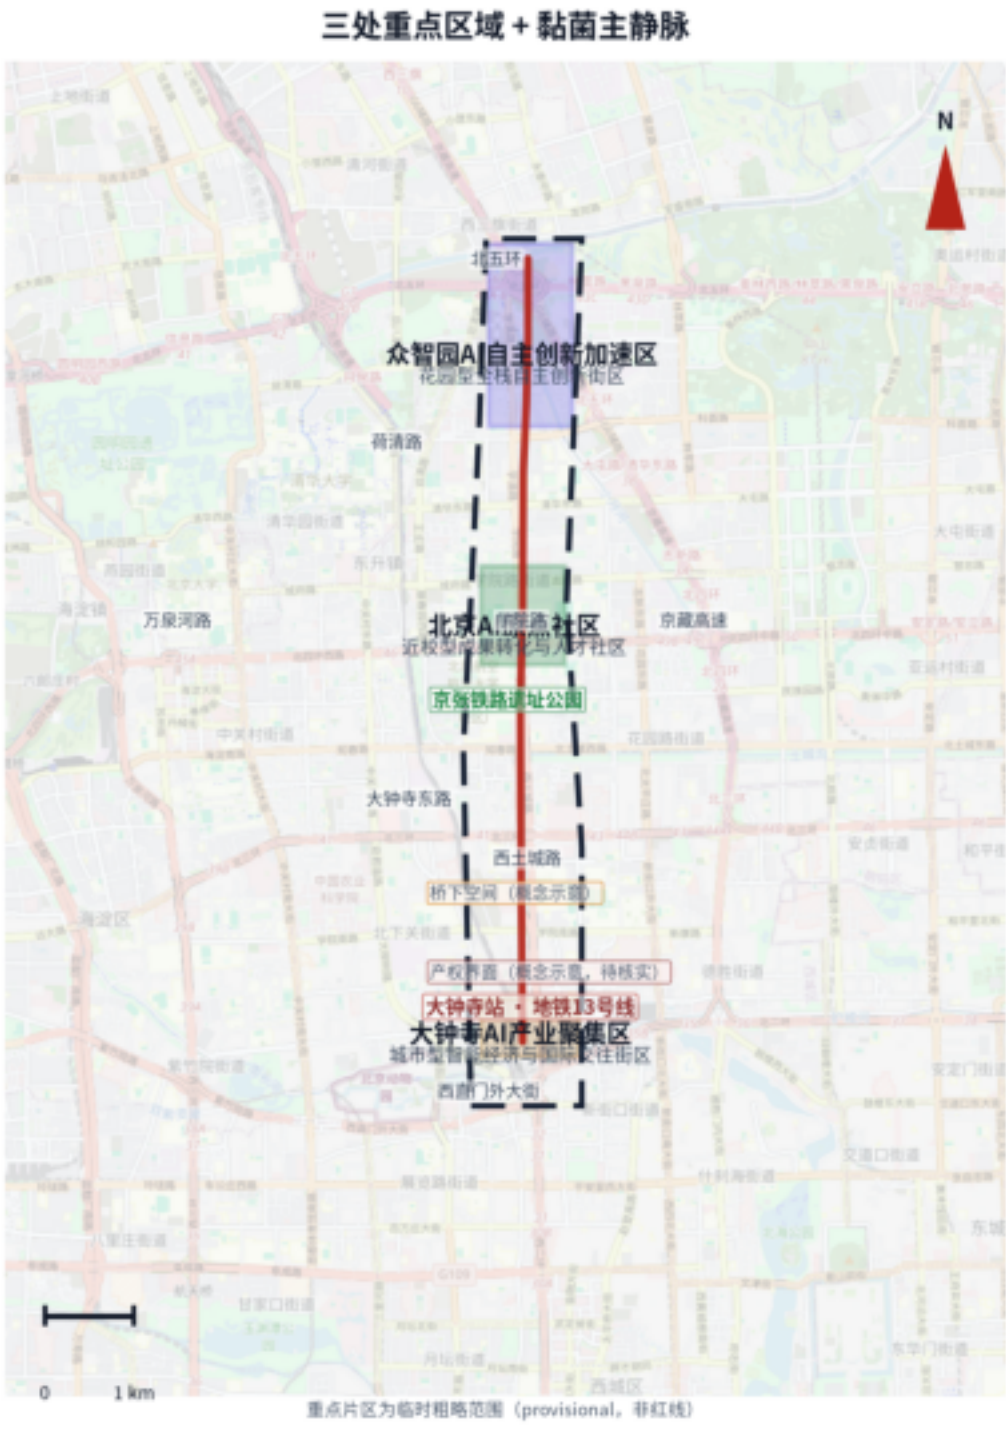

图例

- 众智园AI自主创新加速区
- 北京AI原点社区
- 大钟寺AI产业聚集区
- 黏菌主静脉
- 场地临时边界（虚线）

三处片区边界为公告面积+文字四至界定的临时范围，非官方 polygon，非红线；站点坐标为 OSM

公开数据。

无障碍与包容性（GB 50763-2012）


无障碍服务矩阵（GB 50763-2012）

画像	无障碍与包容性需求	空间响应
开源开发者	夜间协作可达与安全	无障碍出入口/卫生间、分级照明
初创团队	团队含残障成员	无障碍办公/共享测试空间
头部企业访客	国际/行动不便接驳	多语言标识、无障碍电梯
周边居民	老人/儿童/残障通行	缘石坡道、盲道、休息座椅
高校师生	残障师生连通	无障碍慢行缝合、体验点

风险、版权与合规说明


- 真实 Physarum 运行位于临时边界以西约 2-3 公里，仅 140 米交叠；未平移坐标、未编造红线。
- 遗产保护为 editable_by_agent=false 锁定图层；官方遗产几何缺失，f3≡f2（遗产影响退化为造价）。
- 本方案不声称官方批准、审定控规、最终权属或实施保证。
- HTML 不加载远程脚本/瓦片/字体/iframe/表单/API。
- 申诉救济：发现—登记—整改—回访闭环（建议性框架，待主管部门与运营单位批复）。

科学严谨性与可实施性深化（数据锚点）

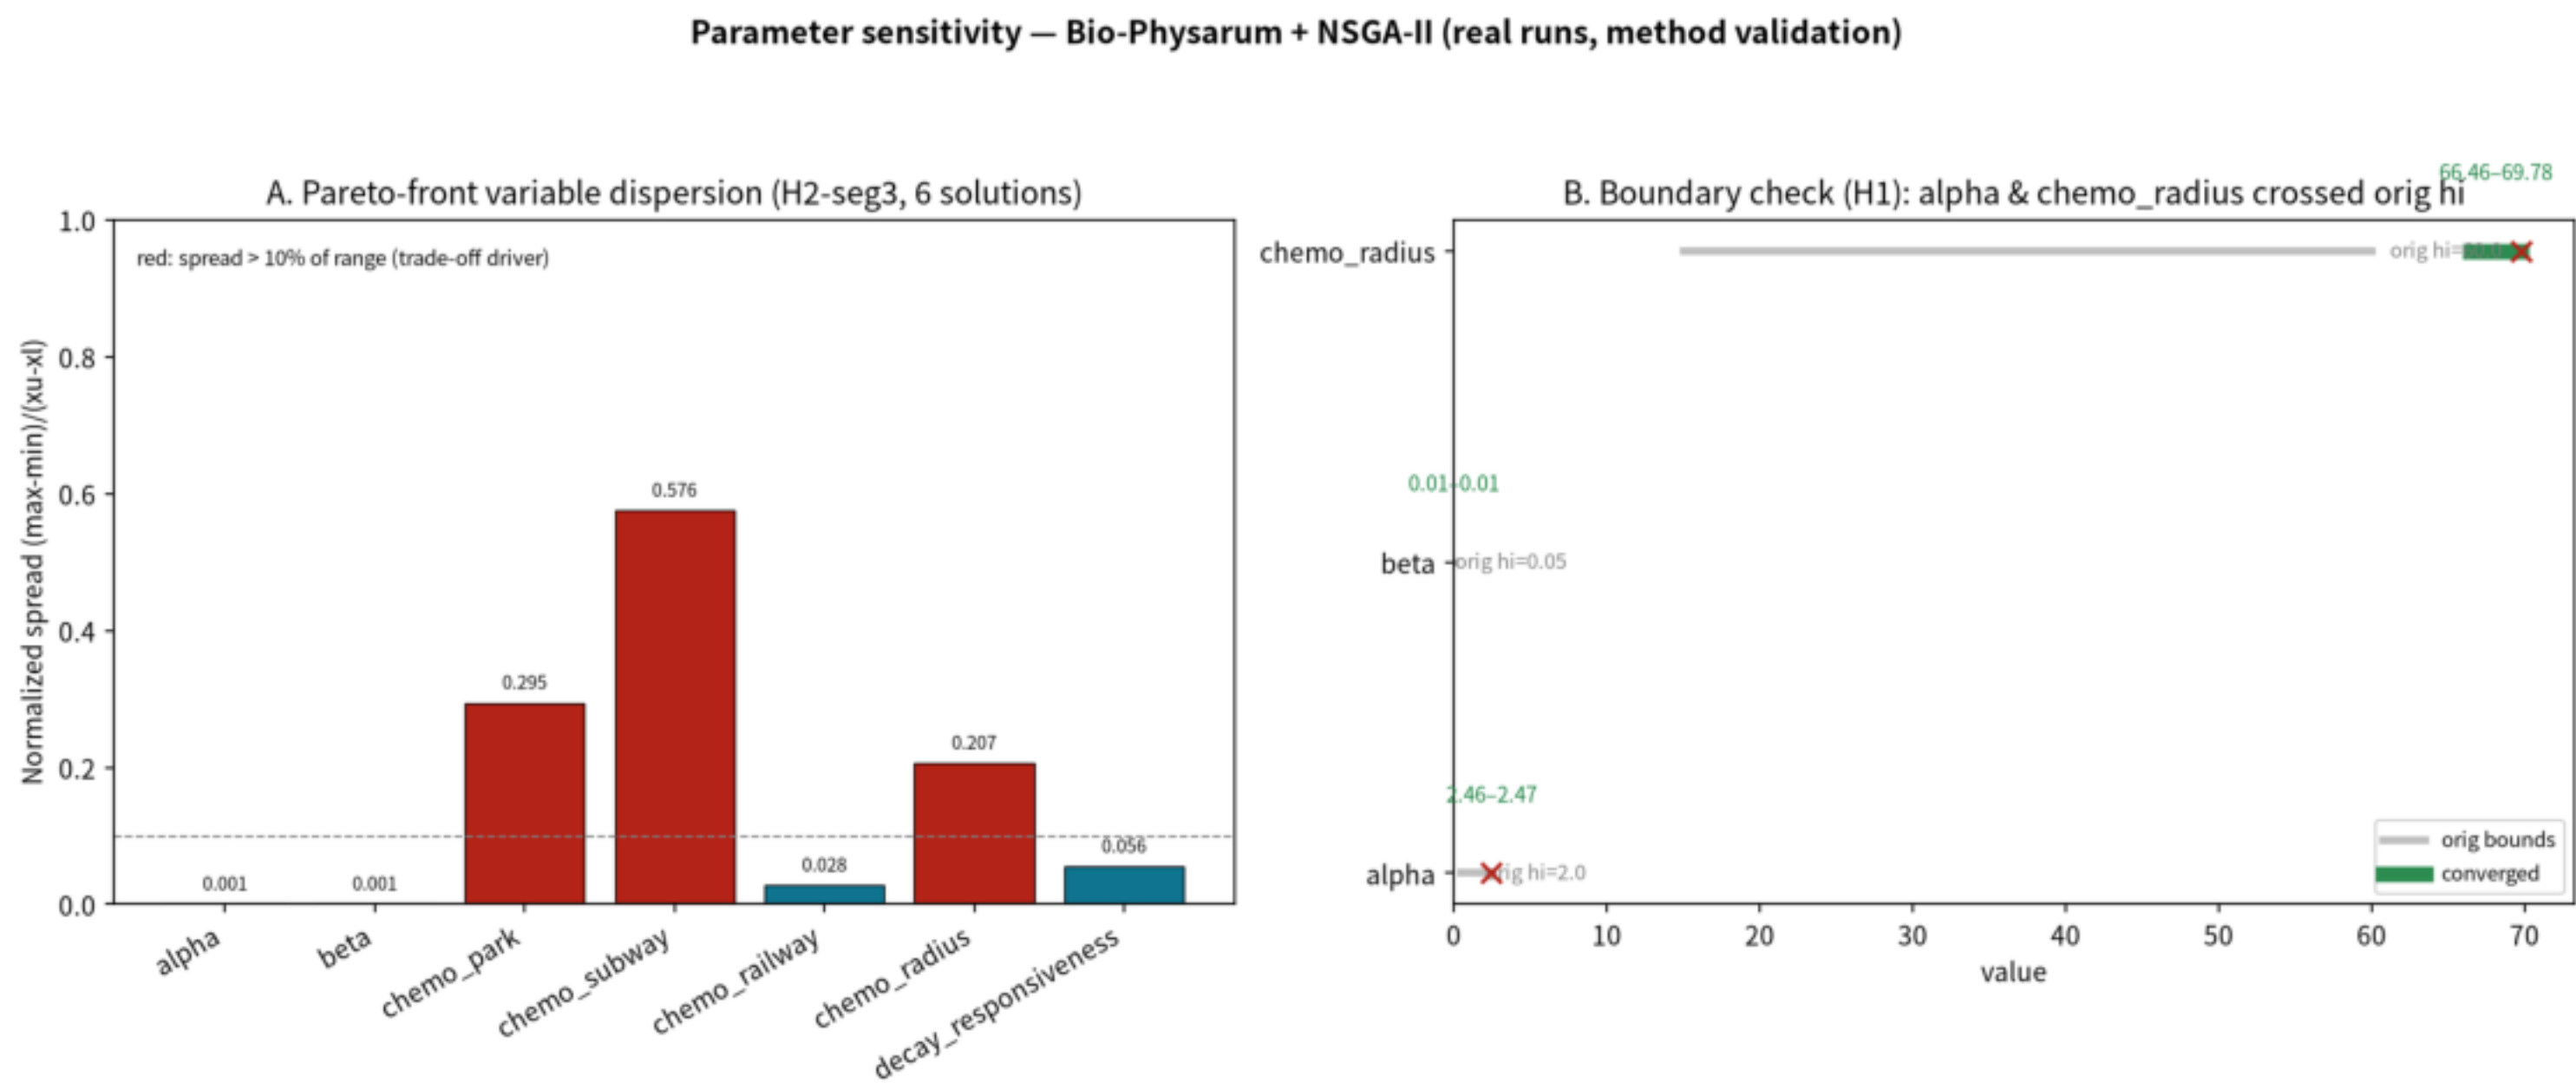

造价明细（建议性框架）			
等级	长度(m)	单价(元/m)	造价(万元)
主干路	740.2	8000	592.2
次干路	1744.1	5000	872.0
支路	3679.9	3000	1104.0
微循环	2648.8	1500	397.3
合计	8813.0	—	2965.5

平均 3365 元/m；仅路网市政造价，不含管线迁改/轨道土建/拆迁（建议性框架）

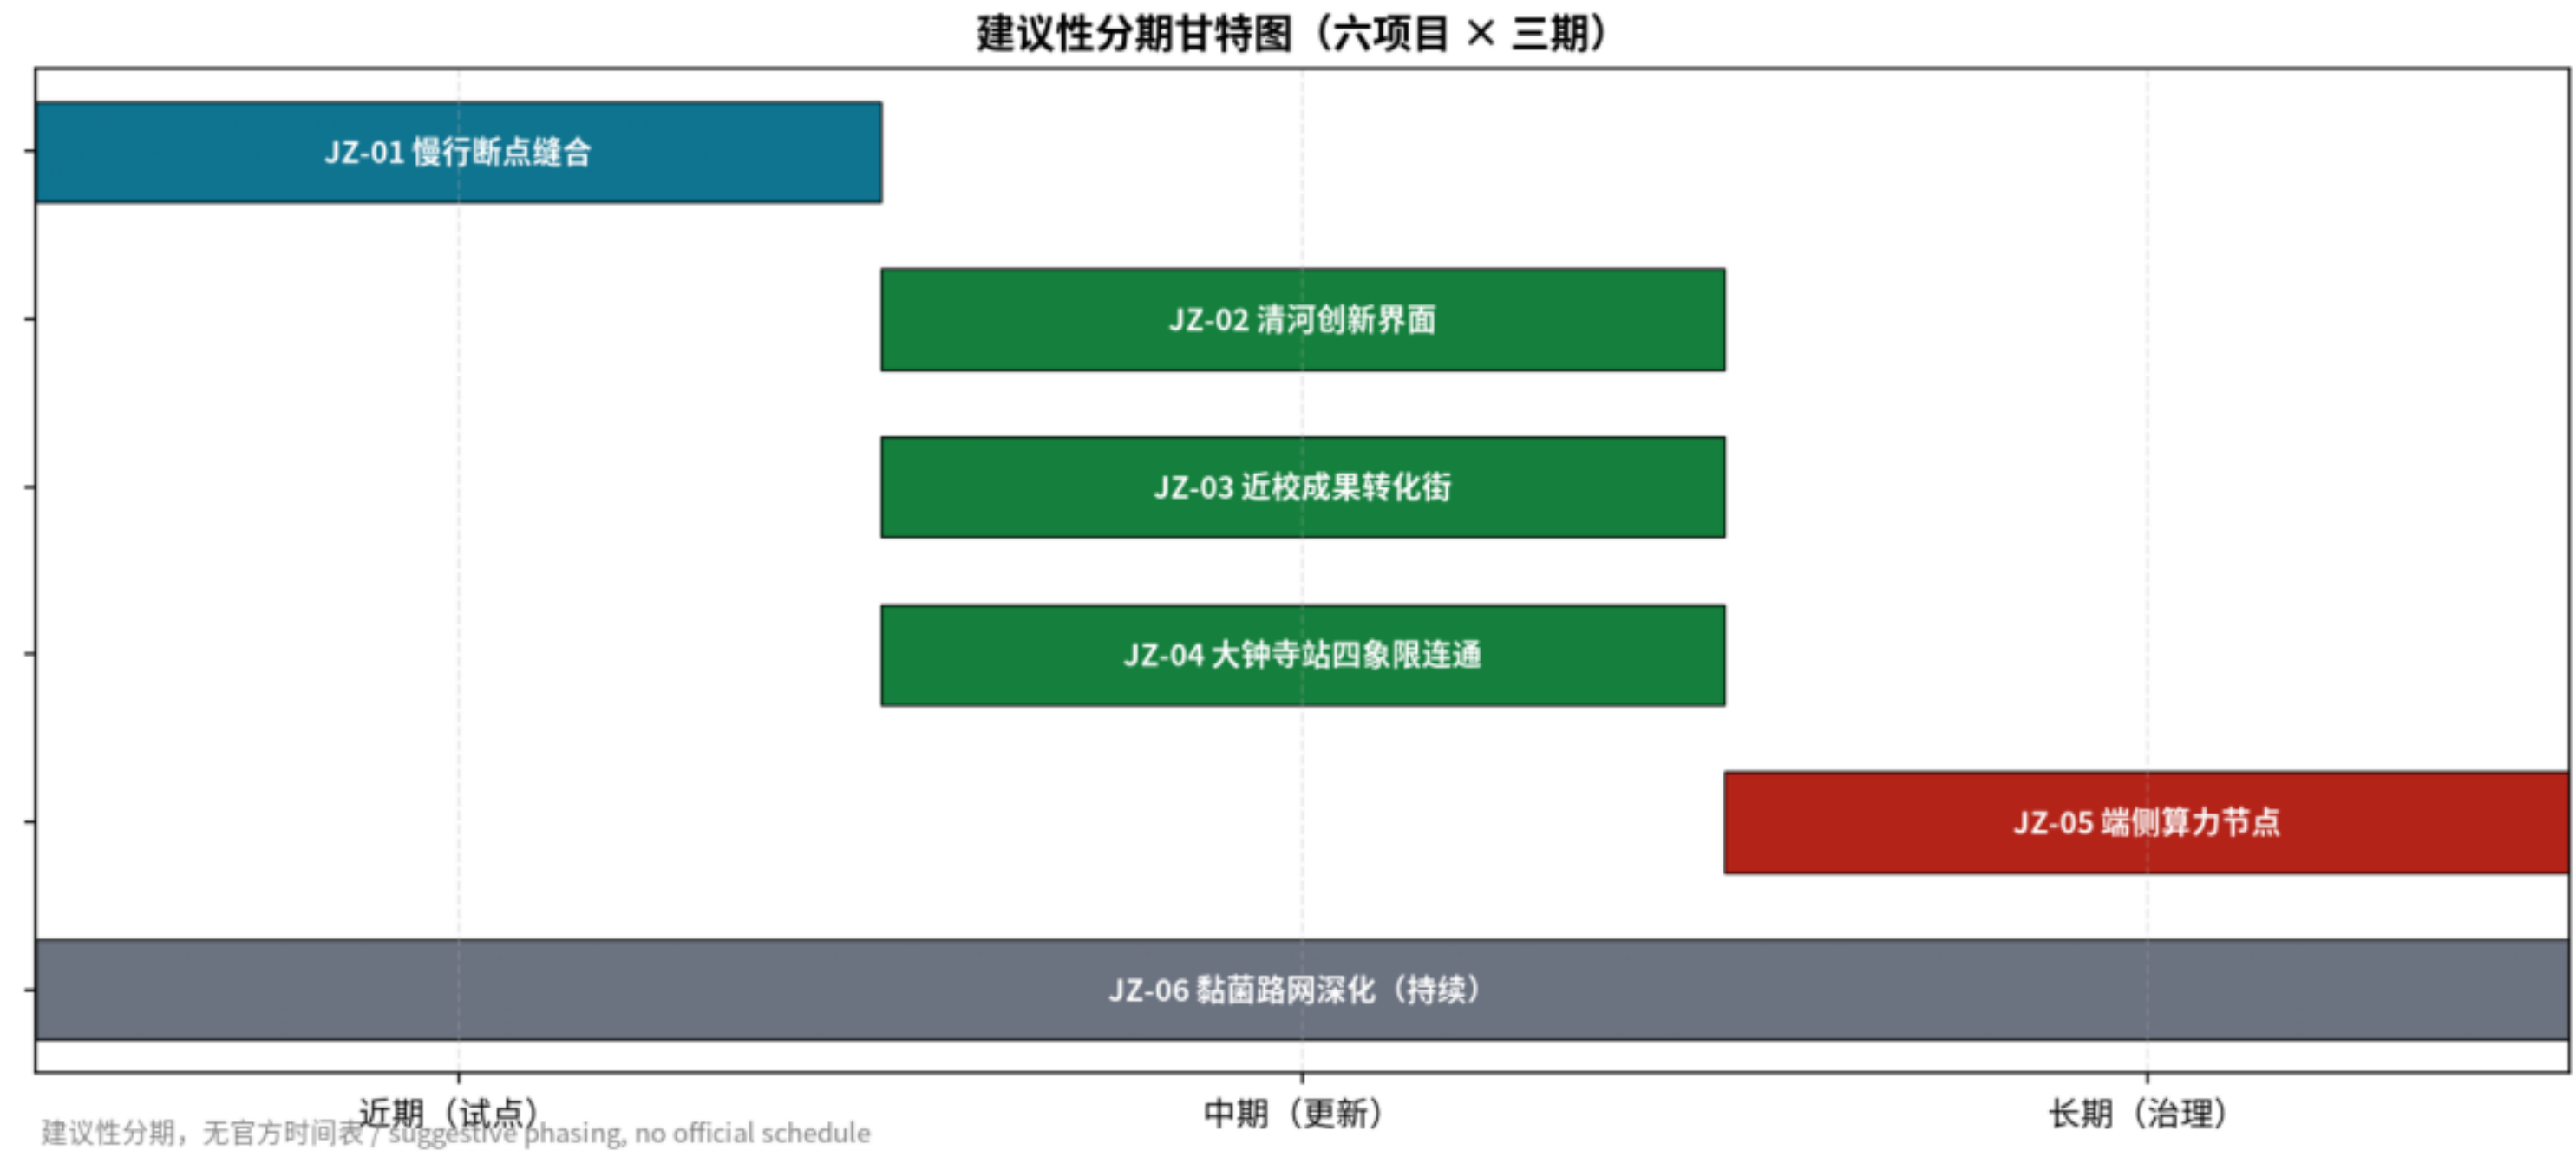

政策衔接矩阵（建议性框架）		
项目	政策/标准依据（真实）	待确认
JZ-01	GB 50763-2012 / 无障碍条例	桥下权属
JZ-02	海绵城市指南 / GB 50014	蓝线/防洪
JZ-03	北京城市更新条例（建议性）	条款/权属
JZ-04	GB/T 51328 / GB 50763	站点/管线
JZ-05	新基建政策（待确认）	监管主体
JZ-06	京政发〔1984〕128号	图则/红线