




# CONTINUUM

## Coordinated Urban Design for the Centennial Jing-Zhang AI Innovation Belt • Concept Proposal

### CONTENTS

|                                                           |    |
|-----------------------------------------------------------|----|
| 01 Overall structure: one spine, three areas, two wings   | 02 |
| 02 Land-use structure: seamless zoning partition          | 03 |
| 03 Detailed design index of the three key areas           | 04 |
| 04 Slow mobility × blue-green public space system         | 05 |
| 05 Metrics recalculation & evidence chain                 | 06 |
| 06 Brand identity system: mark, lockups & hierarchy       | 07 |
| 07 Cross-regional coordination: one belt, five directions | 08 |
| 08 Scenario System & Implementation Outline               | 09 |

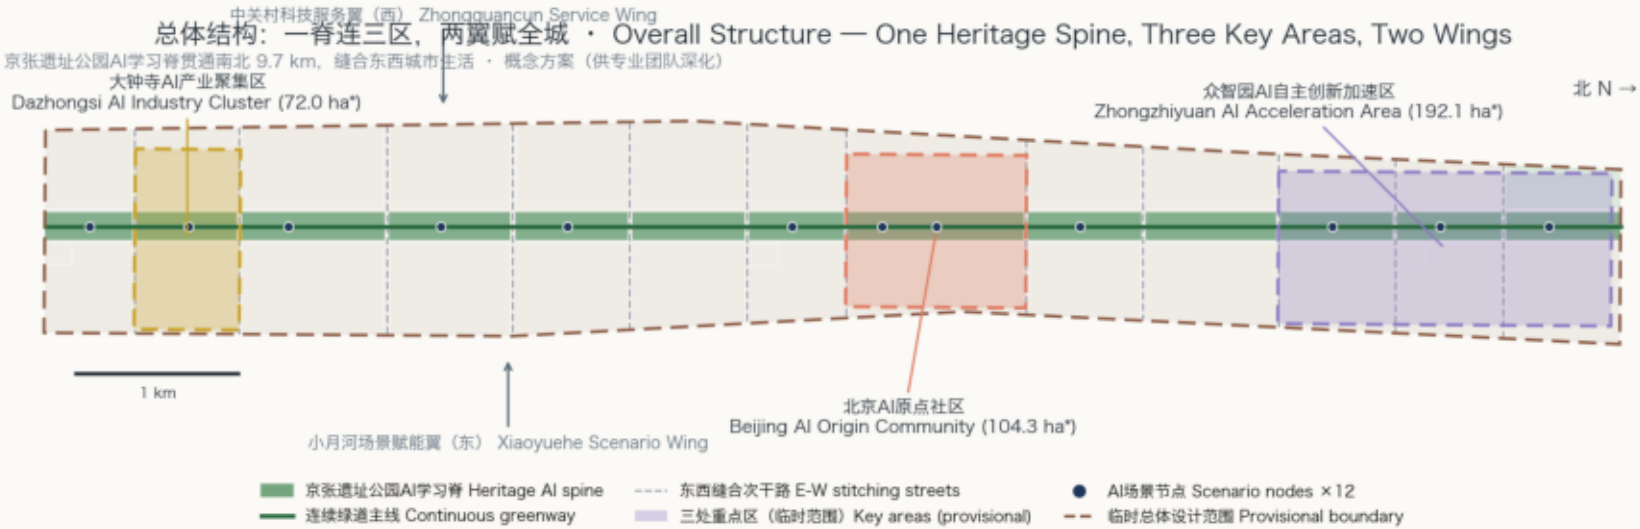


边界为临时约束范围（provisional，虚线），非官方红线；面积均为临时边界复算设计值。来源 Sources: 官方公告 2026-05-09 • 仓库资料包 • 本包 geometry/\*/\*.geojson

01 Overall structure: one spine, three areas, two wings


All boundaries are provisional constraints, not official redlines; all areas are design values recomputed on provisional geometry. Concept proposal for professional deepening — not statutory planning, not a government-approved conclusion.

01 Overall structure: one spine, three areas, two wings

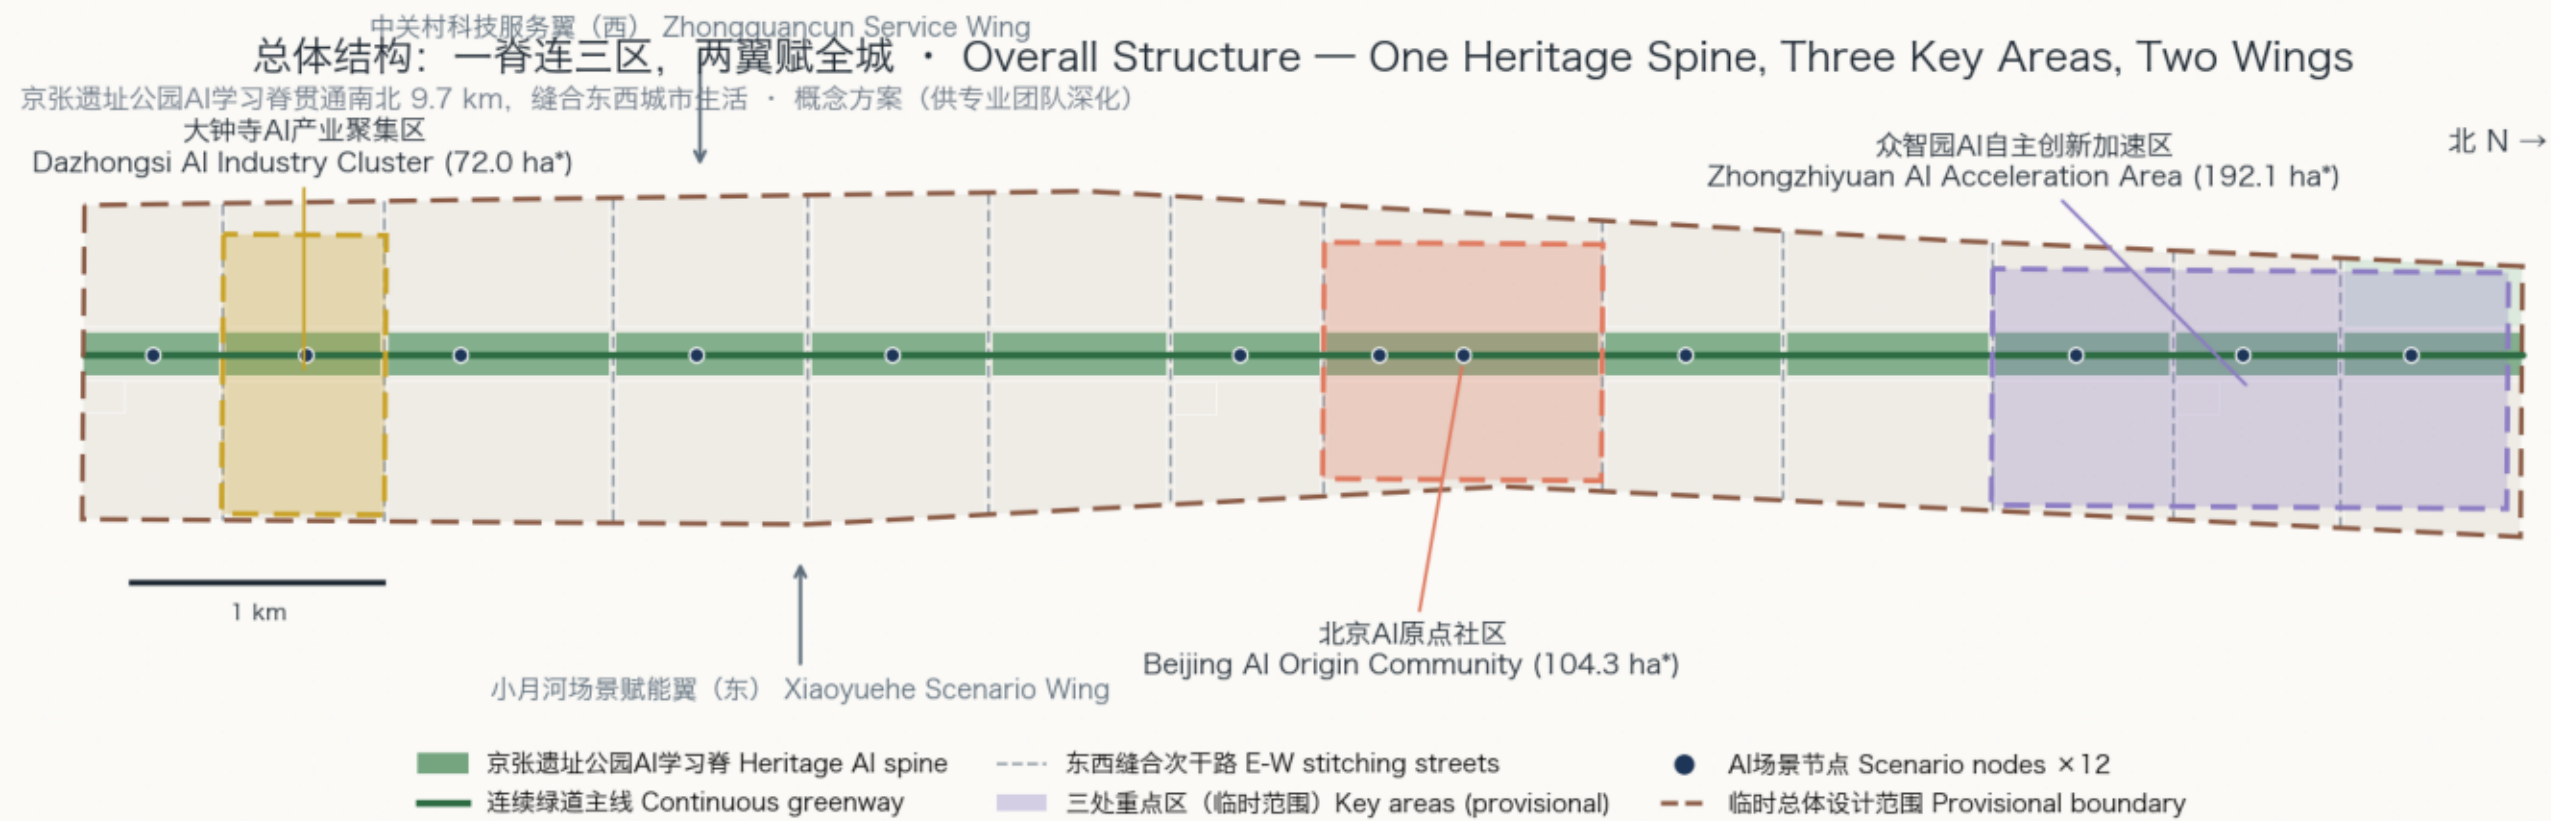

边界为临时约束范围（provisional，虚线），非官方红线；面积均为临时边界复算设计值。Provisional boundary (dashed), not an official redline; areas recomputed on provisional geometry. 来源 Sources: 官方公告 2026-05-09 · 仓库资料包 · 本包 geometry/\*.geojson

02 Land-use structure: seamless zoning partition

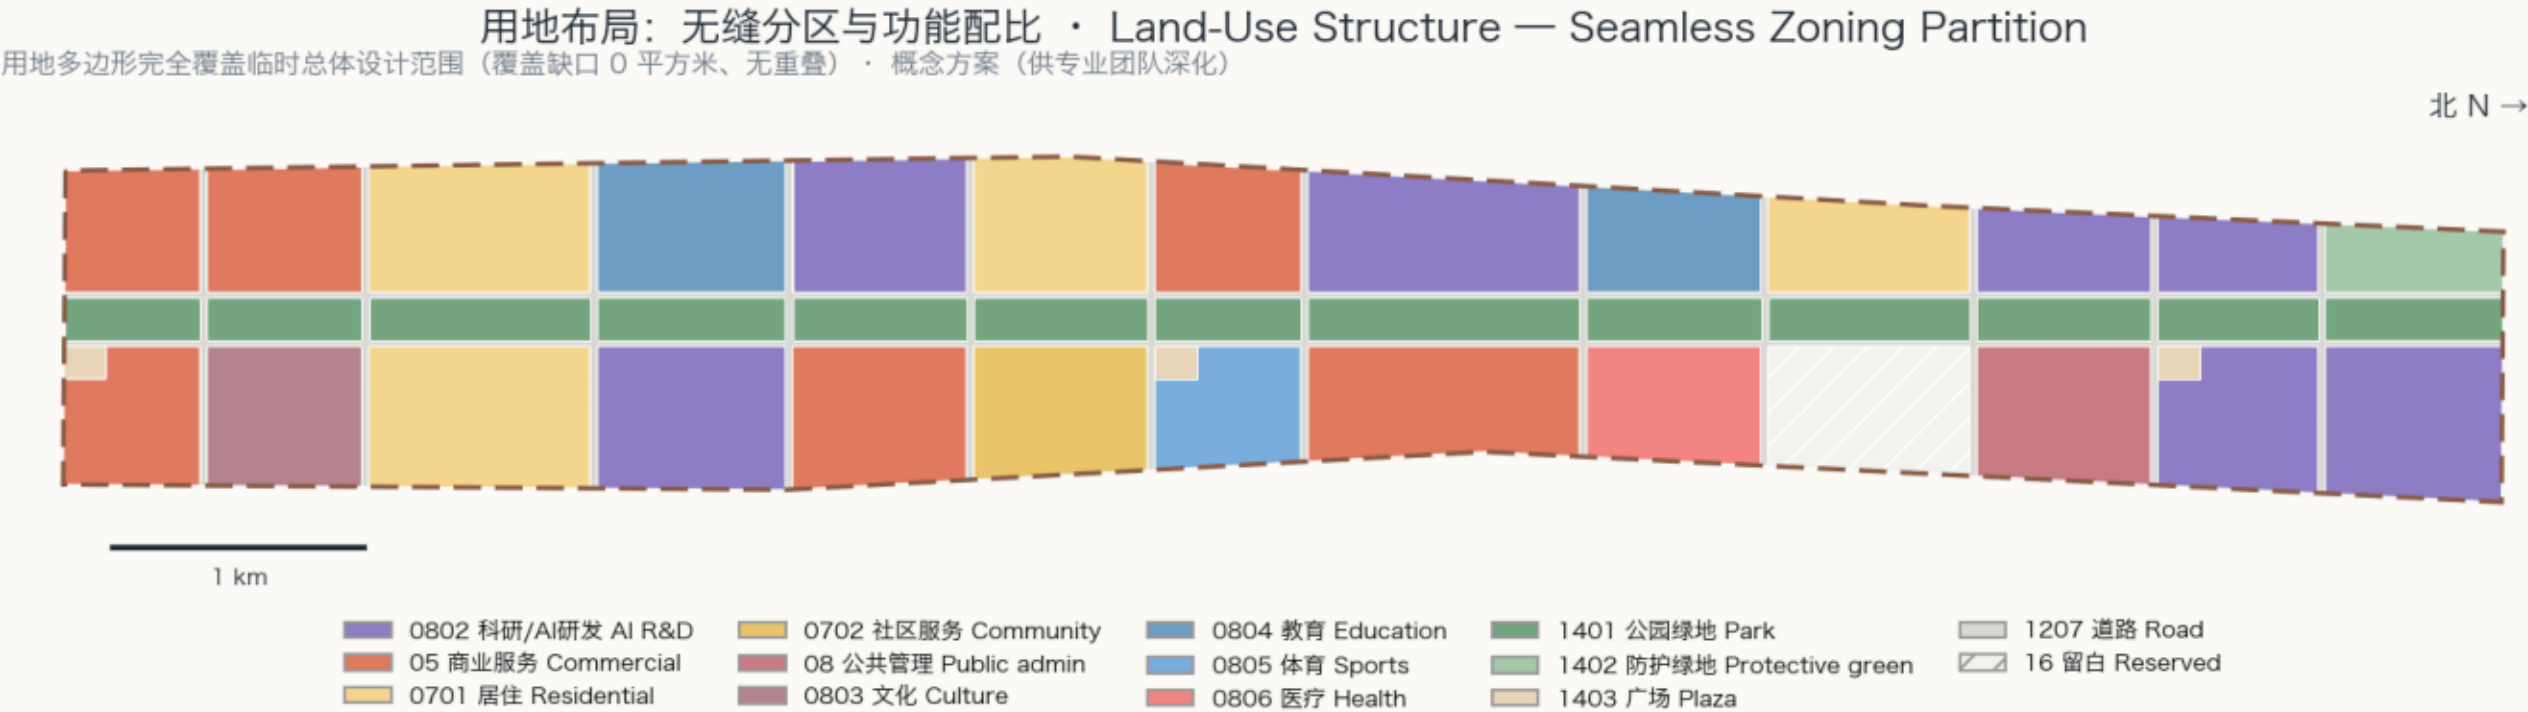


用地构成（公顷） · Land-use composition (ha) — 合计 total 1141 ha = 11.41 km²（临时边界复算 recomputed on provisional boundary）




边界为临时约束范围（provisional，虚线），非官方红线；面积均为临时边界复算设计值。Provisional boundary (dashed), not an official redline; areas recomputed on provisional geometry. 来源 Sources: 官方公告 2026-05-09 · 仓库资料包 · 本包 geometry/\*.geojson

三处重点区详细设计索引 · Detailed Design Index of the Three Key Areas

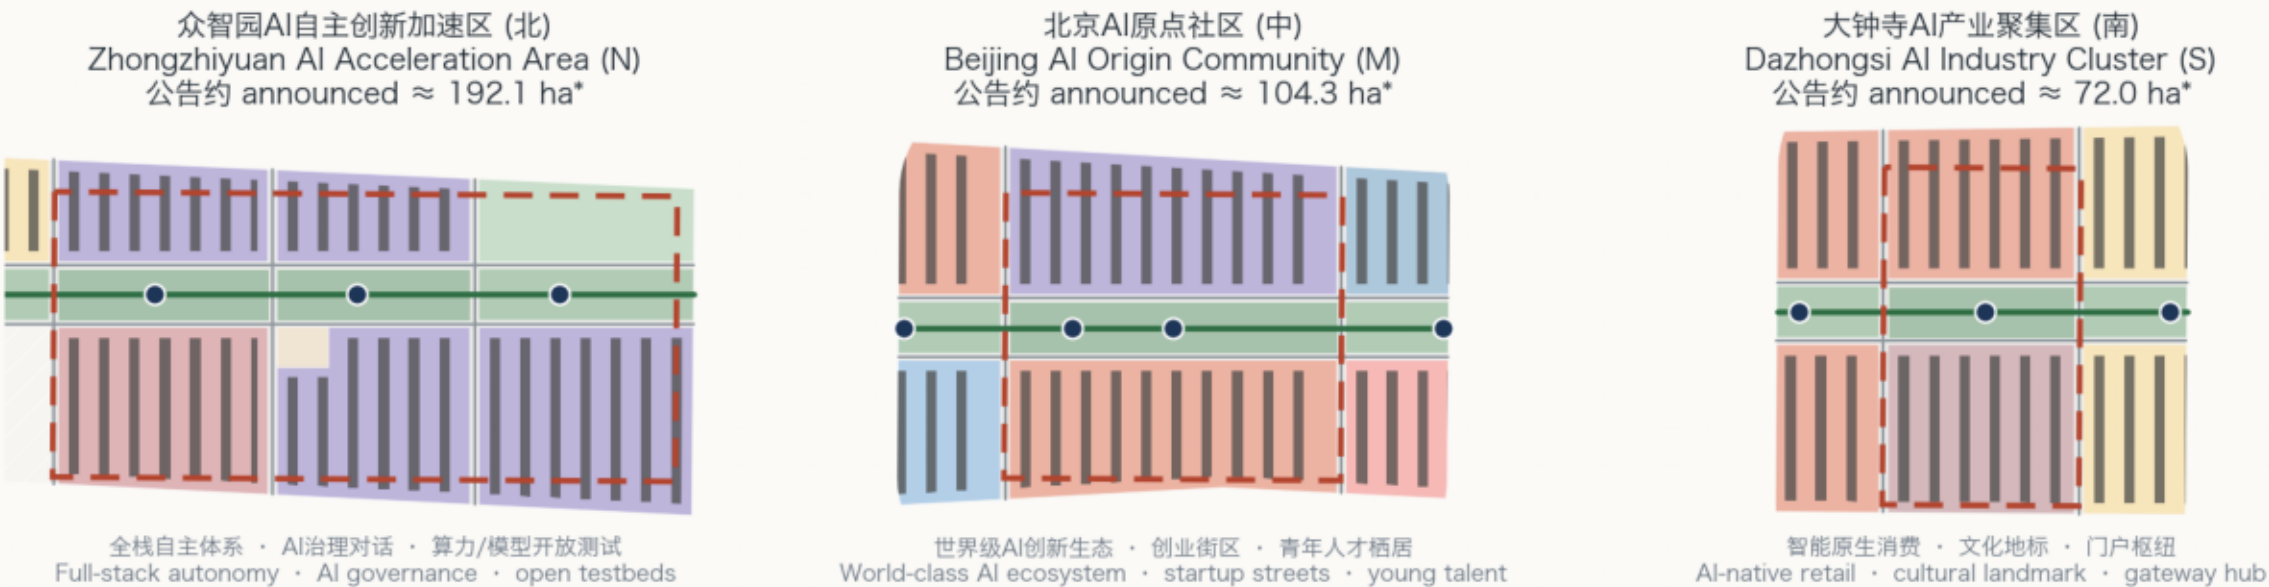

■ 科研/AI研发 AI R&D ■ 商业服务 Commercial ■ 公园绿地 Park ■ 概念建筑体量 Concept massing ■ 绿道主线 Greenway ● AI场景节点 Scenario node - - 重点区临时范围 Provisional key-area

边界为临时约束范围 (provisional, 虚线), 非官方红线; 面积均为临时边界复算设计值。Provisional boundary (dashed), not an official redline; areas recomputed on provisional geometry. 来源 Sources: 官方公告 2026-05-09 · 仓库资料包 · 本包 geometry/"\*.geojson \*面积为公告约数 announced approximate values

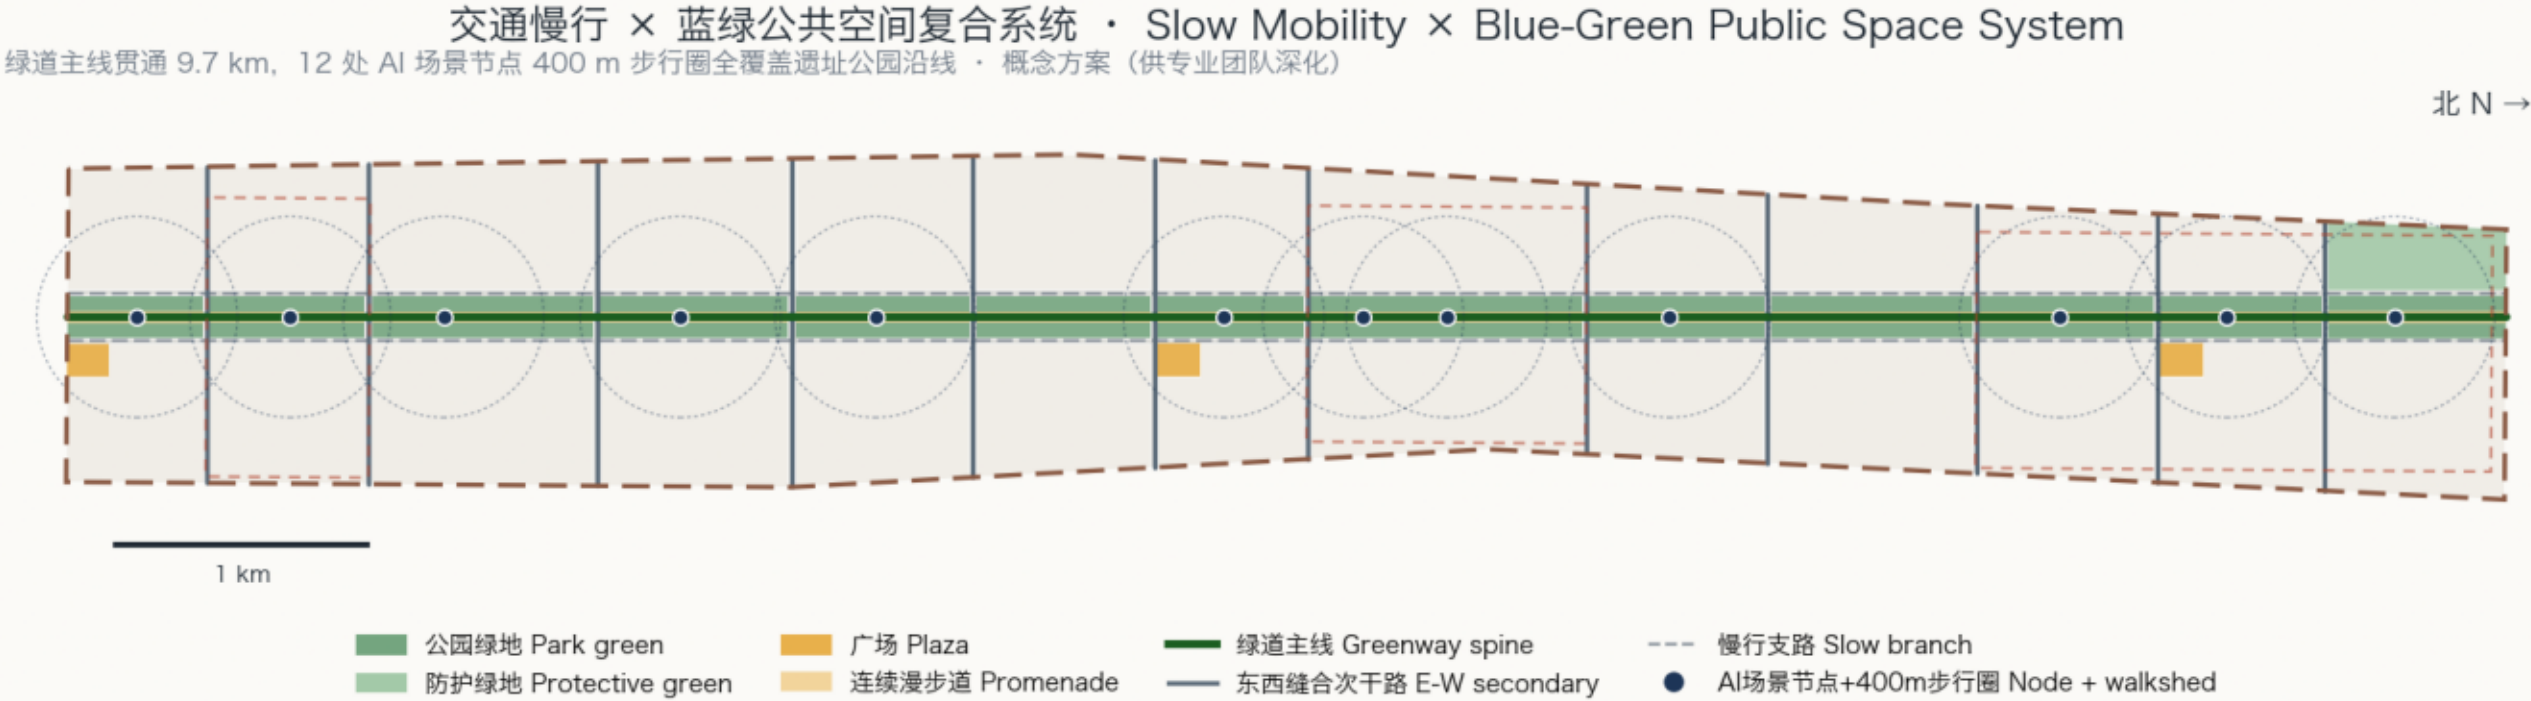

边界为临时约束范围 (provisional, 虚线), 非官方红线; 面积均为临时边界复算设计值。Provisional boundary (dashed), not an official redline; areas recomputed on provisional geometry. 来源 Sources: 官方公告 2026-05-09 · 仓库资料包 · 本包 geometry/\*.geojson


核心指标复算与证据链 · Metrics Recalculation & Evidence Chain

全部数值由 geometry/\*.geojson 在 EPSG:4548 投影下复算，与 metrics.json 完全一致；空间自检 PASS（用地覆盖缺口 0 m<sup>2</sup>、无重叠）。Recomputed from GeoJSON in EPSG:4548; identical to metrics.json; spatial self-check PASS.


① 面积总量 Headline areas

|                         |                        |
|-------------------------|------------------------|
| 总体设计范围（临时复算） Site area* | 11.413 km <sup>2</sup> |
| 绿地面积 Green space        | 177.8 ha               |
| 公共空间面积 Public space     | 51.6 ha                |
| 建筑基底（概念） Footprint*     | 226.9 ha               |
| 概念总建筑规模 Concept GFA*    | 18.39 M m <sup>2</sup> |


② 结构比例 Structural ratios (%)

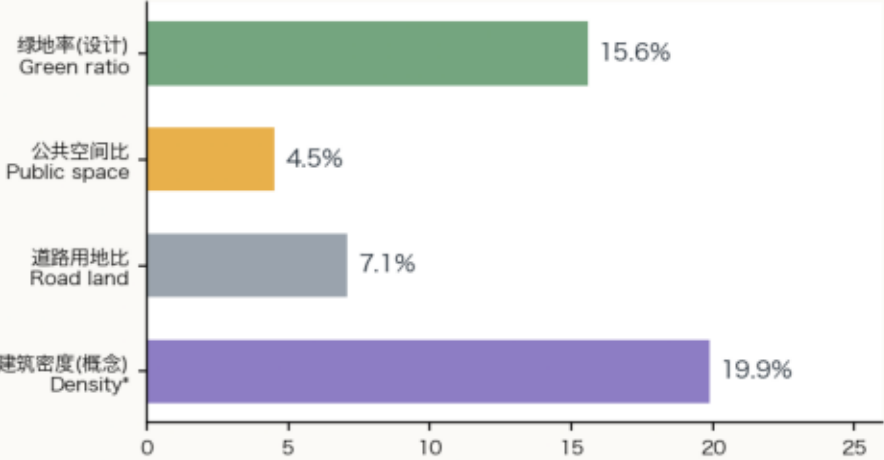

③ 重点区面积校核 Key-area check (ha)

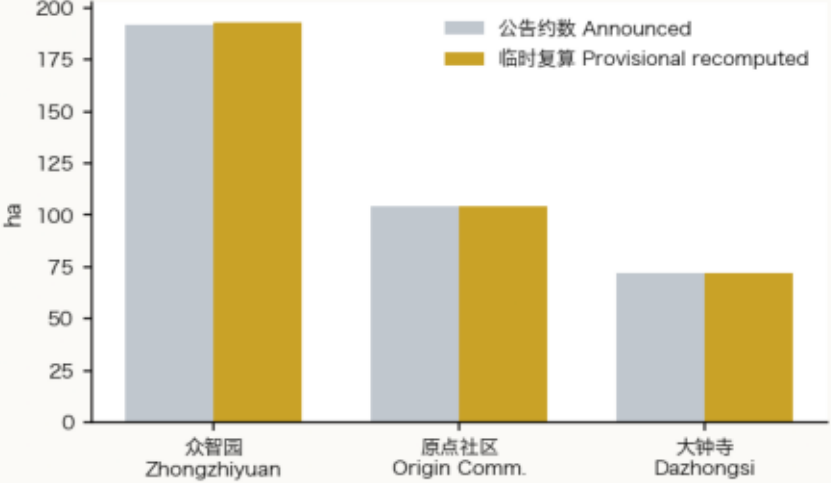


④ 概念分期 Concept phasing (km<sup>2</sup>)

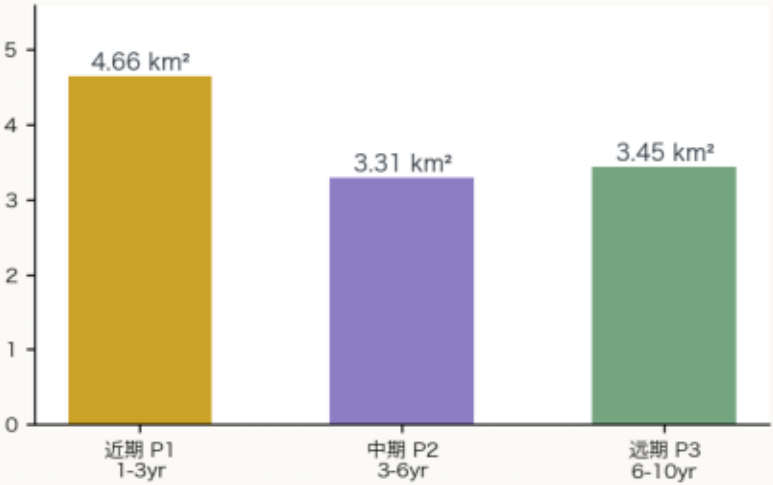

⑤ 待正式数据补齐 Pending official data

|                             |                         |
|-----------------------------|-------------------------|
| 法定容积率 Statutory FAR         | 待控规条件 pending           |
| 法定建筑高度 Height control       | 待管控条件 pending           |
| 法定绿地率 Statutory green ratio | 待控规条件 pending           |
| 官方精确边界 Official boundary    | 临时替代 provisional in use |
| 管控/红线矢量 Constraint vectors  | 层有意留空 layer empty       |

⑥ 证据链 Evidence chain

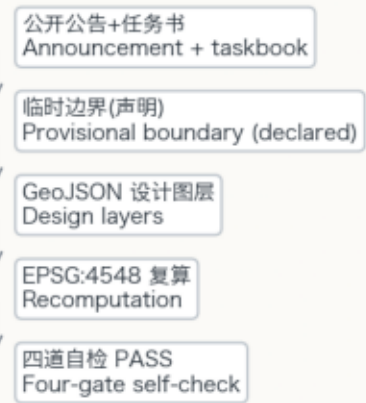

边界为临时约束范围（provisional，虚线），非官方红线；面积均为临时边界复算设计值。Provisional boundary (dashed), not an official redline; areas recomputed on provisional geometry. 来源 Sources: 官方公告 2026-05-09 · 仓库资料包 · 本包 geometry/\*.geojson \*概念设计量，非法定指标 concept design quantities, not statutory



品牌识别系统 • Brand Identity System — 连续体 CONTINUUM

主标志以京张铁路人字形折返线为原型：一条折线贯穿三个节点圆（三区）。原创绘制，未使用现成商标或字体成品。Master mark abstracts the Jing-Zhang herringbone switchback: one polyline threading three node circles. Original drawing.

① 主标志与横排双语锁定 Master mark & horizontal lockup



字标与图形标间距锁定 =  $0.5 \times \text{图形标高度}$  • wordmark gap locked at  $0.5 \times \text{symbol height}$

② 竖排锁定 Vertical lockup



窄幅场景使用 • for narrow formats

③ 留白与最小尺寸 Clearspace & min size



最小尺寸 Min size: 印刷  $\geq 8 \text{ mm}$ ; 屏显  $\geq 24 \text{ px}$   
小于最小尺寸时仅使用图形标  
below min size use symbol only


④ 单色与反白 Monochrome & reversed



⑤ 标准色值 Color palette



⑥ 品牌层级体系 Brand hierarchy

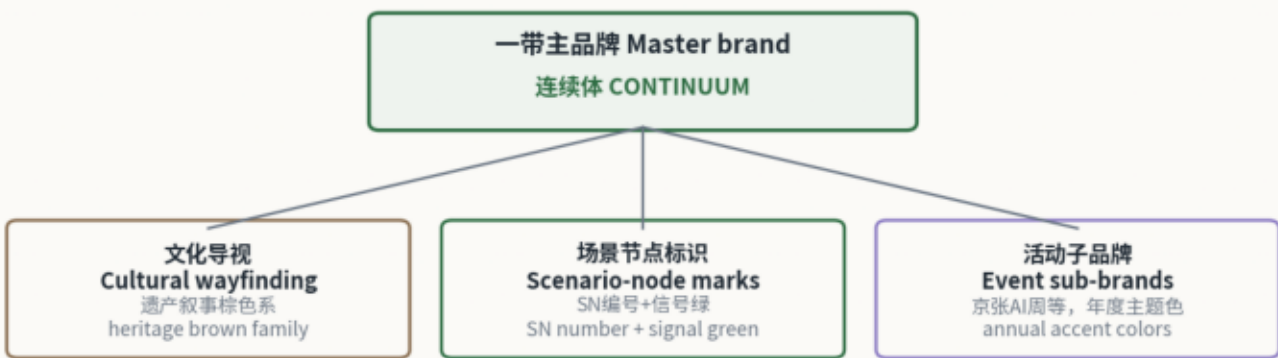


从属标识不得与主标志同尺寸并置 • subordinate marks never sit at equal size with the master mark

概念方案品牌建议，供专业团队深化；未注册商标，不构成商标权利声明。Conceptual brand suggestion for professional deepening; not a registered trademark and no trademark-right claim.

跨区域创新协同机制 • Cross-Regional Coordination — 一带五向 One Belt, Five Directions

本带作为海淀创新链条向全市与京津冀开放的接口装置；五向协同均为概念建议，须以各区意愿与正式协议为准，不构成任何机构承诺。All arrangements are conceptual suggestions pending each party's own decision and formal agreements.

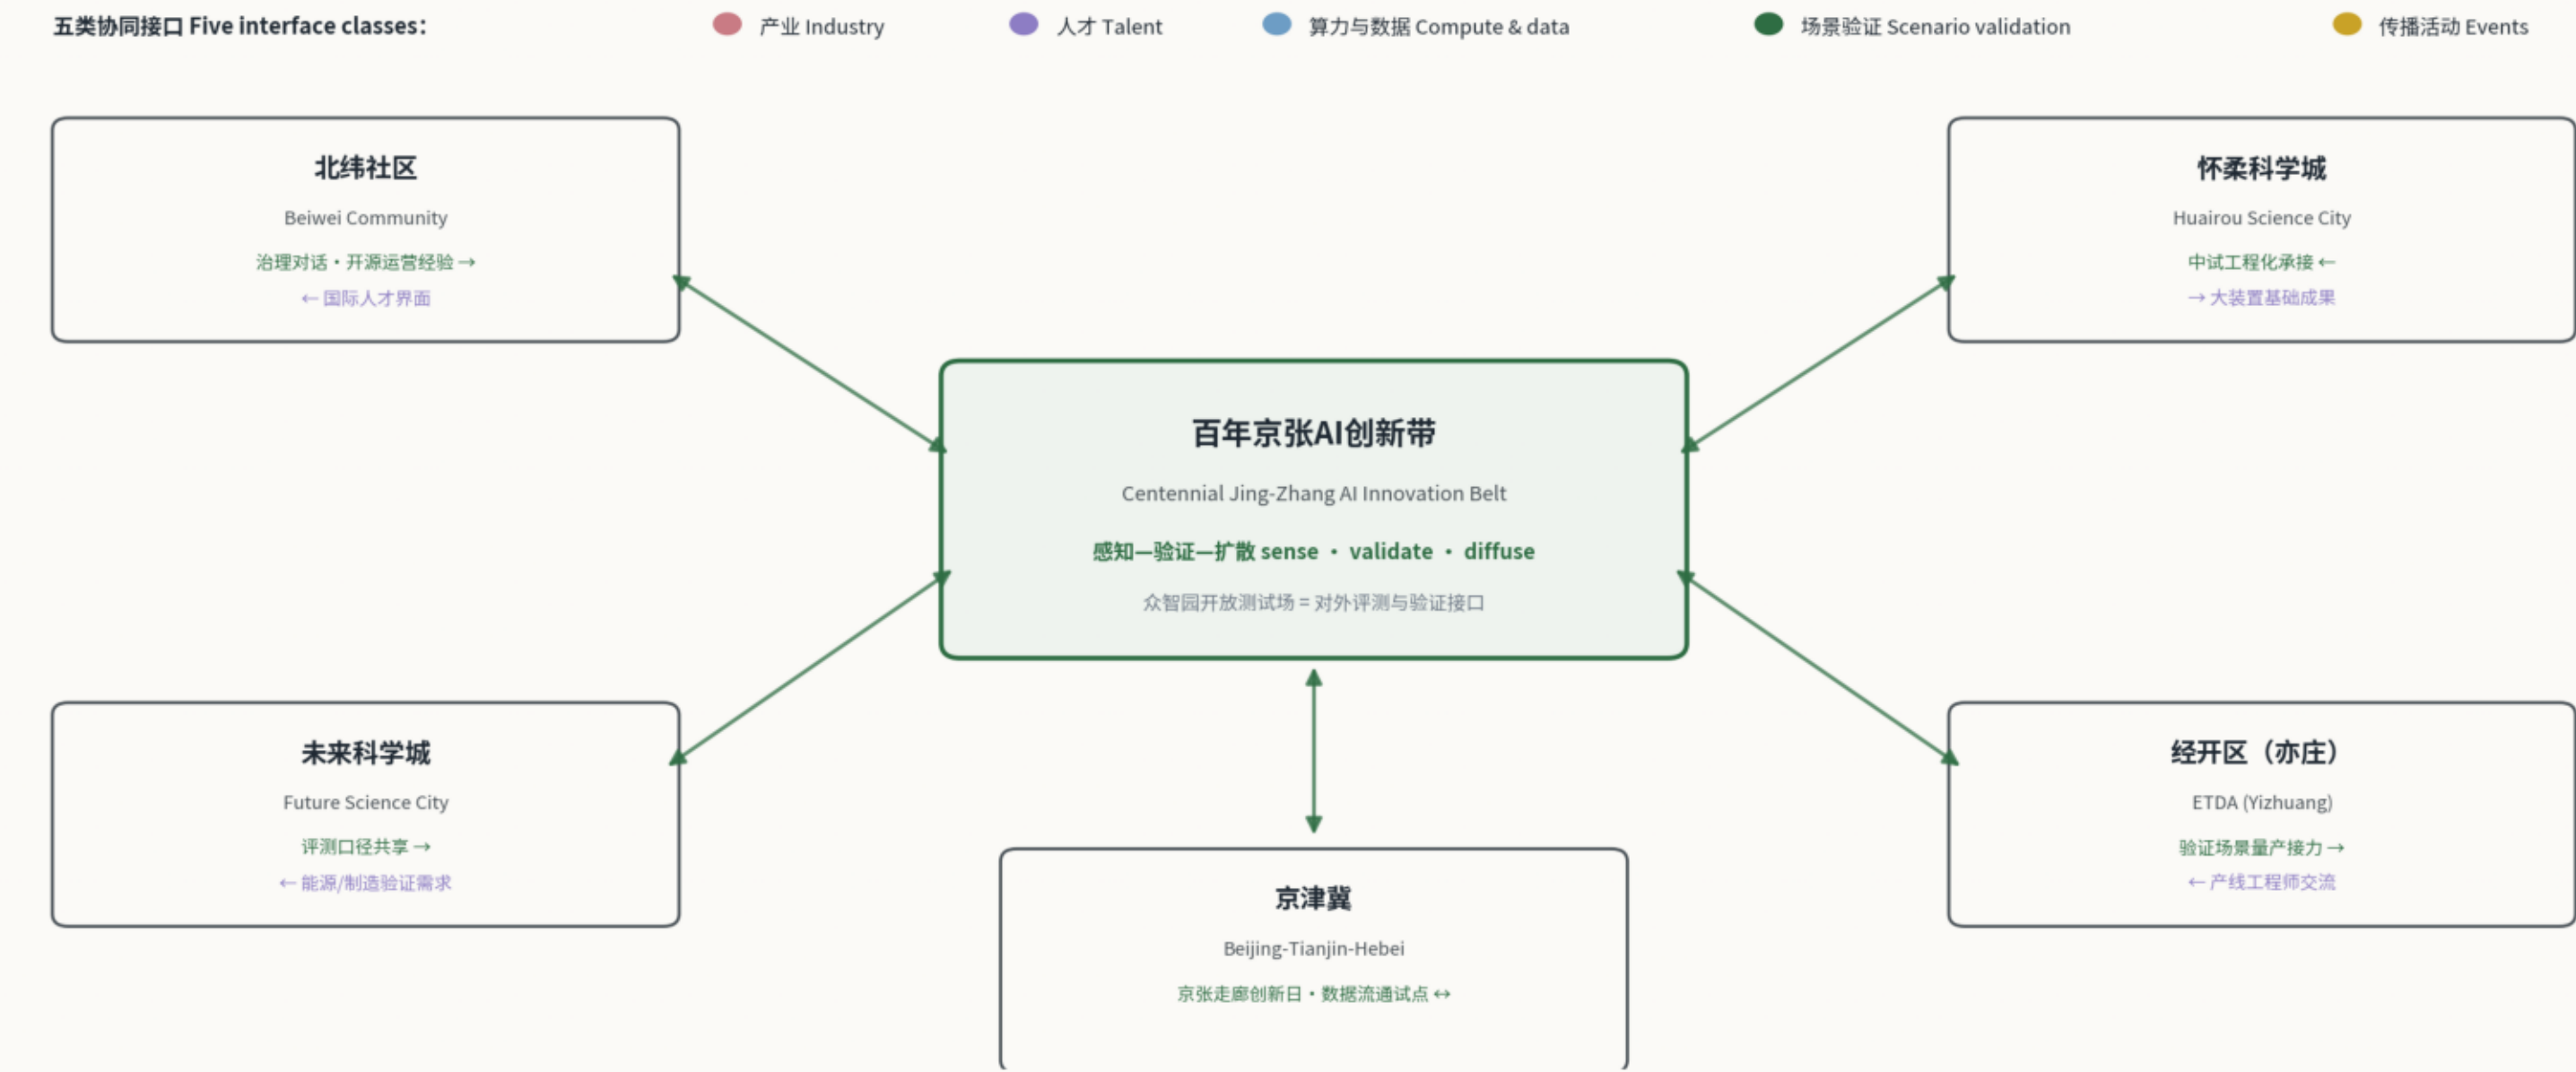

机制矩阵详见方案正文表格：产业（承接/输出）、人才（驻留/培养）、算力与数据（评测互认/合规流通）、场景验证（中试接力/异地复制）、传播活动（联办/走廊创新日）。See the mechanism matrix table in the proposal for the full partner × interface mapping.

概念示意图，非行政边界图；未使用任何官方边界数据。Conceptual diagram, not an administrative boundary map.



## 08 Scenario System & Implementation Outline

Twelve AI scenario cards (SN-01 to SN-12) line the heritage-park AI learning spine; SN-03 (compute & model open testbed), SN-07 (low-speed autonomous delivery loop) and SN-11 (Dazhongsi AI-native retail testbed) are the three industrial validation scenarios. All scenarios follow data minimization, visible on-site notice, and human reviewability.

Five personas: hardcore researchers / founders & engineers / AI-native youth / residents & elders / global visitors & developers.

Three AI pilgrimage landmarks: the Zhongzhiyuan Switchback Point governance tower • the Origin Community First Line of Code plaza • the Dazhongsi Bell-Sound Computing hall.

Concept phasing: near 4.66 km<sup>2</sup> (three ~60 ha priority catalysts: mid-spine demo stretch, Dazhongsi station plaza, Zhongzhiyuan AI Plaza) → mid 3.31 km<sup>2</sup> (stitching + community renewal) → long 3.45 km<sup>2</sup> (reserve + rolling renewal); 14 concept renewal projects — see the implementation and governance matrices in the proposal.

Long-term operations: annual Jing-Zhang AI Week global developer congress • quarterly scenario hackathons • standing AI-guided tours • two-tier governance of an operating company plus a developers' council. All items are conceptual suggestions, not established government arrangements.