


百年京张 AI 创新带城市设计 · 城市设计开源征集 · 概念方案

京张三叠

JINGZHANG TRIFOLD

一条走廊，叠印三次国家基础能力跃迁 —— 人的流动网络 → 知识生产网络 → 智能服务网络

铁轨层 RAIL 1909 · 学路层 ACADEMY 1952 · 智脉层 INTELLIGENCE 2020s | 一脊两廊三港 · 九程十站

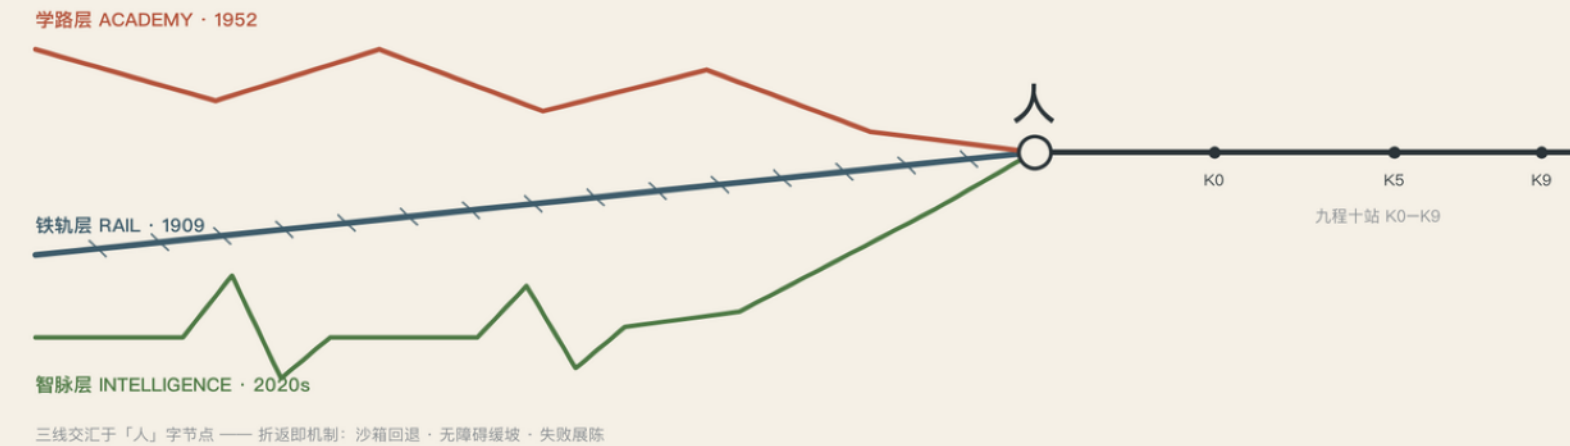

概念性参考方案 · provisional | 所有边界为临时替代边界，非官方红线，不替代法定规划 | 来源：征集方场地资料包 · 公开来源登记表



场地条带剪影（竖向 · 北在上）
南北约 9.7 km × 东西约 1.3 km
总体设计范围 11.41 km² (provisional)

京张三叠

JINGZHANG TRIFOLD — 铁轨 · 学路 · 智脉

铁轨层 RAIL LAYER · 1909

学路层 ACADEMY LAYER · 1952

智脉层 INTELLIGENCE MERIDIAN · 2020s

参赛账号 EndWithHyphen · 版本 v1.0 · 2026-08 · 许可 COMMUNITY-DISPLAY-ONLY

PROVISIONAL

PROVISIONAL · 本方案全部空间建议均为概念建议、参考方案，基于仓库登记的临时粗略边界生成；不替代正式规划，不构成政府审定结论；官方精确边界与重点区 polygon 发布后，全部面积指标须整体重算。

概念与结构 · 三叠叙事与空间骨架

铁轨层 · 1909

中国人自建的第一条干线铁路从这里出发，詹天佑以「人」字形折返线解决青龙桥坡度难题。铁轨层建起「人的流动网络」，是筑路人的层。

学路层 · 1952

院系调整建起学院路「八大学院」，与中关村中国科学院各研究所共同构成共和国第一次成体系部署的学科集群。学路层建起「知识生产网络」，是读书人的层，也是智脉层的使能条件。

智脉层 · 2020s

大钟寺—知春路—五道口一线聚集中国密度最高的 AI 企业群。智脉层正在建起「智能服务网络」——为 AI 而建，也必须为 AI 之后的下一代通用技术预留接口——具身智能、合成生物、量子计算的第一批住户尚未可知。

一脊 · 两廊 · 三港 · 九程十站

一脊

京张遗址公园主脊慢行绿道，南北纵贯、中心线约 9.6 公里，是铁轨层的实体载体与全带公共生活主轴。

两廊

东侧学院路—小月河复合廊（学脉界面讲「读书人」的故事，小月河蓝绿空间修复滨水生态并作低风险场景测试带，对应小月河场景赋能翼）；西侧中关村科创服务联络廊（对接中关村科技服务翼的要素与资本功能）。

三港

南港大钟寺·体验 / 中港原点社区·转化 / 北港众智园·加速，分别为铁轨、学路、智脉三层的叙事主场，按三叠协议在旗舰节点同时容纳历史证据、公共学习与可退出的 AI 服务。

九程十站

K0—K9 十座里程站标沿主脊布置，站间构成九段叙事里程；每处站标是一个场景、一件公共艺术、一段声景，把约十公里行走变成可步读的百年史。

空间结构总图 · 三层范围与用地概念

三层范围工作框架

统筹研究范围 · 约 43.6 km²

北至北五环、东至京藏高速、南至西直门外大街、西至万泉河路；只做产业战略与区域协同研究，不做空间落位结论。


总体设计范围 · 约 11.4 km²

京张遗址公园周边 1—2 公里城市地区；控规深度的城市设计，实算面积约 1141.28 万 m²（与公告口径偏差约 0.1%）。


重点区域范围 · 约 368.4 ha

北港众智园 / 中港原点社区 / 南港大钟寺，均达规划综合实施方案深度。

用地概念平衡（实算 · 临时边界口径）

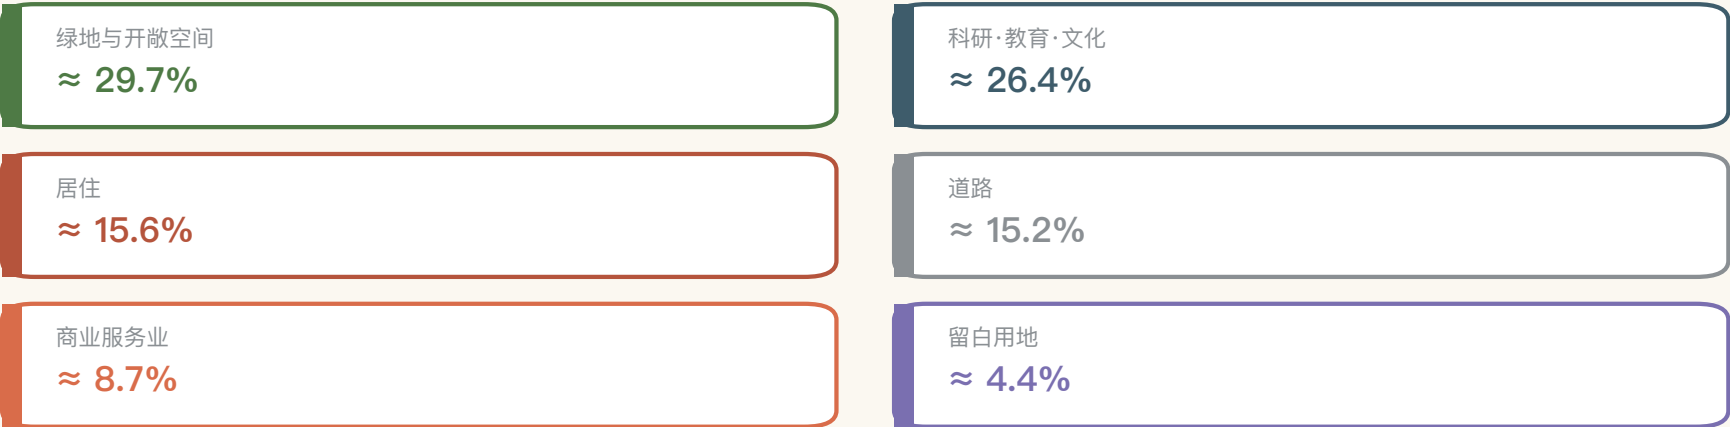

全部比例由提交的用地图层在 EPSG:4548 下实算得出；独立绿地图层口径绿地覆盖率约 29.5%，两口径并存披露。

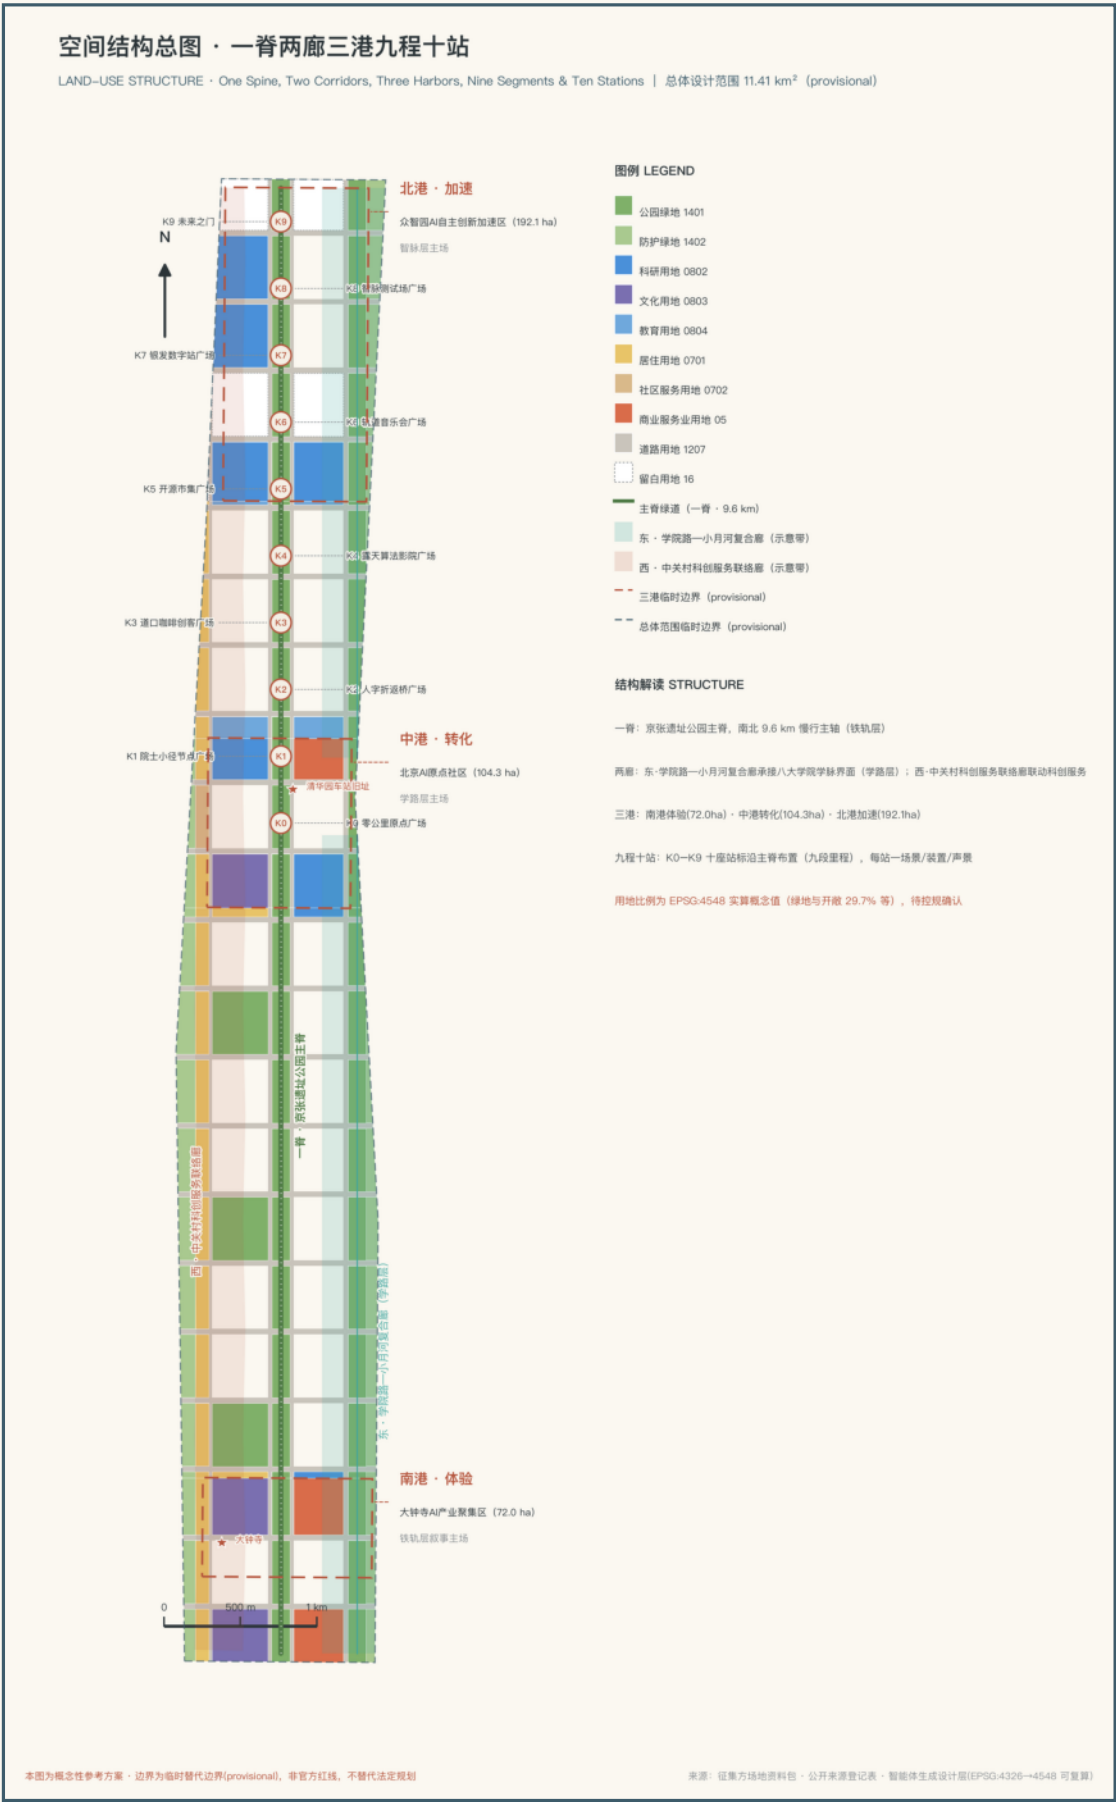

三港详细设计 · 三个叙事主场

南港 · 大钟寺AI产业聚集区（实算约 72.0 ha）

铁轨层叙事主场 · 全带的「出发厅」

定位：百年记忆与智能原生消费的叠合客厅。「一广场一装置一市集」——南港城市客厅广场衔接大钟寺地铁枢纽；「新钟」光声装置让永乐大钟声纹与AI 城市音景对话，是全带唯一主地标与听觉识别系统核心；开源市集与无人零售试验街构成智能原生消费带。按三叠协议同时容纳历史证据、公共学习与可退出的 AI 服务。风险：商业权属复杂，以协商式微更新为主，避免大拆大建假设。

中港 · 北京AI原点社区（实算约 104.3 ha）

学路层叙事主场 · 全带的「零公里」

定位：知识转化为生态的枢纽，中国 AI 的「原点」。「一原点一桥一径」——K0 零公里原点广场是本带步行叙事系统的概念零公里（京张铁路史实里程起点在丰台柳村一带，不在本地地），叠印「AI 原点」纪念意义；人字折返桥借「折返」智慧组织无障碍缓坡与「问题—试验—失败—修正」展陈；院士小径以 AR 导览讲述八大学院与中关村科学家故事。风险：多主体权属与既有园区运营，概念建议需与运营方协商深化。

北港 · 众智园AI自主创新加速区（实算约 192.9 ha）

智脉层叙事主场 · 面向未来的「加速港」

定位：全栈自主创新体系的空间承载，下一代通用技术的预留接口。「一场一门一留白」——智脉测试场为可重构开放测试单元；K9 未来之门为可穿行、可停留的谦逊门槛构筑物，夜间以低亮度光脉冲示意「下一段走廊」，不做高识别度造型地标；约 4.4% 留白用地预留给「AI 之后」的通用技术。风险：临近五环路，建设条件与生态约束需专业核实；留白启用规则应由治理机制明确。

三处重点区 polygon 为临时粗略矩形，矩形边不得解释为地块或道路红线；内部结构设计均为方向性表达。

三港索引图 · 重点地段概念结构


京张三叠 Jingzhang Trifold | 南港体验 × 中港转化 × 北港加速 | 41 处概念体量原型投 concept_role 分色 —— 子图由主脊绿道串联（竖向）

主脊绿道 SPINE

北港 · 加速

众智园AI自主创新加速区 (192.1 ha)


智脉层主场

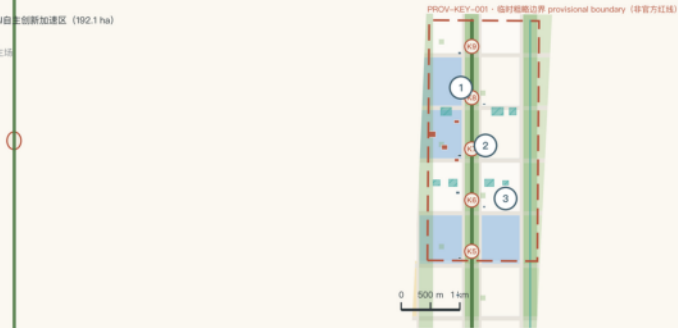

中港 · 转化

北京AI原点社区 (104.3 ha)


学路层主场

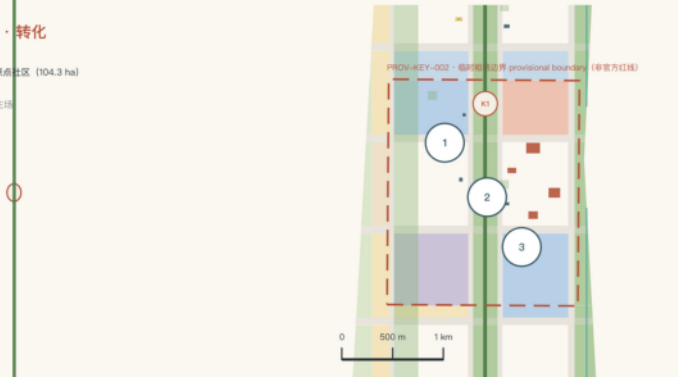

南港 · 体验

大钟寺AI产业聚集区 (72.0 ha)

铁轨层叙事主场

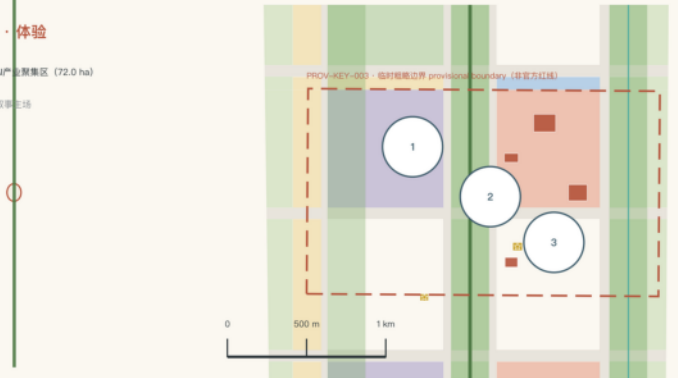

本图为概念性参考方案，边界为临时替代边界(provisional), 非官方红线，不替代法定规划

来源：征集方场地资料包，公开来源登记表，智脉层生成设计图(SP5G-4320--4548 可复算)

概念结构 CONCEPT

一场 · 通用技术测试场(T3机器人操场)

一门 · K9未来之门

一留白 · 第四次浪潮接口预留

三叠协议席位 TRIFOLD PROTOCOL

历史证据 × 公共学习

× 可退出AI服务 (人工复核，可回避)

概念结构 CONCEPT

一原点 · K0零公里原点广场

一桥 · 人字折返桥+清华园站记忆度

一径 · 院士小径AR学路

三叠协议席位 TRIFOLD PROTOCOL

历史证据 × 公共学习

× 可退出AI服务 (人工复核，可回避)

概念结构 CONCEPT

一广场 · 新钟城市客厅

一装置 · 永乐大钟声纹+AI音景

一市集 · 智能原生消费市集

三叠协议席位 TRIFOLD PROTOCOL

历史证据 × 公共学习

× 可退出AI服务 (人工复核，可回避)

概念体量原型 CONCEPT VOLUMES · 41 处

站桥配套体量 ×15

渠·城市客厅界面体量 ×14

地标配套体量 ×5

可量构测试模块 ×7

场景卡与用户画像 · AI 藏在背后，人站在台前

编号	场景	位置	服务对象
S1	站台晨读 · AI 陪伴自习亭	K1 及站台公园	学生
S2	院士小径 AR 导览	学脉廊	游客/学生
S3	道口咖啡 · 开发者客厅	中港	开发者
S4	夜行守护照明	主脊全线	晚归者/居民
S5	记忆采集车	三港巡回	老居民

编号	场景	位置	服务对象
S6	银发数字站	南港+社区	老年人
S7	露天算法影院	K4 站台公园	市民
S8	开源市集	南港	创客/市民
S9	轨道音乐会	K6/人字桥	市民
S10	无障碍触觉音景	主脊全线	视障人士等

产业测试验证场景（概念测试性质 · 可中止 · 可回退）

T1 · TEST

低速无人配送测试段：小月河蓝绿廊（东缘）时段化测试区，公开测试规则与事故处置流程。

T2 · TEST

AI 音乐生成公开测试场：以轨道音乐会为载体，全部曲目标注生成方式与授权状态。

T3 · TEST

城市服务机器人候场单元：北港「先候场、再上线」，通过安全评估与公众公示方可进入开放区域。

六类用户画像

老居民 · 场地记忆的守护者

高校学生 · 学路的主人

AI 研究员与开发者 · 需要社区与算力

国际创业者 · 需要一站式落地服务

亲子家庭与游客 · 安全有趣的公共体验

晚归通勤者 · 亮着灯的回家路

旗舰场景深化（完整机制设计 · 其余保持配套卡片深度）

S4 夜行守护照明

输入仅为匿名人流密度与照度传感，不设人脸识别、端侧处理 24 小时滚动删除；失败退回定时全亮模式。近期试点：主脊南段 1 公里。

S5 记忆采集车

预约—上门采集—本人确认—授权入库—可选展示；AI 仅做转写初筛，每份档案人工核对署名、可随时撤回。近期试点：南港 2—3 个社区。

T3 机器人候场单元

企业申请—安全评估—候场公示测试—公众反馈—转正或退出；测试报告公开，事故即终止并恢复公共空间。近期试点：北港 M1—M3 模块。

隐私总边界：全带场景不设人脸识别；个人数据默认端侧处理；每个场景均有明确数据边界、人工复核与退出机制。

蓝绿网络 · 慢行系统与城市地标

蓝绿骨架与慢行

主脊公园带（约 120 米宽连续绿廊）与东缘小月河蓝绿廊南北并置构成「双纵」，二十一条缝合街形成东西向公共连接，叠加十个 K 节点口袋公园与二十一处站台公园街旁广场，形成「大道—公园—广场」三级公共空间体系。独立绿地图层实算覆盖率约 29.5%，用地平衡口径约 29.7%。

主脊慢行绿道纵贯全带约 9.6 公里，串联 K0—K9 十座站标（九程十站）；小月河滨水骑行道构成东侧第二条慢行纵线；二十一条「缝合街」以约 500 米间距东西向穿越廊道（七条兼作车行次干道，其余为纯慢行街）。

AI 朝圣地标（一主地标+三公共记忆与贡献节点 · 均为概念建议）

主地标 · 「新钟」光声装置

南港：六百年永乐大钟声纹与 AI 生成城市音景的实时对话装置，全带听觉识别系统核心，全带唯一主地标。

① 零公里原点广场 · 公共记忆节点


K0 · 中港：本带叙事零公里（概念编号，非京张铁路史实里程原点）；地面以 1435 毫米标准轨距做铺装刻线，供人停留集会。

② 人字折返桥与老站记忆馆 · 公共记忆节点

K2 附近：无障碍缓坡与「问题—试验—失败—修正」展陈让「折返」成为可体验的机制；桥下记忆馆展示清华园老站口述史与铁路遗物。

③ K9 未来之门 · 公共记忆节点

北港北端：可穿行、可停留的谦逊门槛构筑物，夜间以低亮度光脉冲向北示意「下一段走廊」，不做高识别度造型地标。

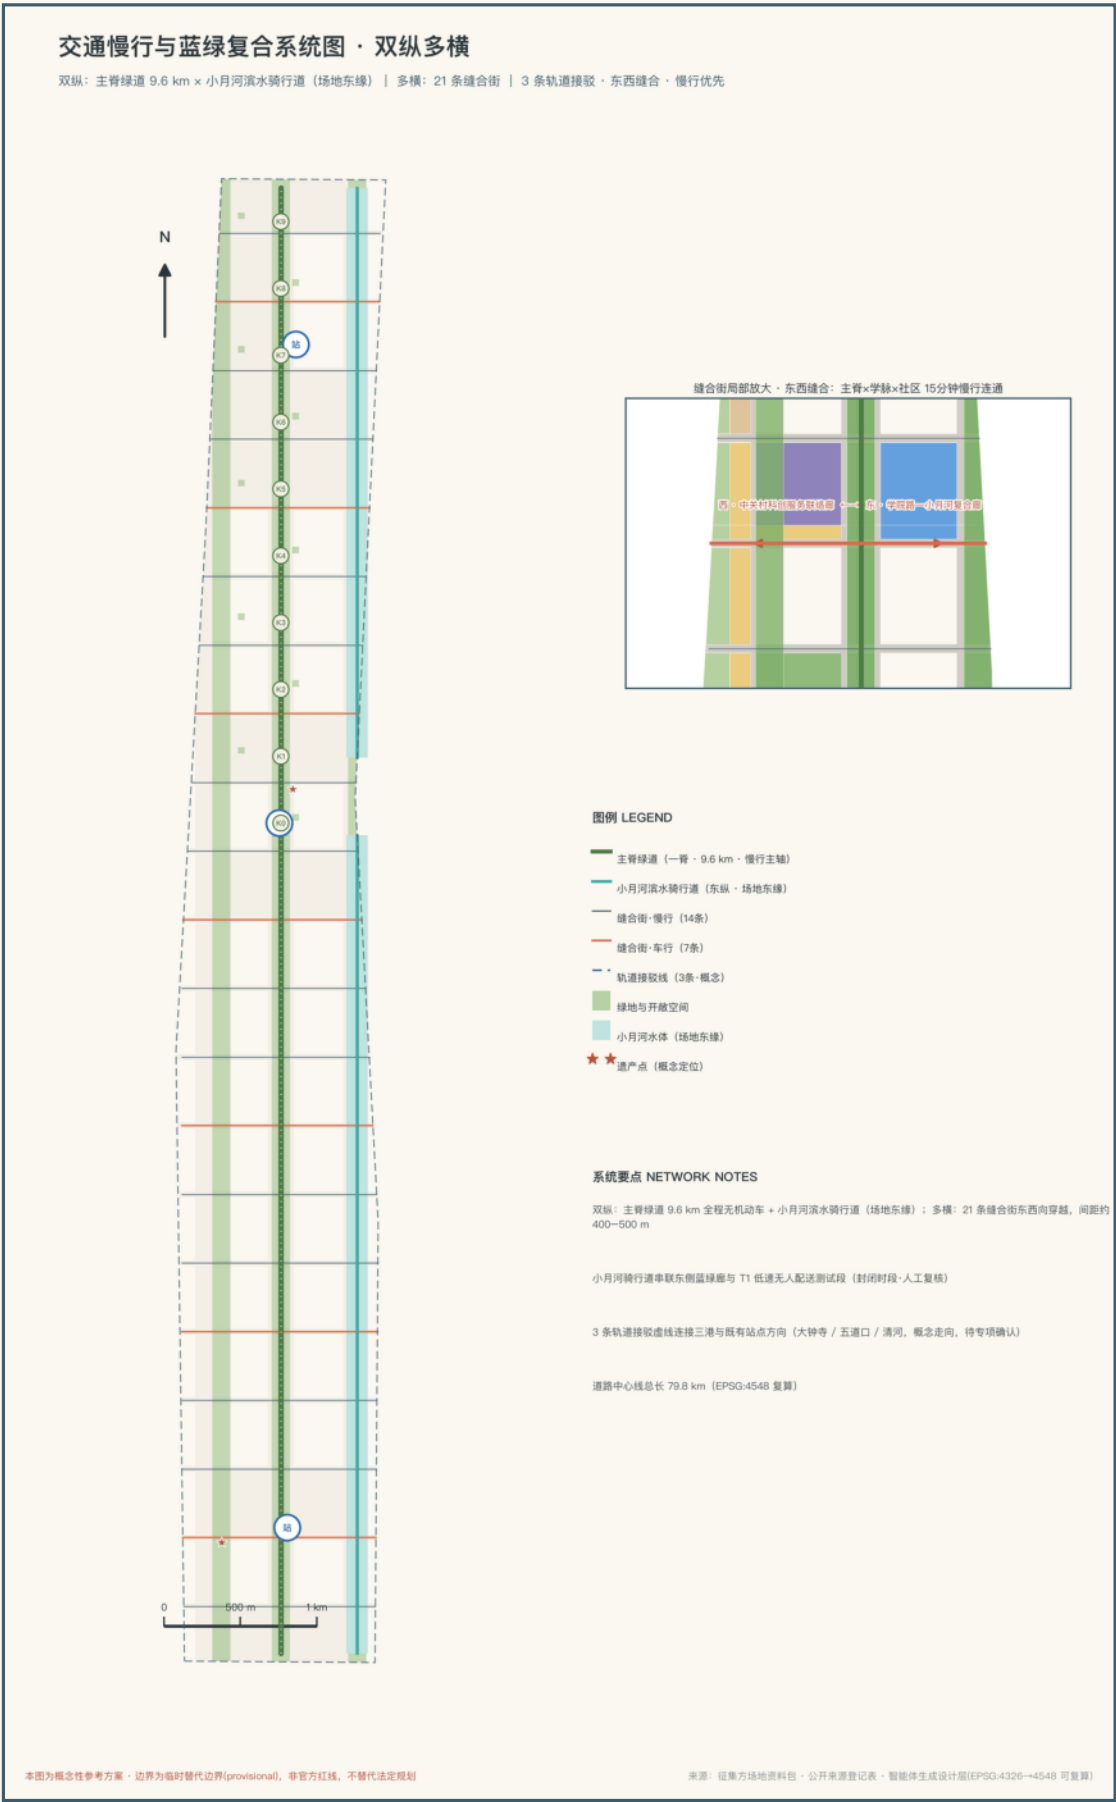


指标体系 · 面积复算与实施分期



证据 · 资料来源与合规声明

资料来源（公开登记表分级使用）

- ① 北京市规划自然资源委海淀分局：资格预审公告（2026-05-09）
- ② 用户提供并清权：面向全球智能体的开源征集任务书摘录（2026-05-18）
- ③ 北京市科委·中关村管委会：「三区两翼」打造世界级AI集聚地（2026-04-03）
- ④ 教育部：《北京学院路上八大学院》（2009-08-24）
- ⑤ 北京日报：京张铁路历史零公里核查（2026-08-11）；「三区两翼」布局报道
- ⑥ 中国铁路官网：京张铁路文化遗产资料（「人」字形折返线路位于青龙桥站）
- ⑦ 住建部《城市设计管理办法》（2017）；自然资源部《用地用海分类指南》（2023）
- ⑧ 《无障碍环境建设法》（2023）；七部门《生成式人工智能服务管理暂行办法》（2023）
- ⑨ 海淀区融媒：北京AI原点社区集聚规模报道（2026-07-29，宣传口径背景数据）
- ⑩ 仓库登记：临时粗略边界与三处重点区 polygon + 公开来源登记表

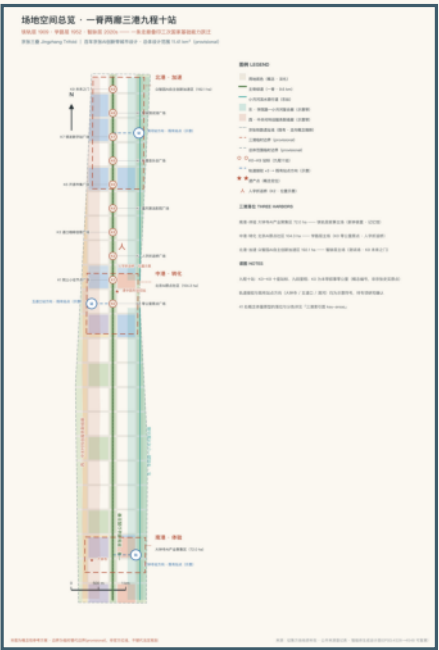

Provisional 边界声明

截至提交，组织方尚未公布官方精确边界与重点区 polygon。本方案场地边界与三处重点区均采用仓库登记的临时粗略边界，仅用于 AI 生成、可视化与本地自检，不得解释为官方红线、审批依据或精确面积依据；官方 polygon 发布后，用地、建筑、道路、绿地、公共空间、分期与全部面积指标都需整体重算。

指标可复算说明

全部面积类指标由提交的 GeoJSON 在 EPSG:4548（CGCS2000 三度带，中央经线 117°E）下以多边形面积实算；比例类指标以临时边界实算面积为分母；任何第三方可用同样方法复现。机器审计层完整保存于 sources.json · metrics.json · compliance_matrix.json · standard_matrix.json · design_depth_matrix.json · geometry/*.geojson。

概念建议边界条款

本方案不代表任何政府审定、审批或实施承诺；所有空间建议均为概念建议；临时边界不作红线；容积率、高度、拆改留、线位、容量、投资与时序均不作最终结论；所有测试场景不构成已批准运营；涉及资金、政策、招商的表述均为深化方向，不构成任何政府承诺。

版权与 AI 生成责任

仅使用公开或已清权资料；全部图件、标识与图形为 AI 生成或原创绘制的概念表达，未使用未经授权的字、商标、人物肖像与版权图像。本方案由 AI 智能体生成、经人类概念方向讨论确认，最终判断权属于人类与专业团队（共创宪章第七条）。完整版权说明见 report/copyright_statement.md。