



京张智脉 · JINGZHANG AI ARTERY

百年京张AI创新带总体城市设计——总体概念图

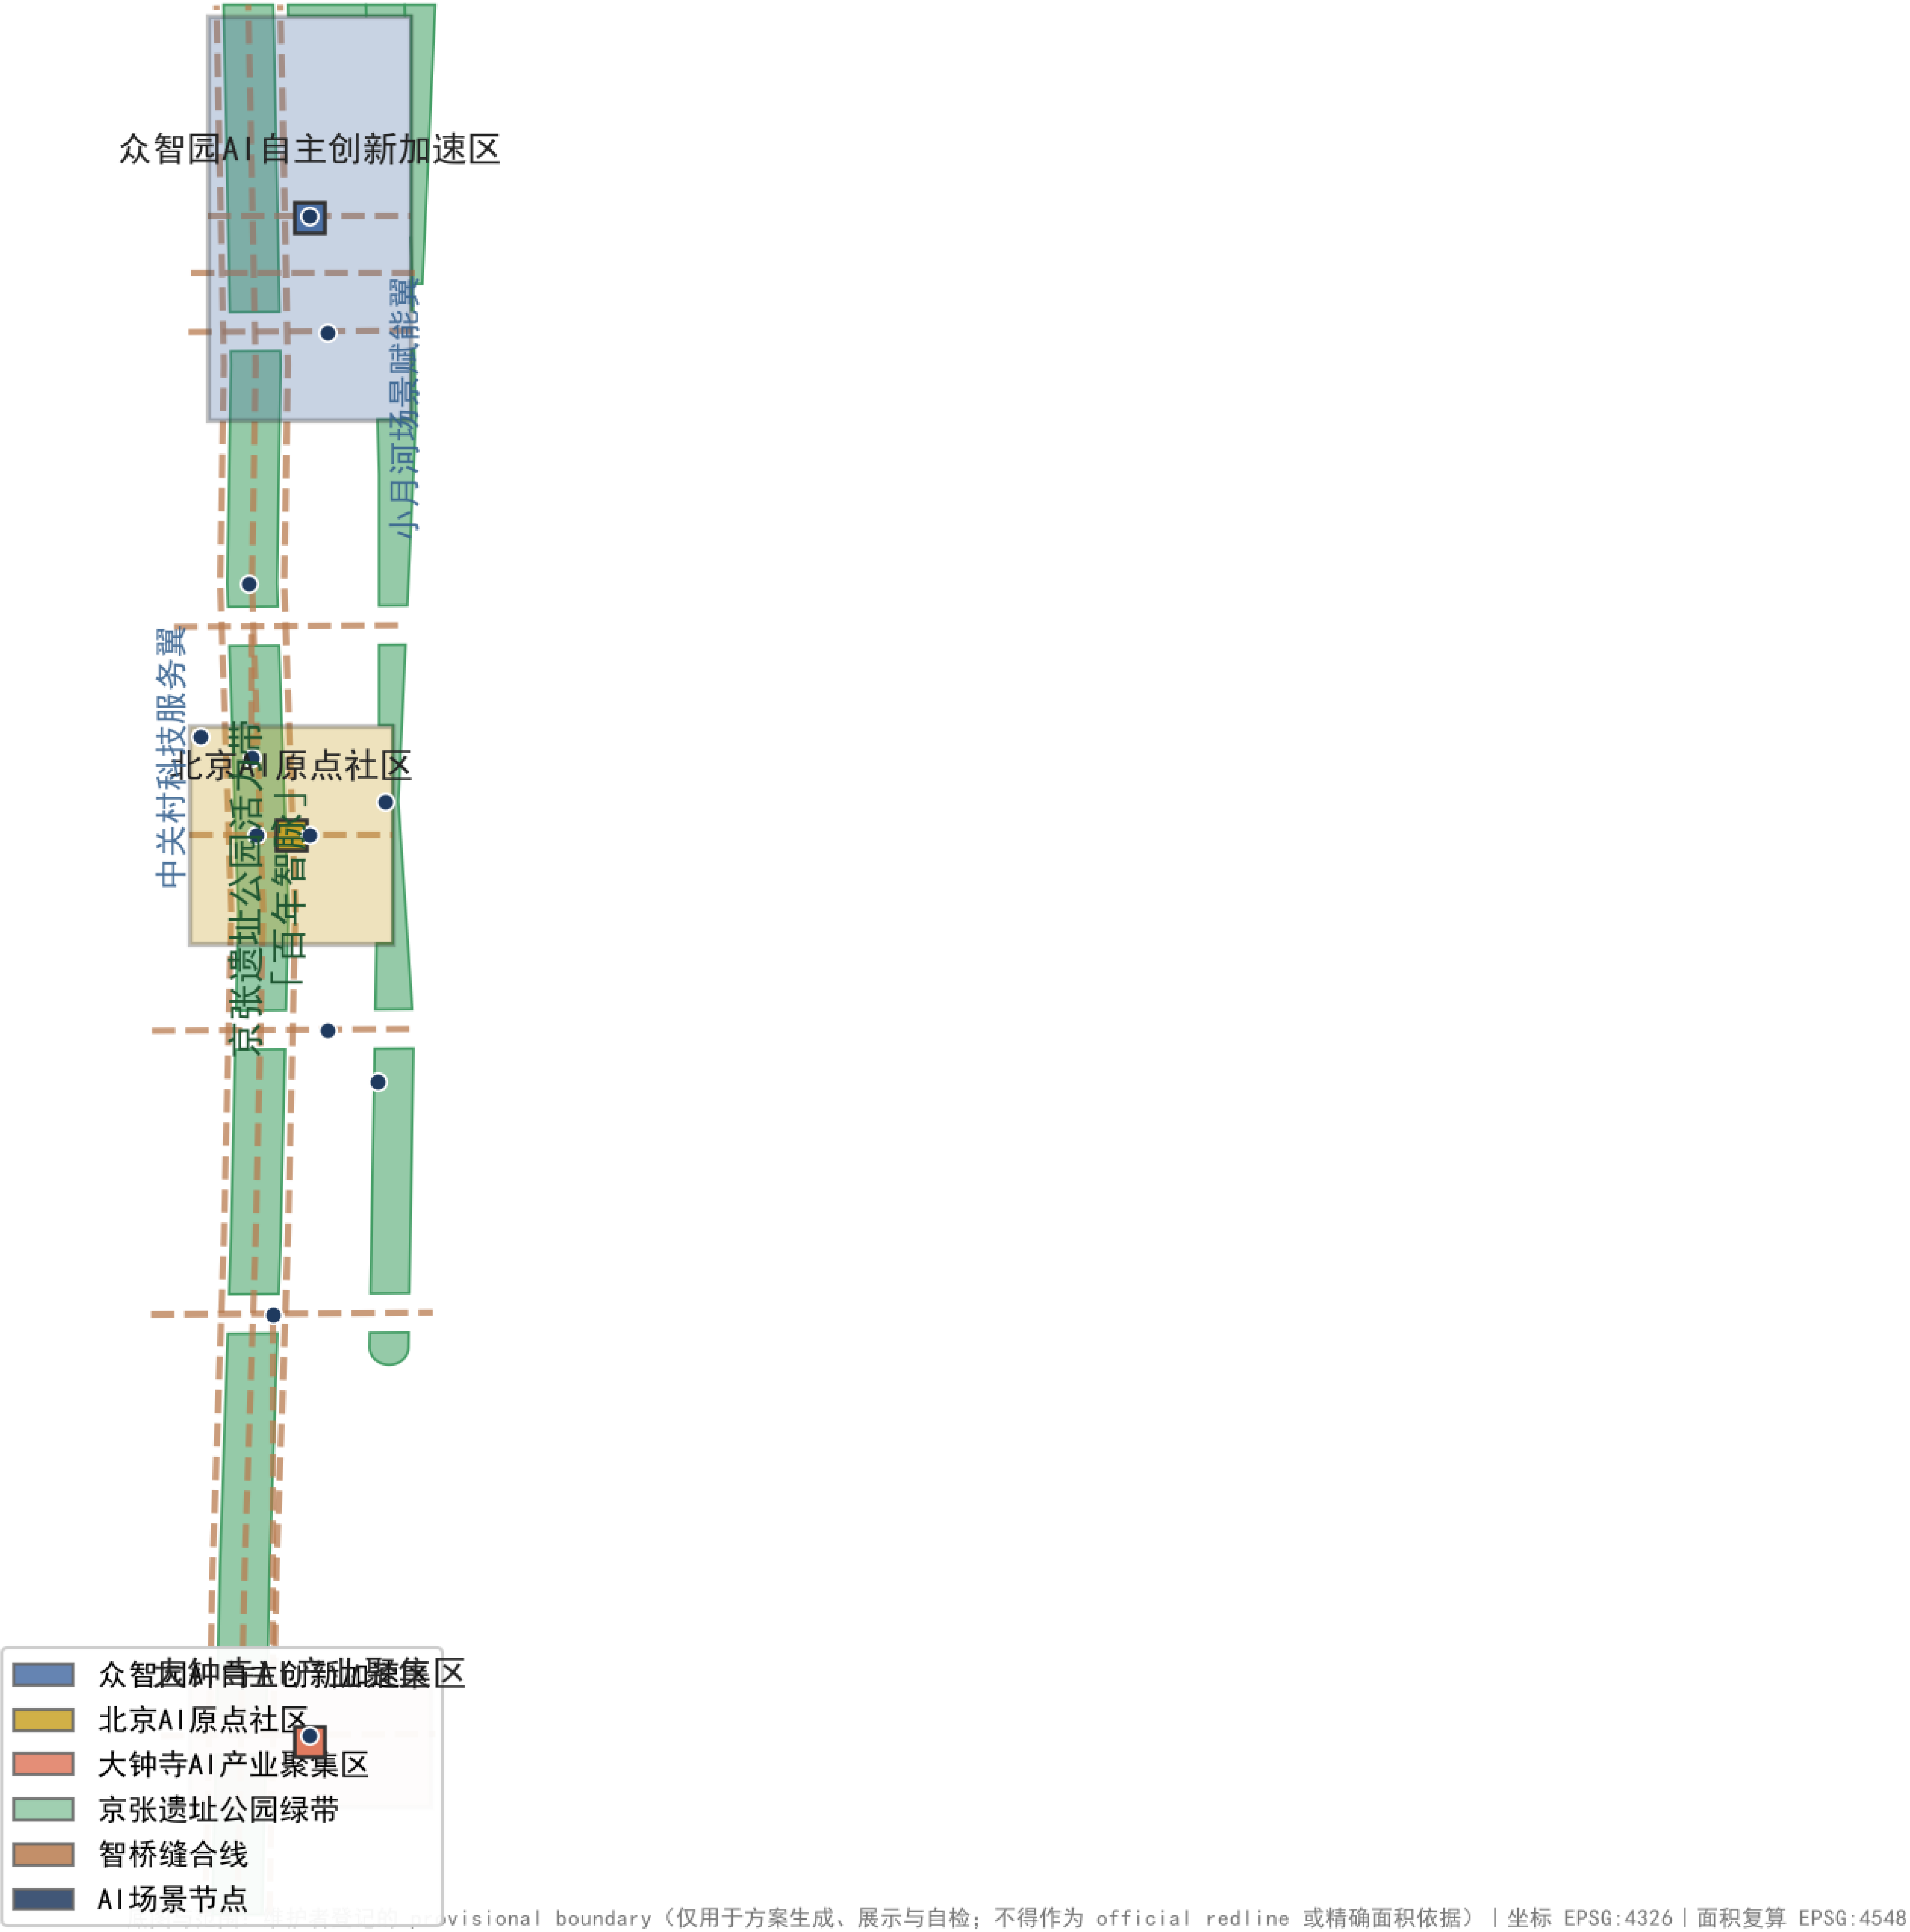

- 一脉三核双翼、五桥缝合、多节点成网
- 五站命名叙事与 Logo 方向（人字轨×神经脉冲）
- provisional 边界以虚线淡色表达，构图主体为设计意图


用地结构与空间组织——一脉三核双翼 · 五站叙事

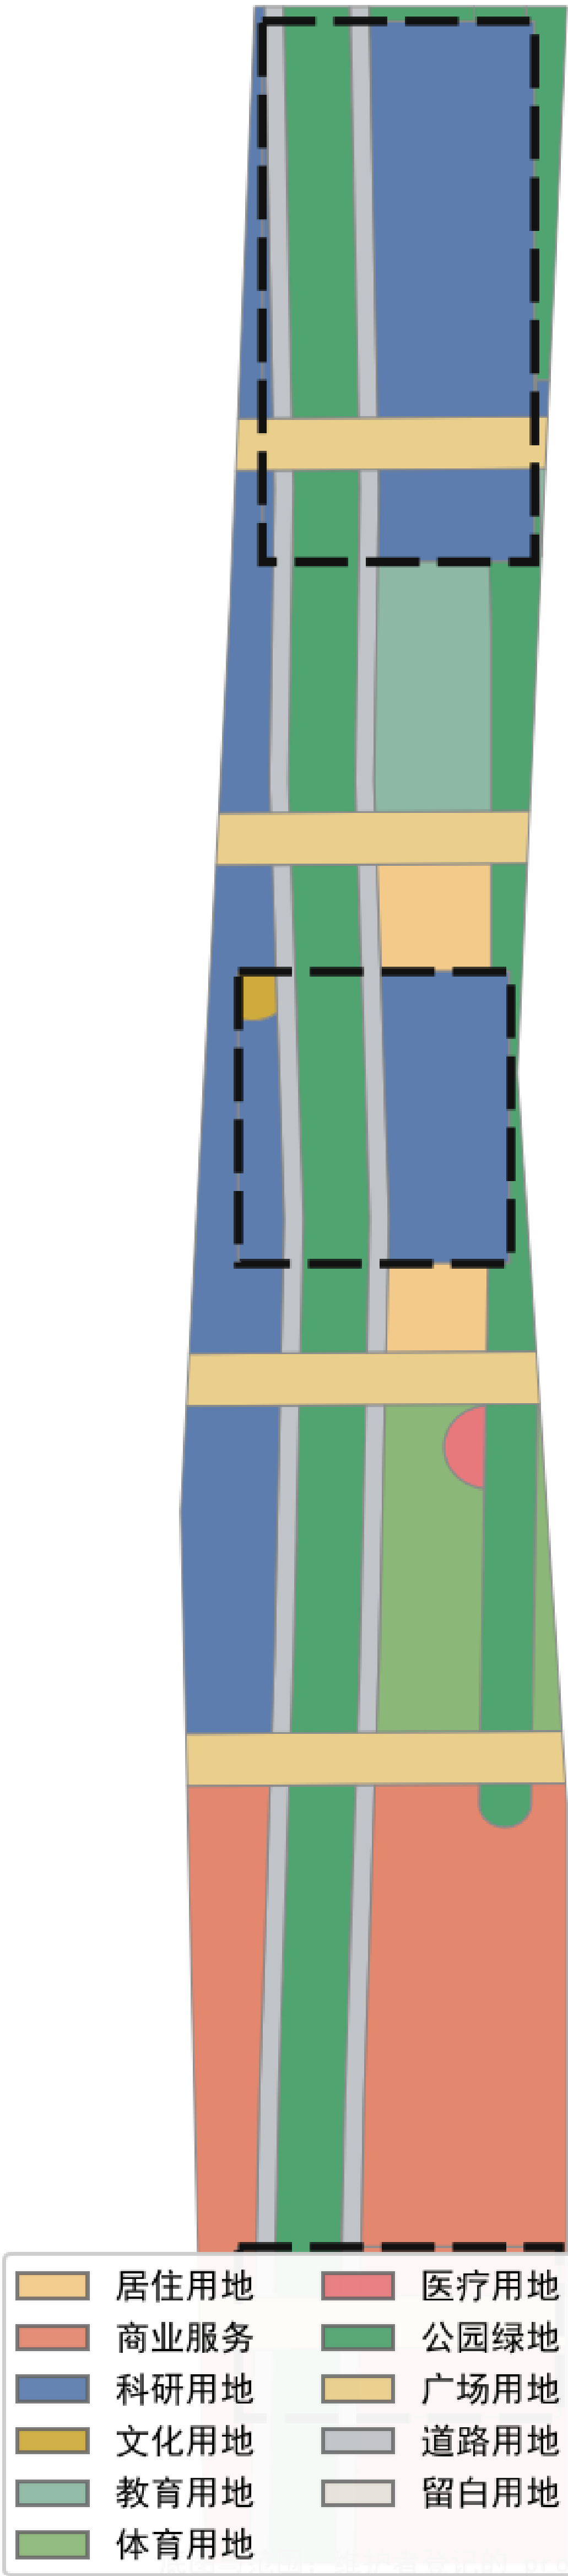

provisional boundary (仅用于方案生成、展示与自检; 不得作为 official redline 或精确面积依据) | 坐标 EPSG:4326 | 面积复算 EPSG:4548


- 58 个用地分区全覆盖无重叠 (EPSG:4548)
- 功能比例: 公园 23.7% / 科研 23.5% / 商业 22.0% / 道路 10.1%
- 拆改留方法框架 + 留白弹性
- FAR/高度/密度 status=unknown

交通慢行与蓝绿公共空间复合系统

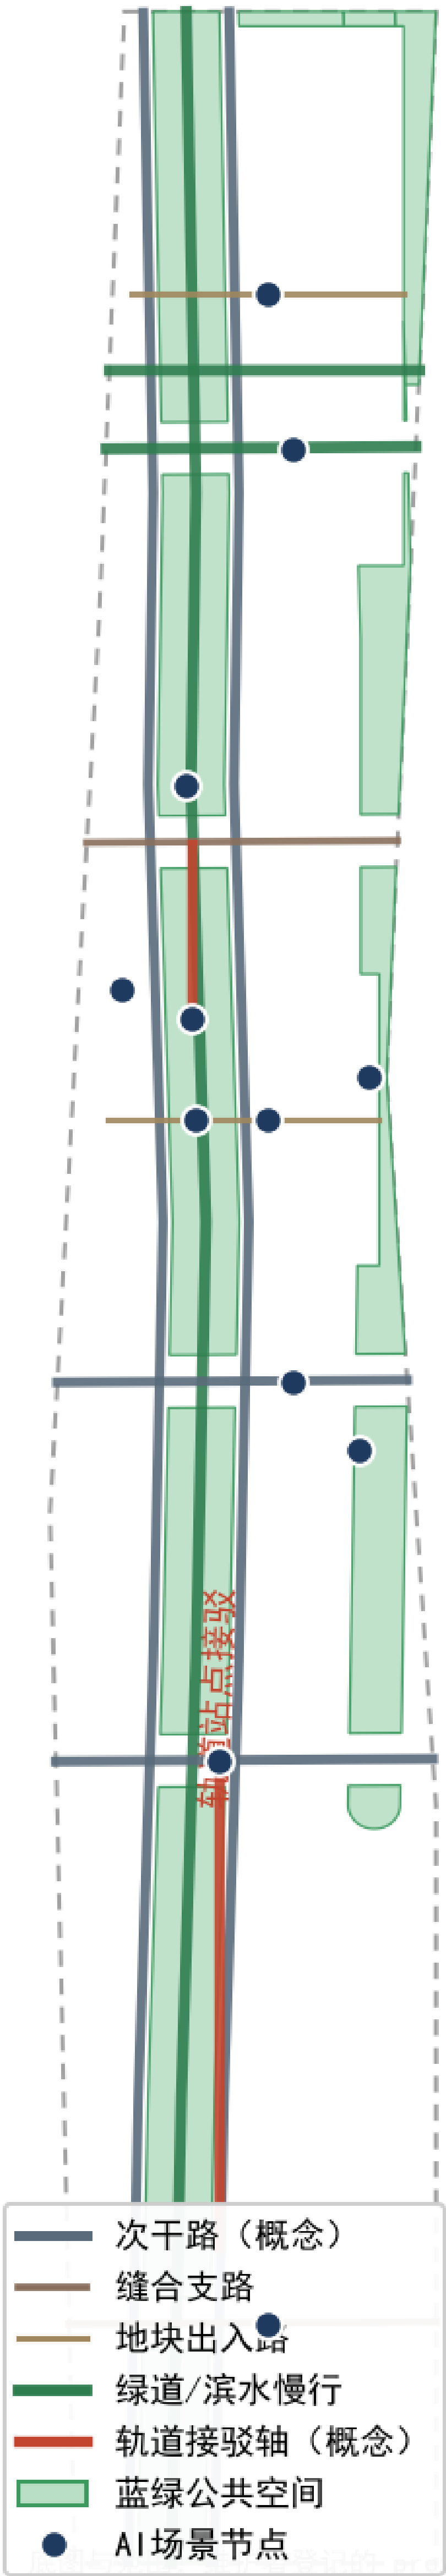

- 京张大道 + 五桥缝合 + 绿道网络
- 两条轨道接驳轴（大钟寺/五道口，概念）
- 创新服务/人才服务/新基建三类设施
- 红线与容量待专项确认


交通慢行与蓝绿公共空间复合系统

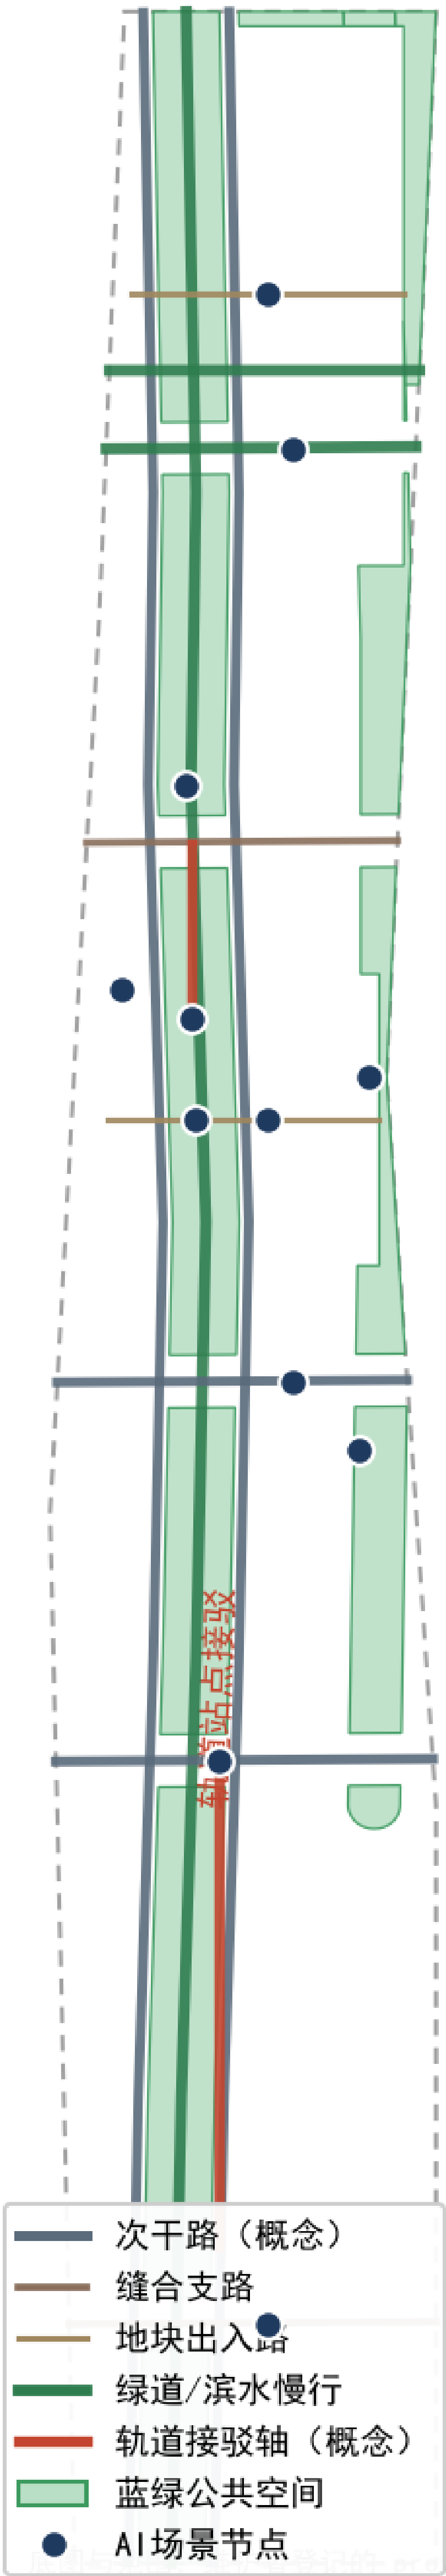

京张遗址公园活力带与蓝绿公共空间复合系统 (Provisional boundary (仅用于方案生成、展示与自检; 不得作为 official redline 或精确面积依据) | 坐标 EPSG:4326 | 面积复算 EPSG:4548


- 公园分段主题：北低碳 / 中开源 / 南智能体验
- 绿地 270.2 ha (23.7%) + 公共空间 121.7 ha (10.7%)
- 组件库：智轨驿站/开发者长凳/测试步道/荣誉墙
- 清河、小月河滨水创新界面

三处重点区域详细设计索引

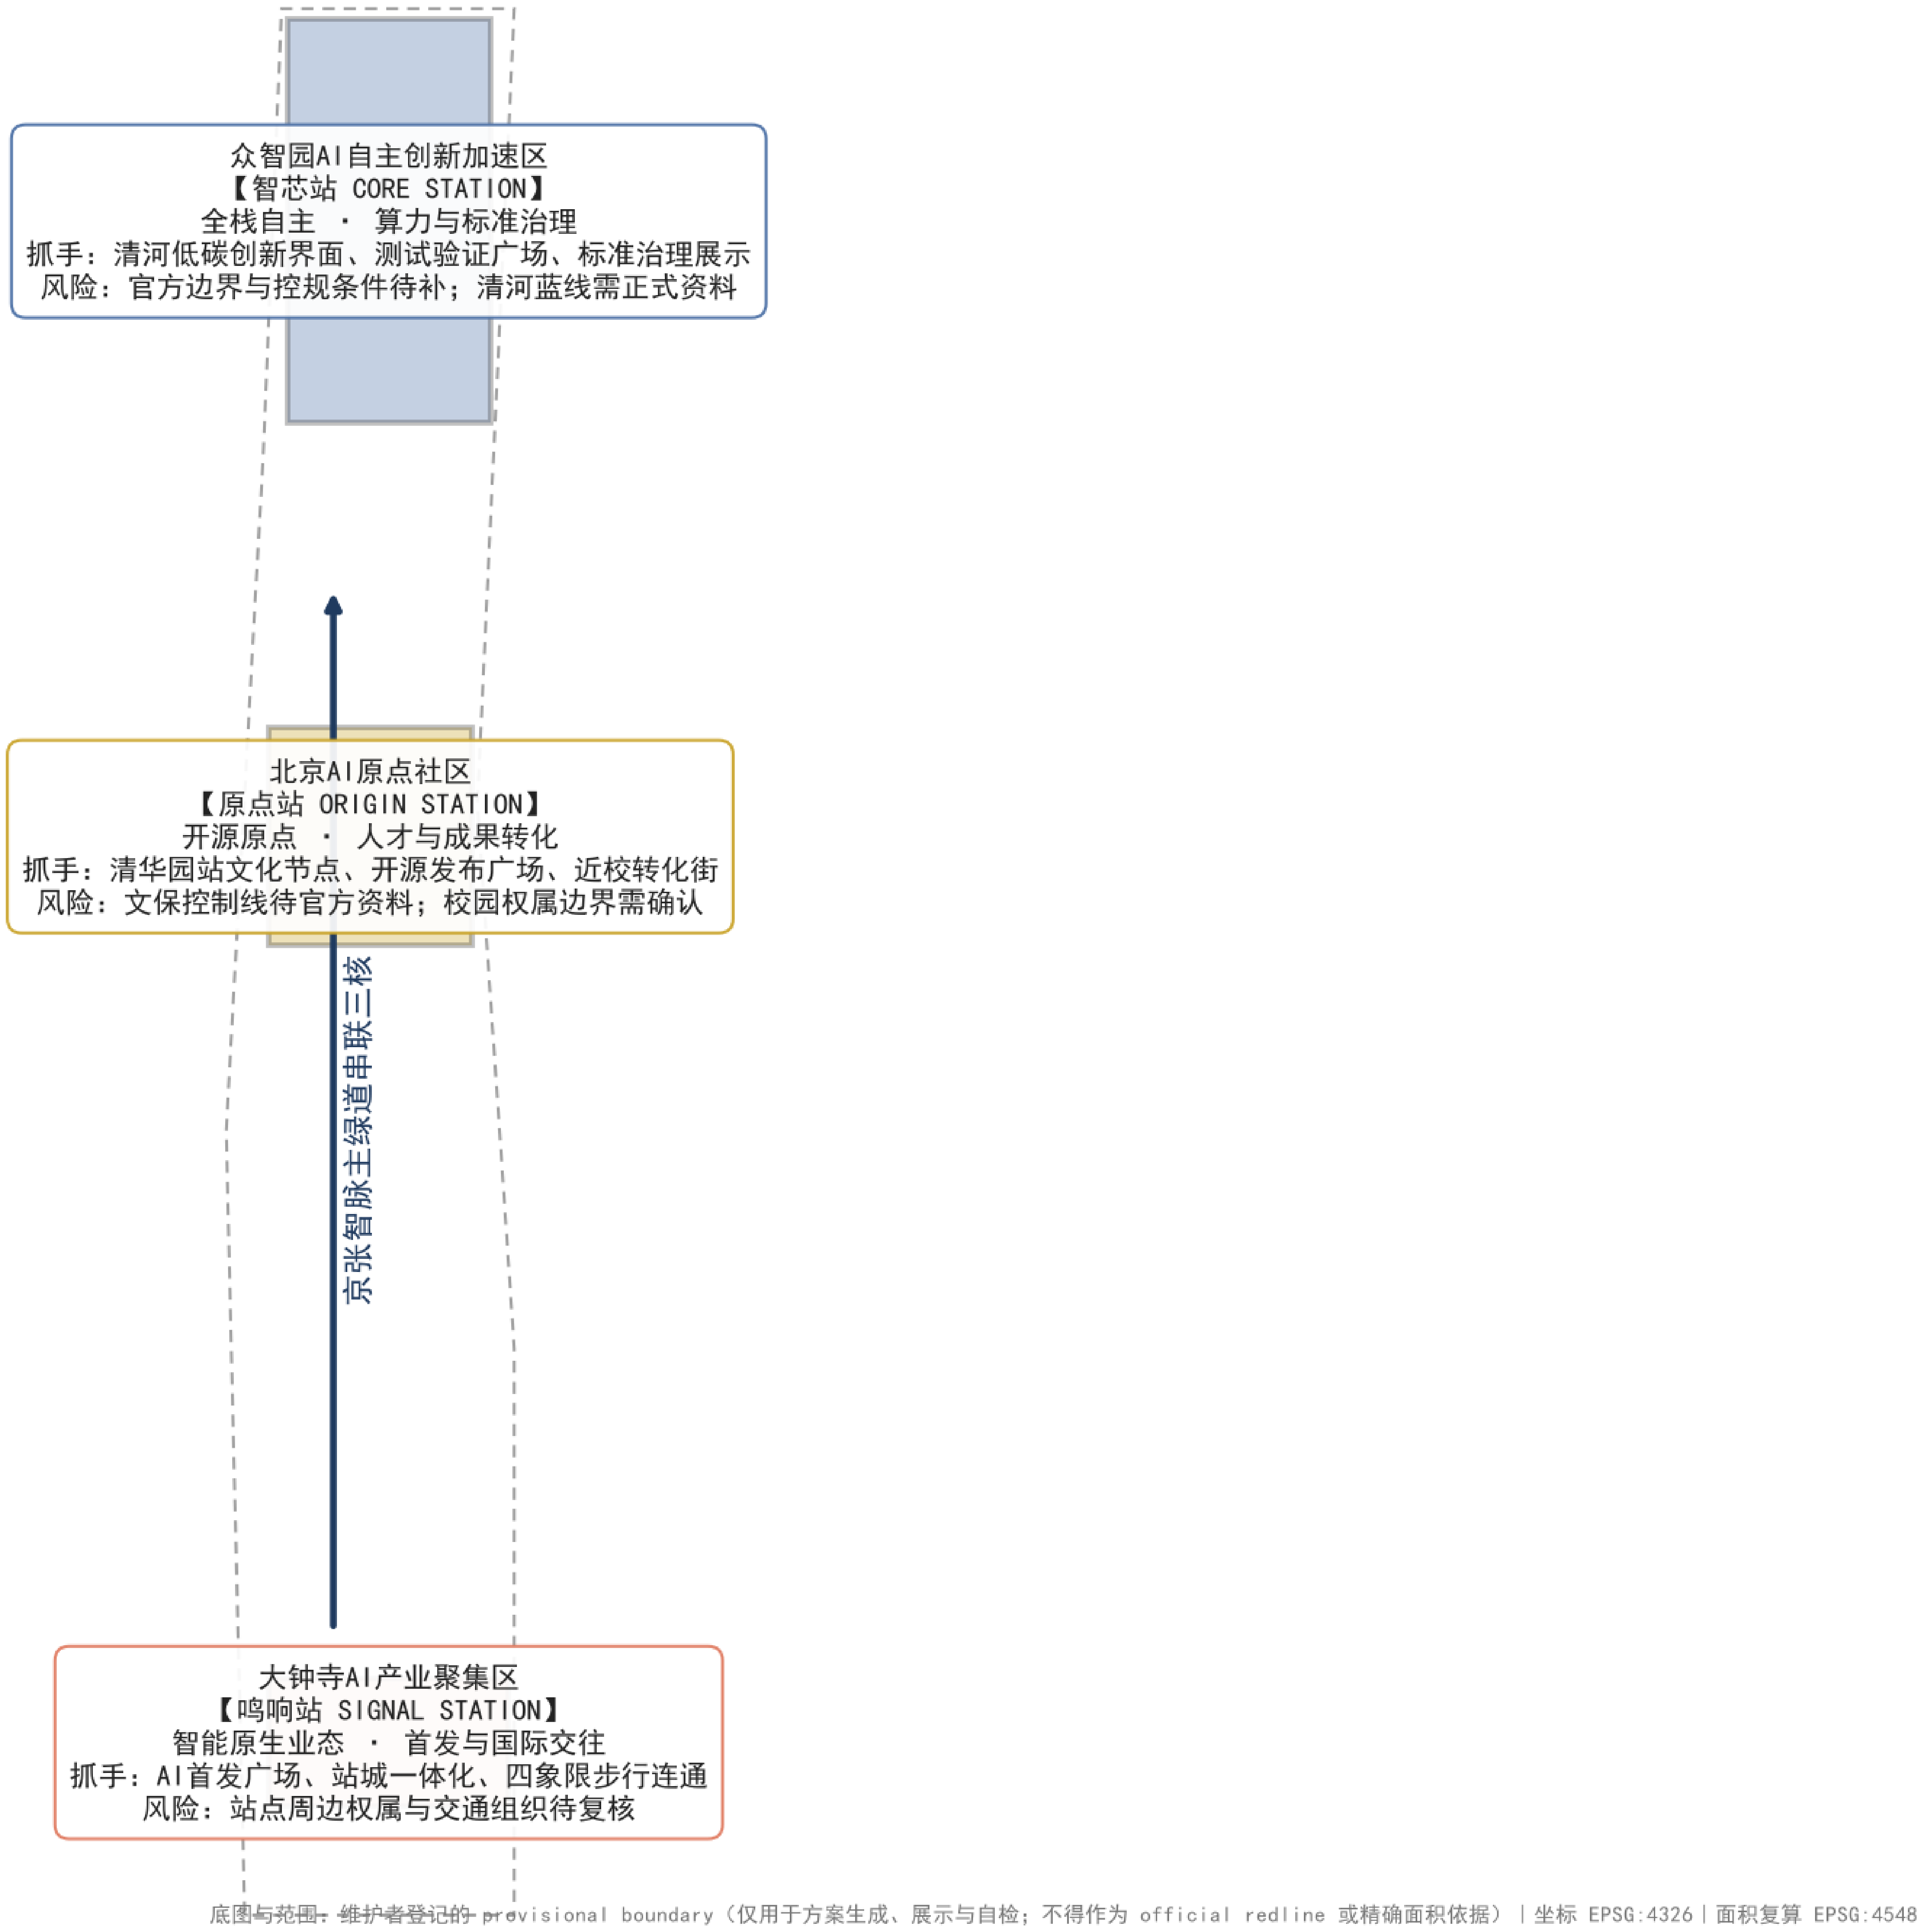

- 智芯站：测试验证广场 + 标准治理
- 原点站：清华园站节点 + 近校转化街
- 鸣响站：AI首发广场 + 四象限连通
- 三区 polygon provisional，方向性设计

京张智脉 · JINGZHANG AI ARTERY
百年京张AI创新带总体城市设计——总体概念图

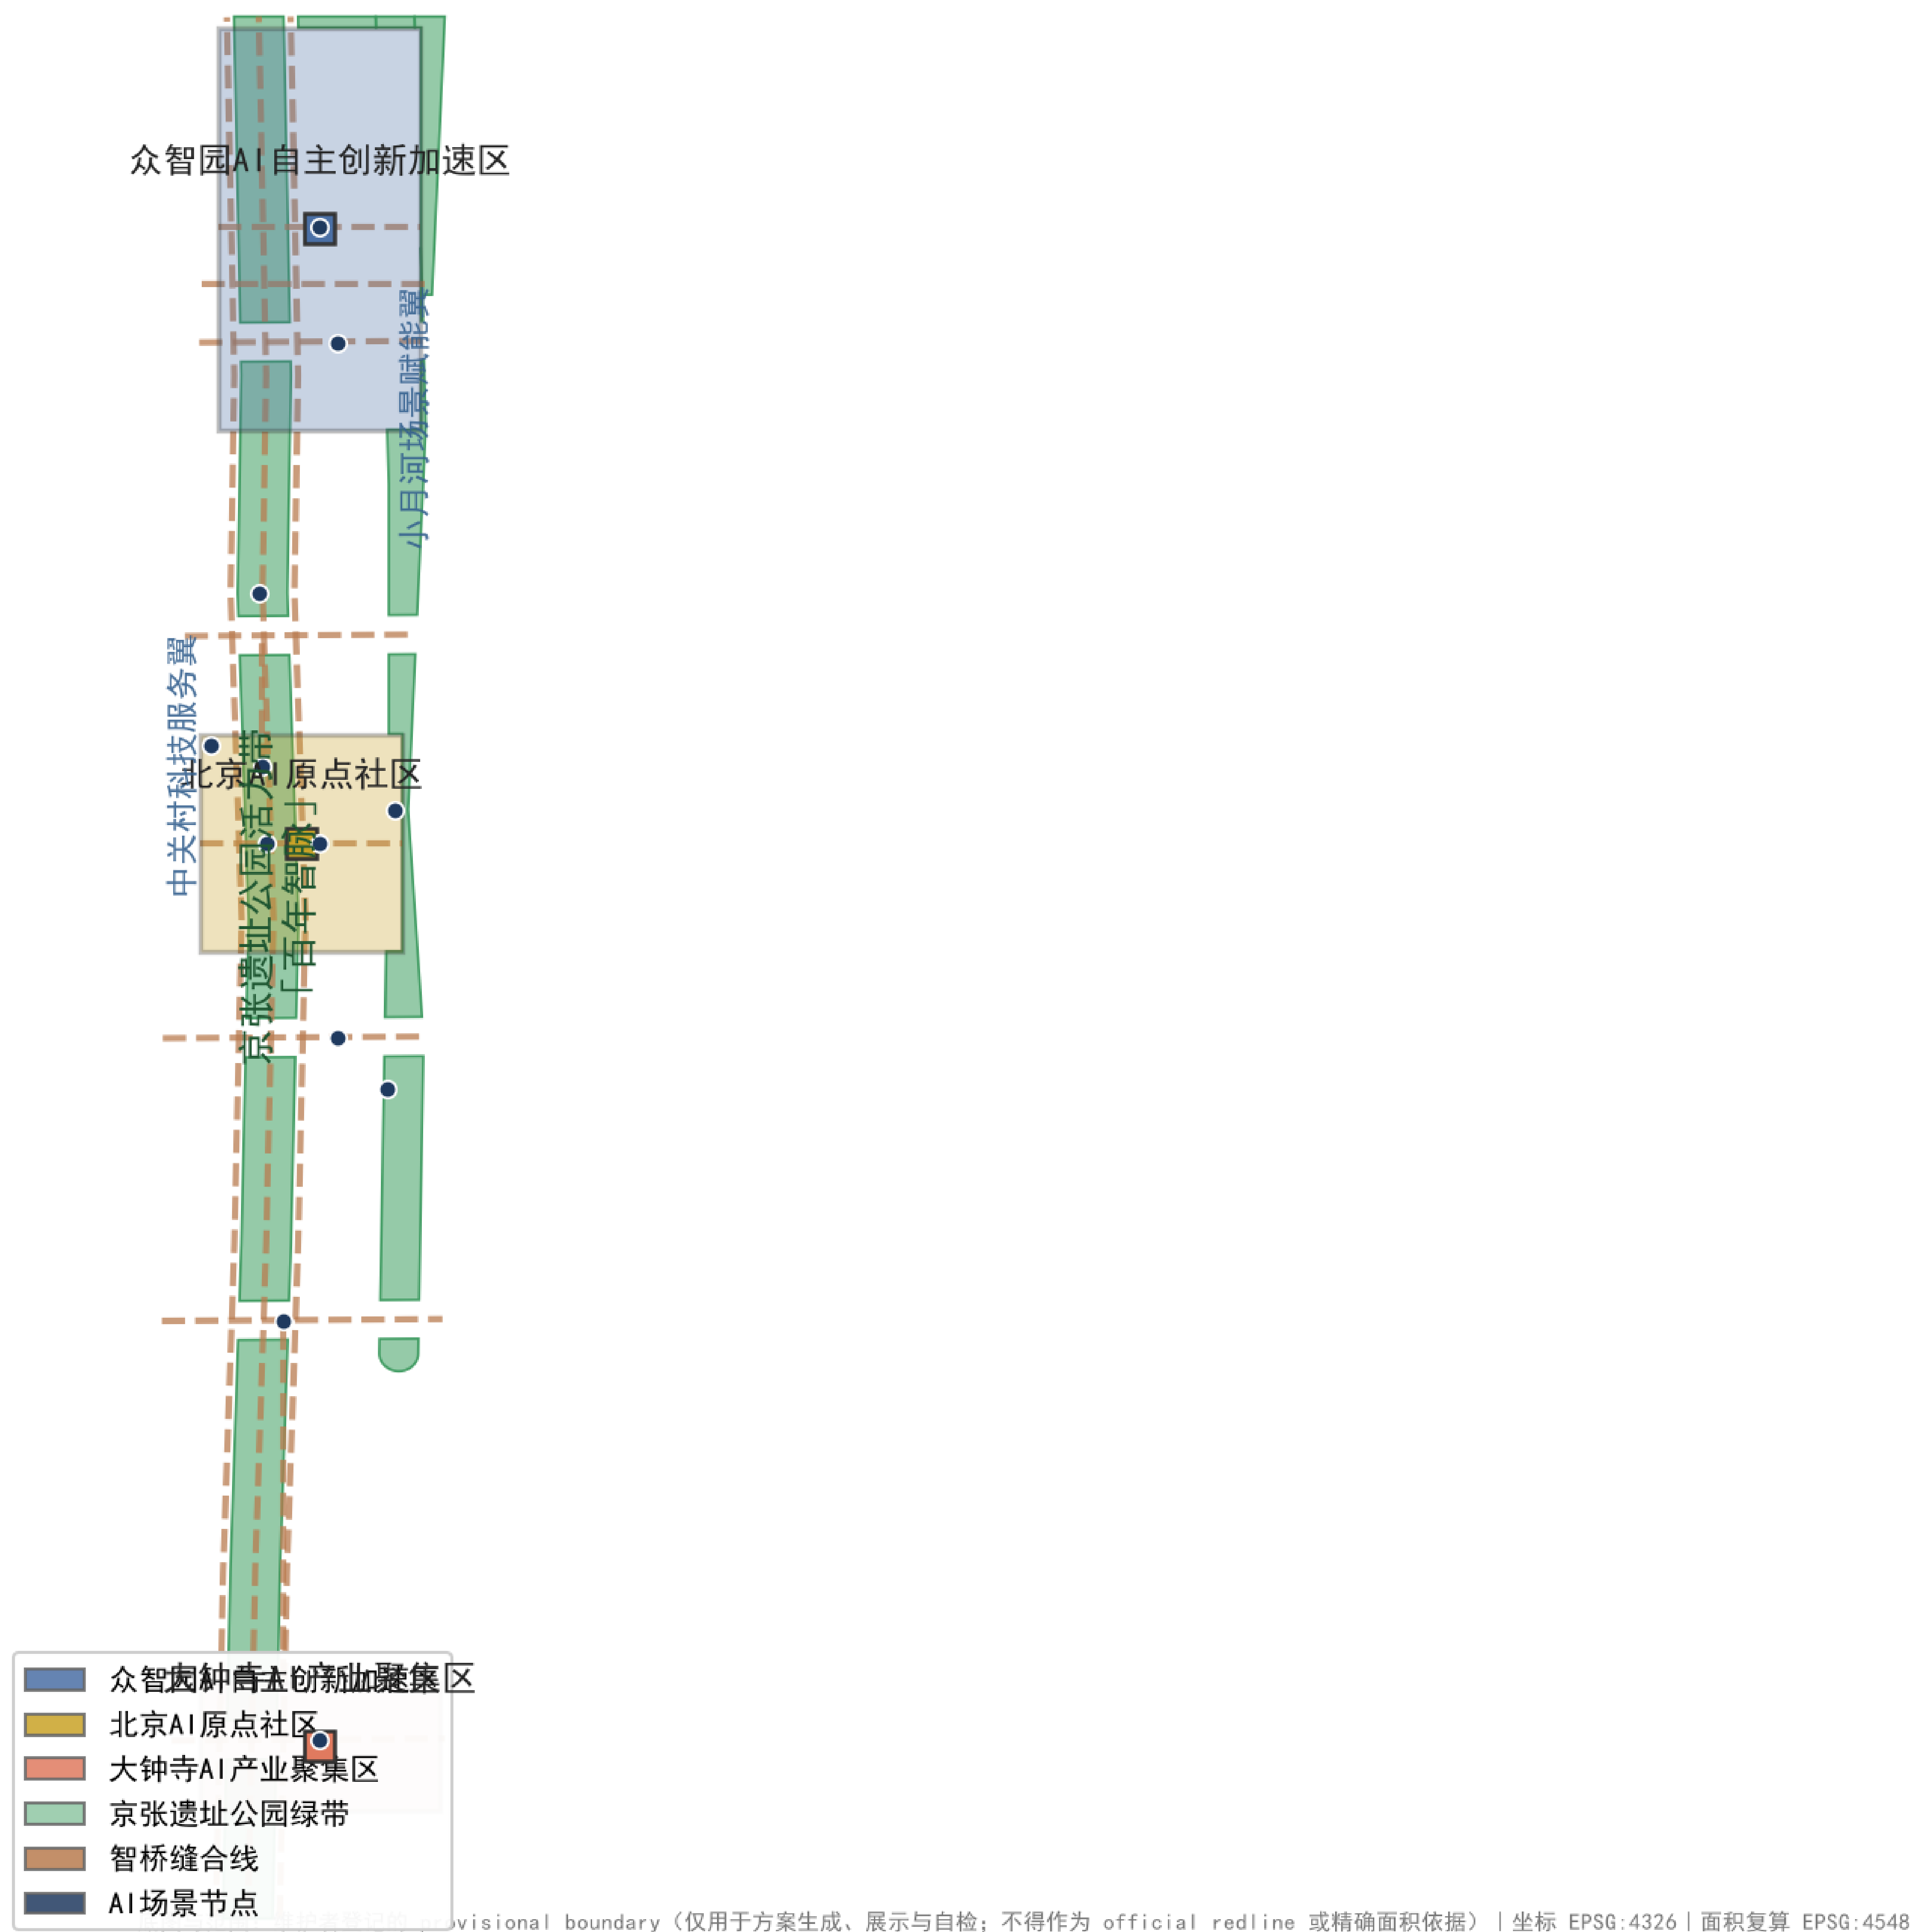

- 12 场景卡 (4 测试验证) + 12 场景节点
- 5 类用户画像与场景-空间-运营映射
- 12 个概念更新项目 + 三期分期
- 年度活动体系与长期运营机制

核心指标复算与证据链

总体设计范围 1141.3 ha geometry/site_boundary.geojson EPSG:4548 复算	绿地率 23.7% geometry/green_space.geojson 绿地并集 / 范围面积	公共空间率 10.7% geometry/public_space.geojson 公共空间并集 / 范围面积	概念建筑基底 110 栋 geometry/buildings.geojson 设计概念基底，非法定规模
AI场景节点 12 个 geometry/scenario_nodes.geojson 与12张场景卡一一对应	更新项目清单 12 项 proposal.md 概念清单，非实施承诺	重点区域 3 处 geometry/key_areas.geojson 公告 368.4 公顷 (provisional)	AI朝圣地标 3 个 proposal.md 人字碑 · 原点之环 · 鸣响之钟

证据链: GeoJSON 分区 → EPSG:4548 复算 → metrics.json → 五图 → A3/A0 → visual/index.html
自检状态: DETERMINISTIC VALIDATION / SPATIAL REVIEW / VISUAL PACKAGING / PROFESSIONAL EVIDENCE 四门本地自检
口径提示: FAR、建筑高度、建筑密度等官方控规指标缺失, 保持 status=unknown, 待正式资料补入后复算

- 三类指标: 空间复算/官方管控/运营绩效
- EPSG:4548 复算链与四门自检
- 合规矩阵 22 条 + 标准矩阵 9 条 + 深度矩阵 15 项
- 风险与待补资料清单 (risk.json / assumptions.json)