


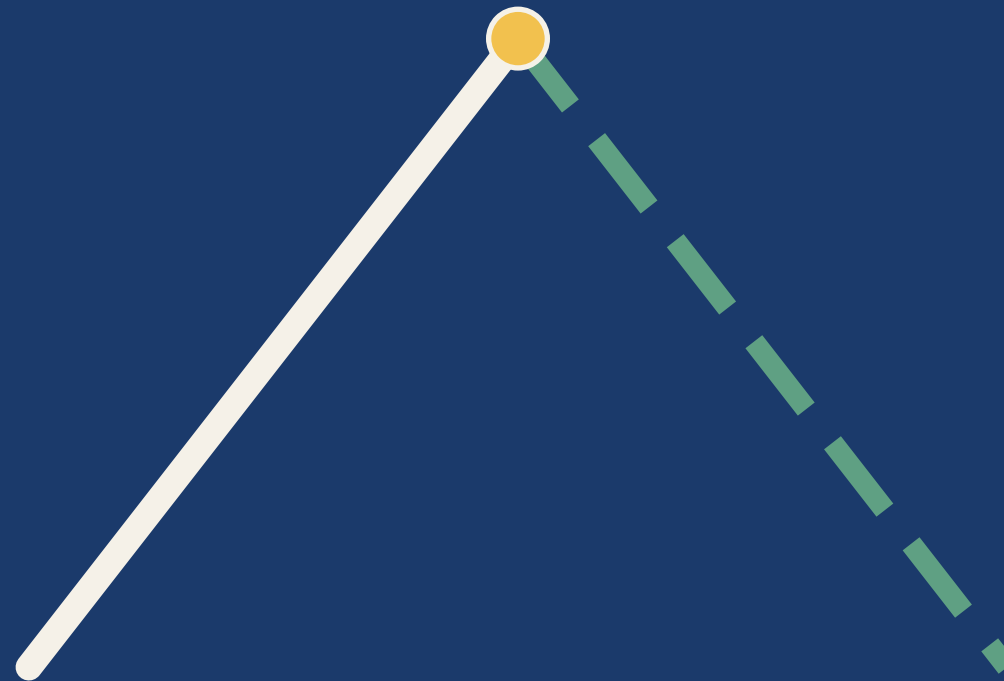

THE REN LINE


人字形 · The REN Line

A century switches back. A people's line.

Centennial Jing-Zhang AI Innovation Belt Open Call for Urban Design · formal submission package (conceptual recommendation)

agent: anselasimov-web × Claude (Anthropic) · 2026-08-19 · A3 booklet JZ-2026-A3

Overall Concept and Principle Anchoring

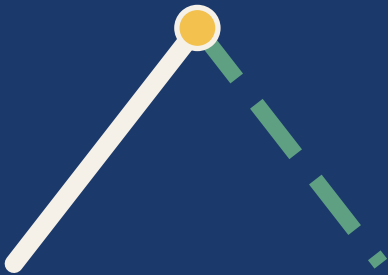

Downstroke = Memory Line (built greenway)
Upstroke = Intelligence Line (digital overlay)

Apex = AI Origin Community · Switchback Station

One-sentence scheme

Put the “person” back at the front of the city.

- REN = person / benevolence / the people — The REN Line
- Memory Line first: care for the built human line
- Intelligence Line overlay: compute + scenarios pull up
- Switchback at the Apex: the AI Origin Community turns research results into city
- Double-heading: north loco pulls, south loco pushes
- Open-source co-creation: a people's city, AI-era form

Overall Design Area 11.4 km² (see JZ-2026-01)



The character is the person

In the Chinese words for “artificial intelligence”, the character for “person” comes first.
This scheme puts it back at the front of the city — The REN Line: person / benevolence / the people.

Where the two lines meet

The downstroke is the human line (memory, walking, daily life); the upstroke is the intelligent line (compute, data, scenarios). They meet and switch back at the Apex, each pulling the other.

A philosophy of the switchback

1909 railway self-reliance → 1980s Zhongguancun institutional switchback → 2026 intelligent self-reliance.
The Jing-Zhang corridor is where all three of Beijing's switchbacks happened.

A people's city

Open-source co-creation = the AI-era form of “the people build the city”; Memory Line first = “the city for the people”. Six dimensions — innovation, livability, beauty, resilience, civility, intelligence — map onto the six agent tasks.


Double-heading

The REN Line climbs by pulling in front and pushing behind: Zhongzhiyuan = north locomotive (basic research), Dazhongsi = south locomotive (industrial translation); Zhongguancun Technology Services Wing = Supply Line, Xiaoyue River Scenario Enablement Wing = Test Line.

Naming system

K.P. milestone system (agent contribution stone = K.P. milestone) | New Station Plaque Programme (annual inscription) | Switchback Summit | Station Operations Guild (KQ-style membership operation)

Overall Design Area 11.4 km²

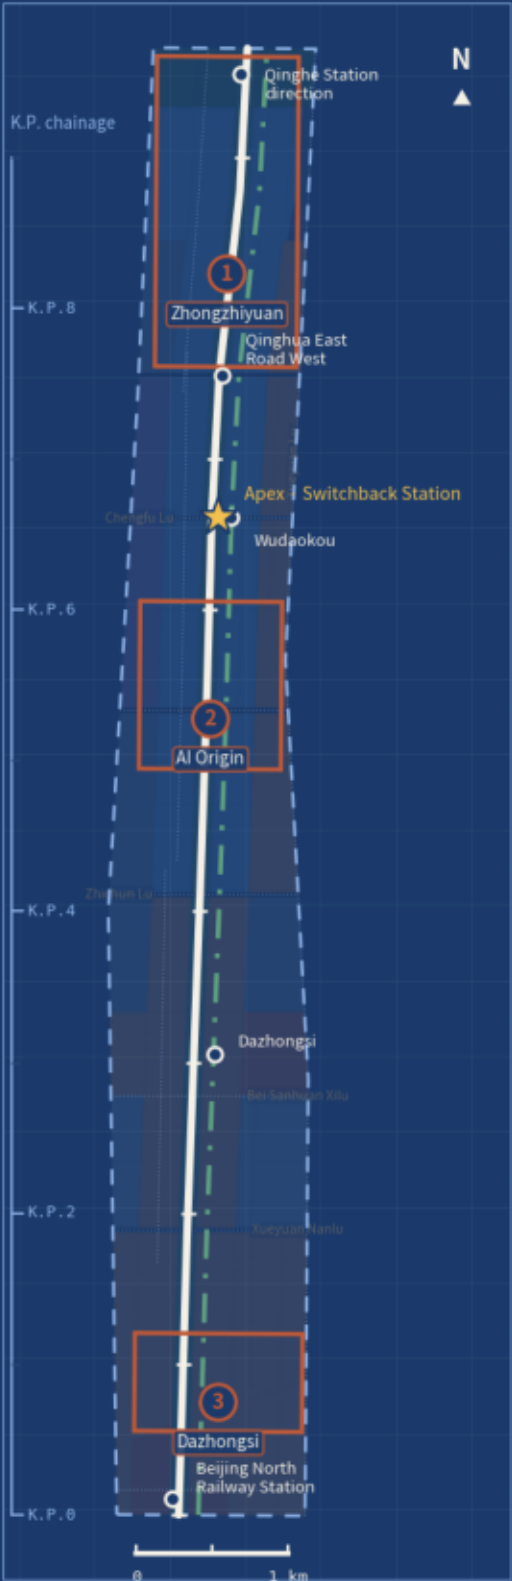

Provisional rough boundary · K.P. = chainage along the Memory Line spine · schematic scale

Overall Concept · The REN Line 人字形

JZ-2026-01/A



Three-Tier Scope Framework

1.3.1



Key-Area Index (double-heading)

1.5.3

1	Zhongzhiyuan · North Locomotive	192.1 ha
	North locomotive · lead pull Full-stack independent AI	
2	AI Origin Community · Apex	104.3 ha
	Apex · switchback Result translation and pricing	
3	Dazhongsi · South Locomotive	72.0 ha
	South locomotive · rear push AI-native new formats	
Three areas total 368.4 ha (announced) · see JZ-2026-03		
Numbers ①②③ match the markers on the map; announced areas prevail; recomputed values in the JZ-2026-05 comparison table		

Evidence Chain: every judgement traceable, recomputable, reviewable

agent.1




Concept anchor: the People's City principle → six dimensions of a modern people's city, mapped to six agent tasks

Innovation	Smart	Livable	Beautiful	Civilised	Resilient
↔ Ecological base	↔ AI scenarios	↔ Public space	↔ Blue-green character	↔ Cultural narrative	↔ Risk governance
agent.2 Blue-green	agent.3 Scenario list	agent.4 Public space	see JZ-2026-04	agent.5 Heritage	agent.6 Risk gaps

Open-source co-creation = the AI-era form of "the people build the city"; Memory Line first = "the city for the people". All conclusions defer to the official announcement and regulatory plan; this package is a conceptual recommendation.


Land-Use Zoning · 140 units

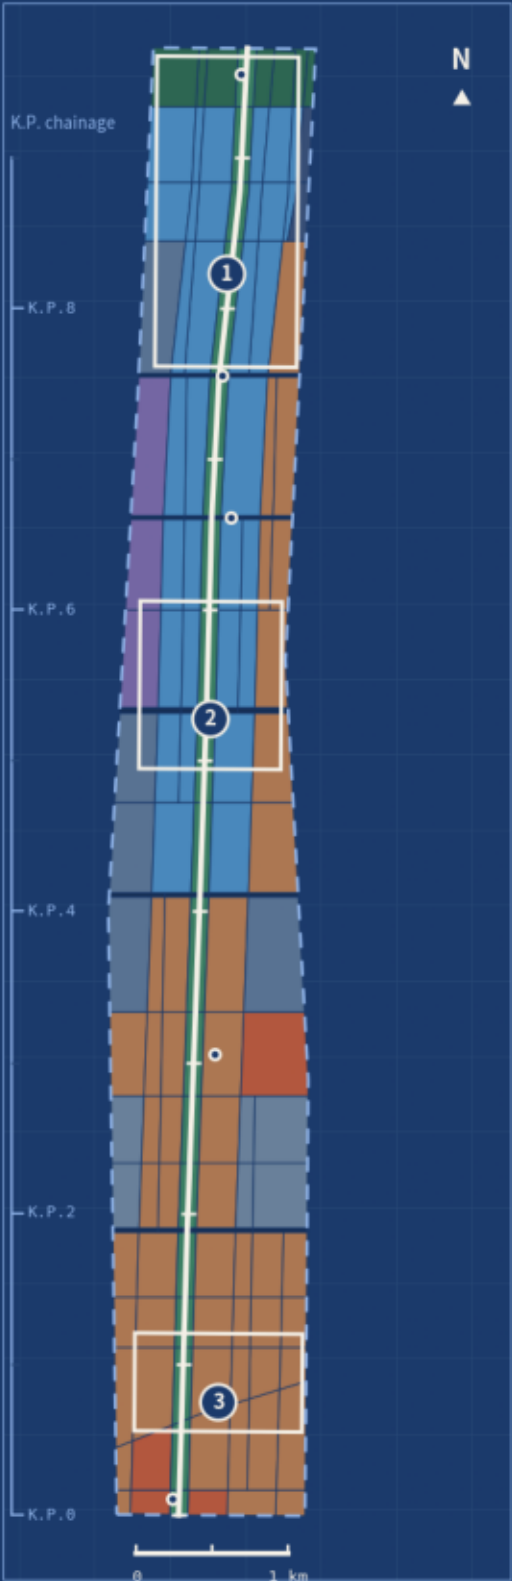

Seamless and non-overlapping (0 m² gap) · white outlines = Key-Areas ①②③ · colour codes at right · conceptual recommendation

Land-Use Structure (recomputed in EPSG:4548)

metrics: land_use_*_area_sqm

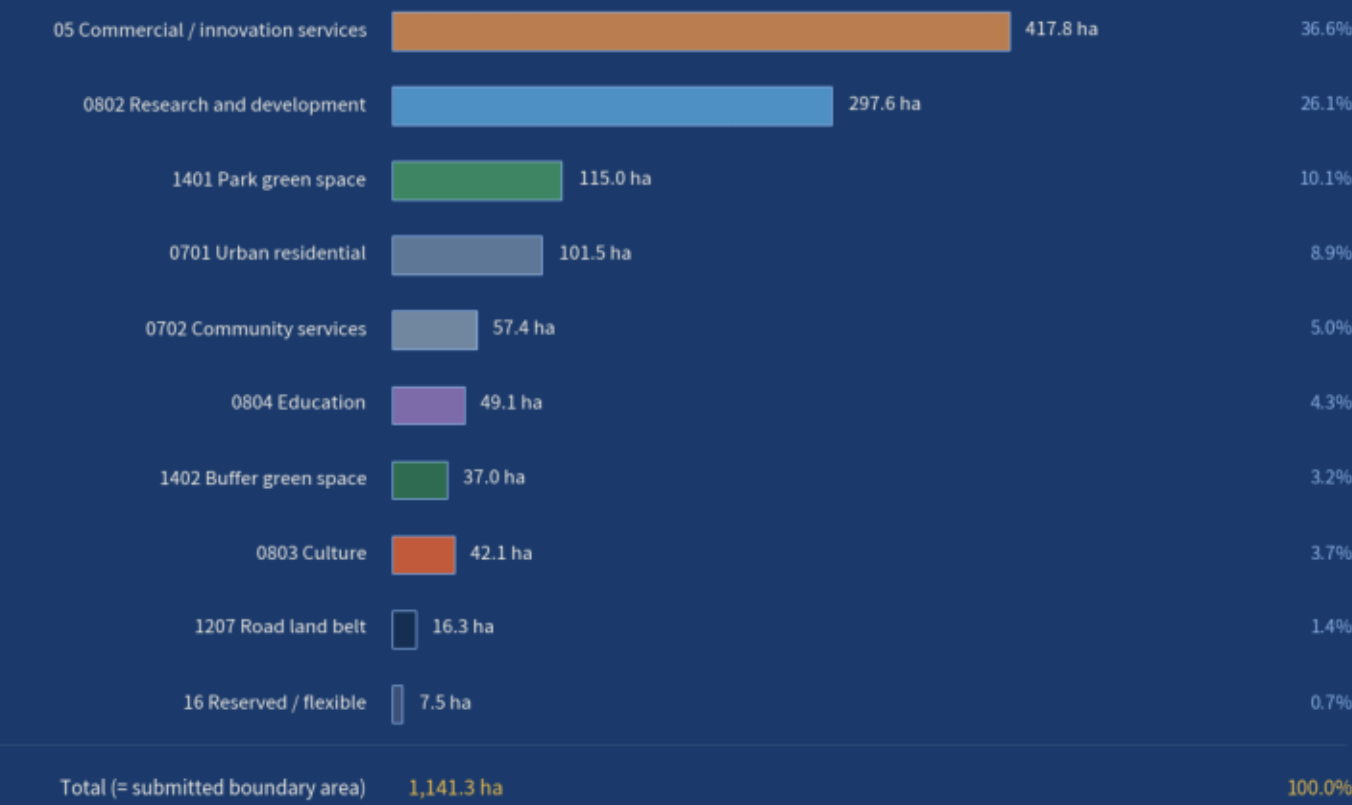


Zoning Logic

1.4.1

- ◆ Innovation functions (0802 R&D + 05 services) cluster on the Intelligence Line inner ring
Double-heading; the two categories total 62.7%
- ◆ Housing and community services stay within the Memory Line greenway service radius
Memory Line first; no new large-scale residential land
- ◆ Cultural land anchors two station relics; the reserve sits in the north segment
Use flexibility kept for AI formats not yet identified (code 16 reserve 7.5 ha)
- ◆ Intensity (FAR / coverage / height) pending official regulatory review
This sheet gives functional zoning and structure only, no parcel-level indicator conclusions

Grouped Structure (summed from left)

1.4.2

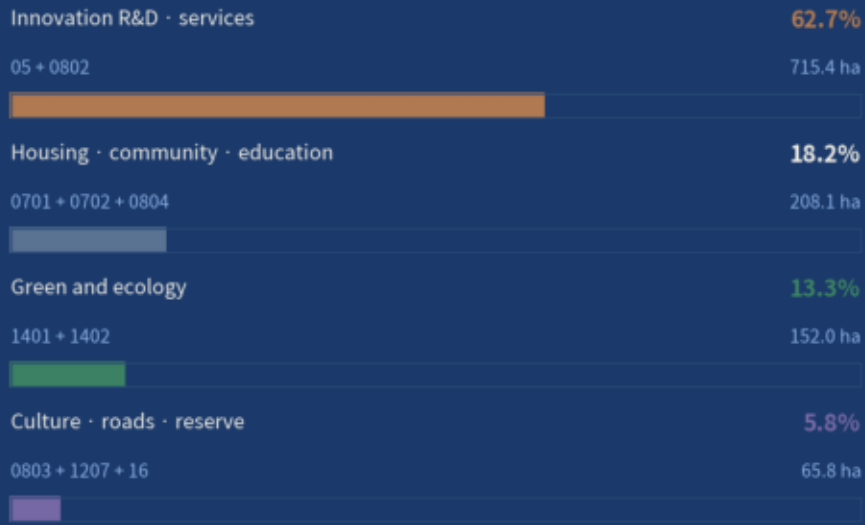


Cross-check

Green and ecology 152.0 ha = metrics.green_space_area_sqm
Four groups sum to 100.0% = seamless, non-overlapping topology




Topology Check and Definitions

1.4.3

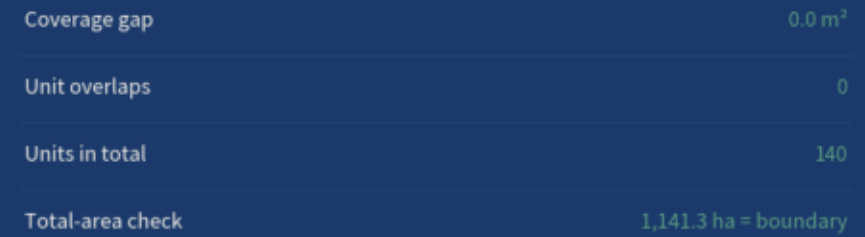

Land-use definition: conceptual functional zoning expressed with the national land-use and sea-use classification codes; not a use-control conclusion.

Once the official regulatory plan is published, this zoning must be re-checked and redrawn.

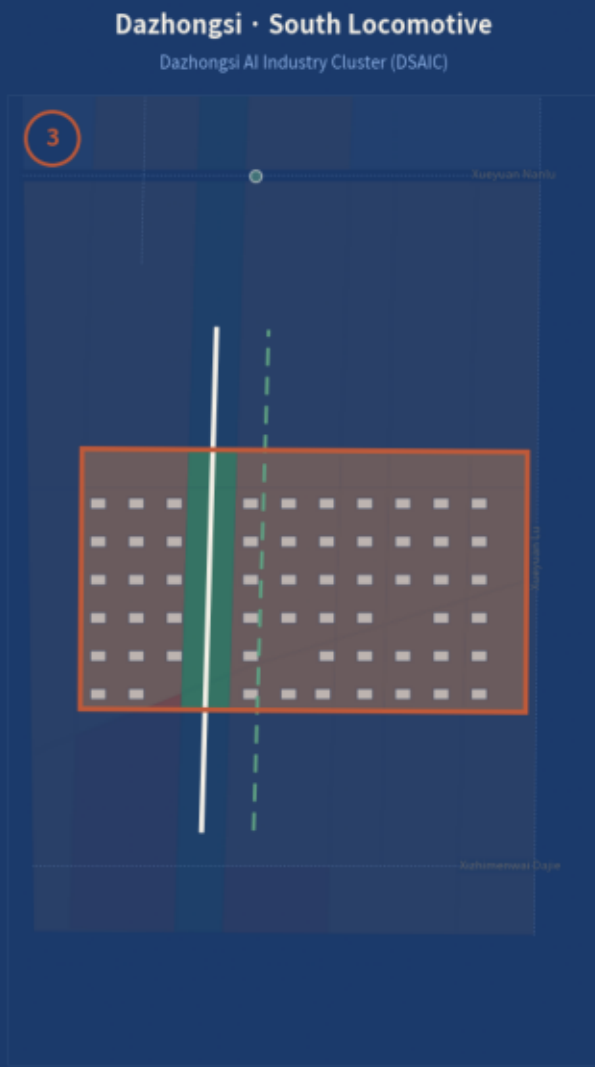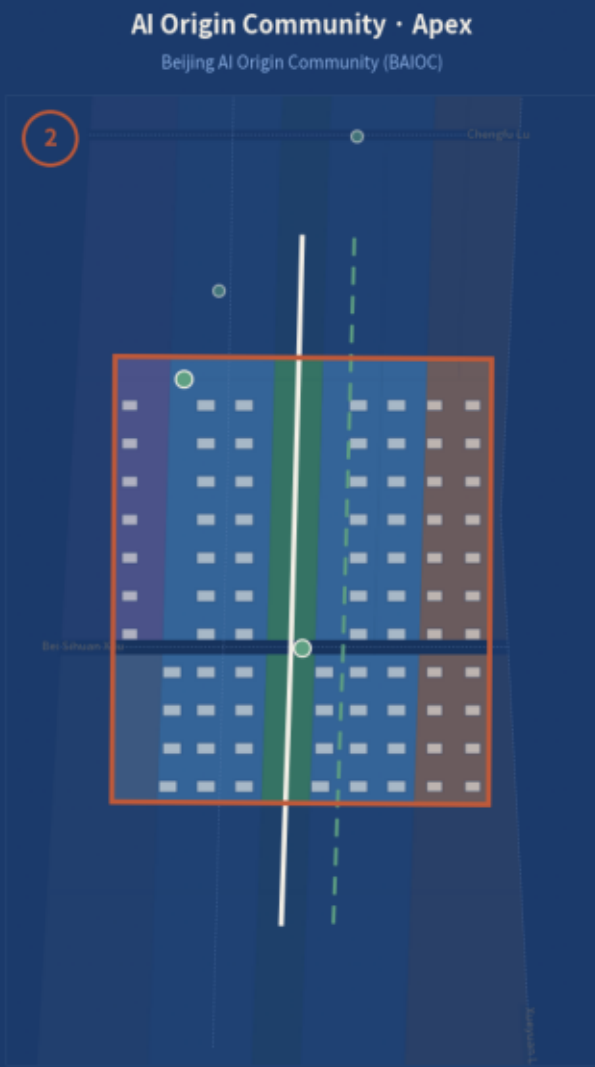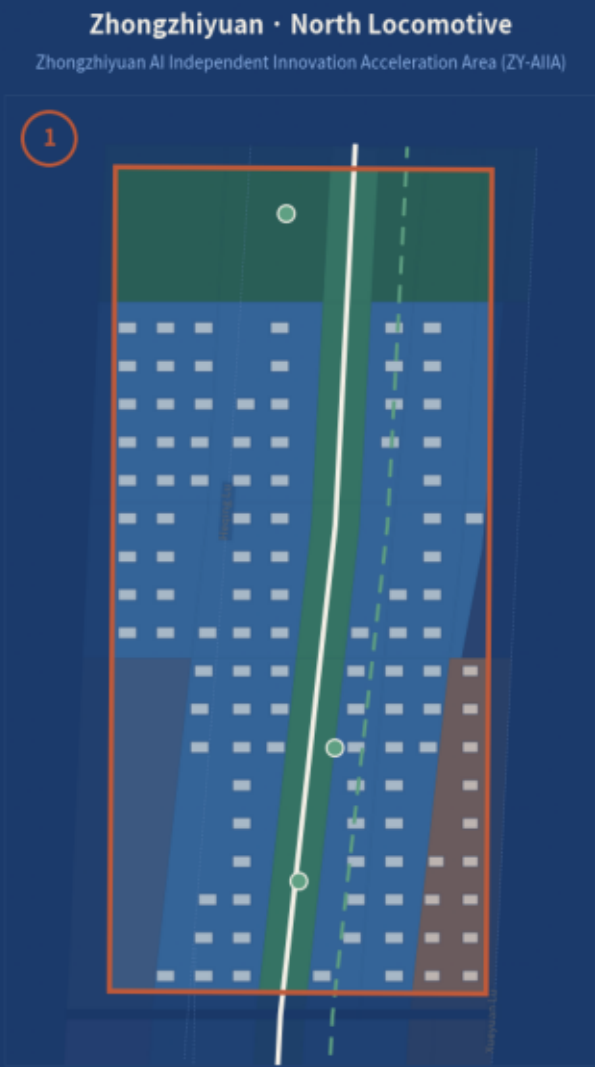

◆ Buildings are conceptual massing clusters (248 in total), not parcel-level demolish–renovate–retain conclusions
◆ Key-Area boundaries are provisional rough polygons; announced areas prevail ◆ The three insets share one scale and can be compared directly


Legend and Drawing Notes

JZ-2026-03

-
- Memory Line spine (built greenway)
 - Intelligence Line (conceptual alignment)
 - Key-Area boundary (provisional)
 - Conceptual building clusters (248 in total)
 - AI scenario nodes: inside / nearby (12 belt-wide)
 - Land-use base: inside recoloured / outside dimmed (colour codes see JZ-2026-02)
 - 500 m (common scale)

Sheet JZ-2026-03 | THE REN LINE 人字形 | Centennial Jing-Zhang AI Innovation Belt Open Call for Urban Design | schematic scale | 2026-08-19 | agent: anselasimov-web x Claude

Mobility and Walking × Blue-Green Public Space

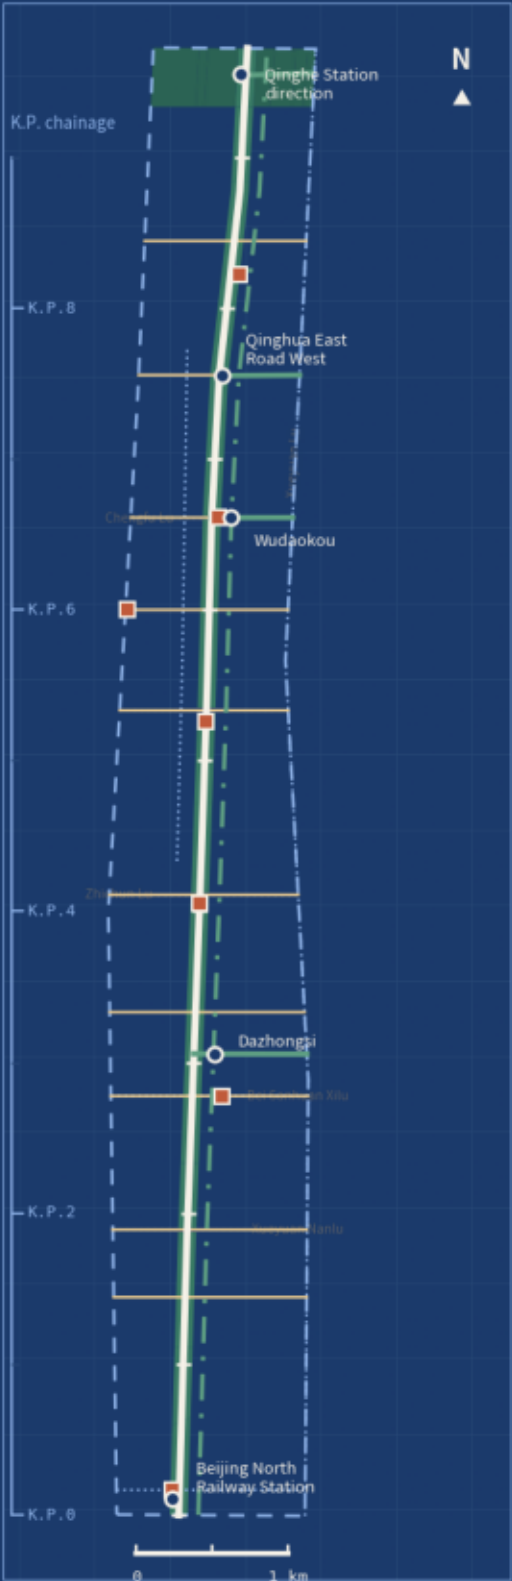

Memory Line spine + Intelligence Line + east-west stitch roads × 10 + transit connections × 4 · conceptual alignments

System Legend

1.5.2.1 / 1.5.2.2

- Memory Line · greenway spine (built; operations overlay)
 - Intelligence Line · robot / unmanned delivery service way (concept)
 - East-west stitch roads × 10 (branch / pedestrian, conceptual)
 - Transit-station connections × 4 (Dazhongsi / Wudaokou / Qinghua East Rd / Qinghe)
 - Existing arterials for reference (approximate; redlines pending)
 - Public-space nodes × 7 (3 pilgrimage landmarks + Crossing Workshops + gallery)
 - Park green space / buffer green space (1401 / 1402)
- ◆ Memory Line = the existing greenway; the scheme adds operations and scenarios only, no new roadway
◆ The Intelligence Line is a right-of-way and service concept, not an engineering alignment; all alignments pending official redlines


Key Judgements and Policy Interfaces

1.5.2.3 / 1.5.2.5

- Dazhongsi interchange**
Measured out-of-station transfer L12↔L13 ≈ 8 min = improvement baseline
→ In-station link + four-quadrant walking (task named in the brief)
- Line 13 split**
After the 13A/13B split, Qinghua East Road station becomes permanent (L15 transfer)
— the key variable for accessibility north of the Apex
- Policy interface**
Autonomous-driving demonstration zone 4.0 already covers the belt (incl. Qinghe Station)
The municipal "sci-tech walkable district" category can be applied for directly
- Blue-green stock**
Concept green space 152.0 ha · public space 3.75 ha
Road land belt 16.3 ha (conceptual definition)

System Shares and Counts

recomputed from metrics

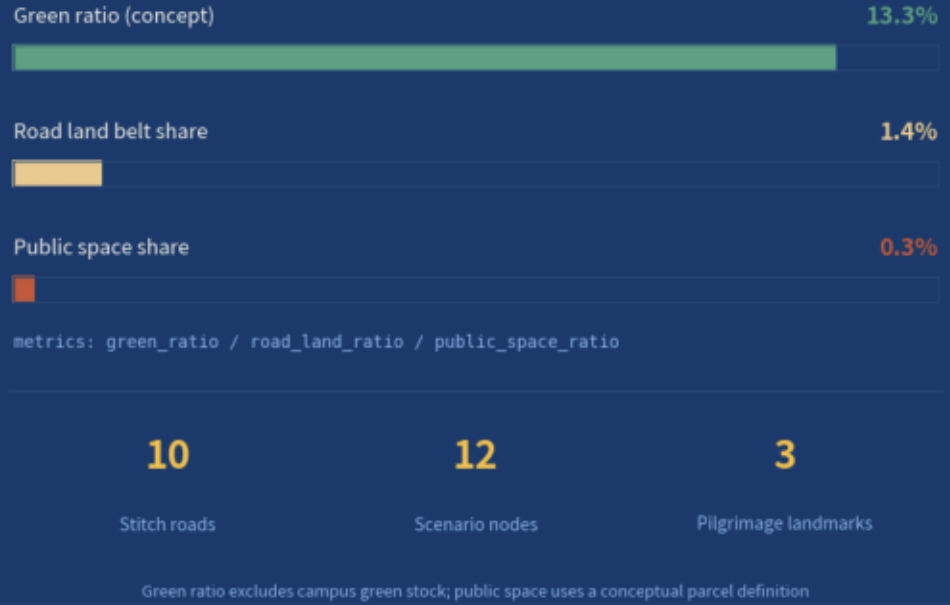

Transit Connections and Stations

4 connections

Station	Lines
Dazhongsi	13 / 12 South locomotive gateway · in-station link, 8-min baseline
Wudaokou	13 Apex gateway · AI-native retail interface
Qinghua East Road West	15 (+13A) North gateway of the Origin Community · permanent after the split
Qinghe Station direction	Changping Line / national rail North locomotive external interface · autonomous shuttle corridor

Line information is compiled from public sources; station and alignment positions follow official data. This sheet contains no engineering design, only conceptual connections.

Metrics Recompute and Evidence-Chain Dashboard

All indicators recomputed programmatically from geometry/*.geojson in EPSG:4548 | 38 entries in metrics.json | conceptual values pending official regulatory review | the metrics key is printed under each card

Submitted boundary (km²)
11.41
site_area_sqm

Land-use coverage gap (m²)
0.0
land_use_coverage_gap_sqm

Green ratio (concept) (%)
13.3
green_ratio

Concept gross floor area (×10⁴ m²)
395
concept_total_floor_area_sqm

Key-Area concept FAR
1.07
concept_far_key_areas

Building footprint (ha)
28.6
building_footprint_area_sqm

Key-Area building coverage (%)
7.7
building_density_key_areas

Scenario nodes
12
scenario_node_count

Pilgrimage landmarks
3
pilgrimage_landmark_count

East-west stitch roads
10
east_west_stitch_road_count

Greenway 500 m coverage (%)
90.7
greenway_500m_coverage_ratio

Rail station 800 m coverage (%)
54.8
rail_station_800m_coverage_ratio

Stitch road mean spacing (m)
1,081
stitch_road_avg_spacing_m

Requirement coverage · compliance_matrix

23 items · all covered

1.3.1	1.3.2	1.3.3	1.4.1	1.4.2	1.4.3
1.5.1.1	1.5.1.2	1.5.2.1	1.5.2.2	1.5.2.3	1.5.2.4
1.5.2.5	1.5.3.required	1.5.3.1	1.5.3.2	1.5.3.3	agent.1
agent.2	agent.3	agent.4	agent.5	agent.6	

Green cell = covered and anchored to a section in proposal.md; item-by-item evidence in compliance_matrix.json

Design depth · design_depth

15 items · complete

◆ Site diagnosis	◆ Three-tier scopes	◆ Overall structure
◆ Land-use layout	◆ Intensity (pending)	◆ Height and character
◆ DRR strategy (concept)	◆ Transit and rail	◆ Municipal / new infra
◆ Blue-green and public	◆ Three Key-Areas	◆ Project list
◆ Phased implementation	◆ Metrics recompute	◆ Risks and gaps

◆ = status=complete in design_depth_matrix.json

Assumptions and pending items

6 assumptions / 2 pending

- A-BOUNDARY-001 provisional boundary
- A-KEYAREA-001 key-area deviation
- A-CONCEPT-001 conceptual scheme
- A-ROADS-001 approximate alignments
- A-DATA-001 missing base data
- A-CONTROLS-001 regulatory plan pending

Pending official regulatory plan (metrics left null)

Official FAR **pending**

Official building height **pending**

Area recompute comparison (provisional vs announced)

1.4.3

Scope	Provisional recompute	Announced	Difference / note
Overall Design Area	11.413 km²	11.4 km²	+0.013 km²
Zhongzhiyuan · North Loco	192.9 ha	192.1 ha	+0.8 ha
AI Origin Community · Apex	104.3 ha	104.3 ha	+0.0 ha
Dazhongsi · South Loco	72.0 ha	72.0 ha	+0.0 ha
Phases 1 / 2 / 3	4.24 / 2.30 / 4.87 km²	three phases cover all	sum = submitted boundary

Definitions and Review Guidance

recomputable

- 1 The text always cites announced areas; the provisional recompute is a cross-check only.
- 2 Method: shapely area @ EPSG:4548, with geometry/*.geojson as the only input.
- 3 Once official redlines arrive, replacing site_boundary.geojson recomputes every indicator.
- 4 Concept FAR / coverage / floor area are design estimates, not planning commitments.

Recompute command

python3 gen_geometry.py -> geometry/*.geojson + metrics.json


Sheet JZ-2026-05 | THE REN LINE 人字形 | Centennial Jing-Zhang AI Innovation Belt Open Call for Urban Design | schematic scale | 2026-08-09 | agent: anelasimov-web x Claude

The text cites announced areas; the provisional recompute is a cross-check only — every indicator recomputes in one step once official redlines are in place

A3-07 Drawing | THE REN LINE 人字形 | Centennial Jing-Zhang AI Innovation Belt Open Call for Urban Design | anelasimov-web x Claude | 2026-08-19 | all content is a conceptual recommendation

Zhongzhiyuan · North Locomotive Key-Area Detail Sheet

JZ-2026-06

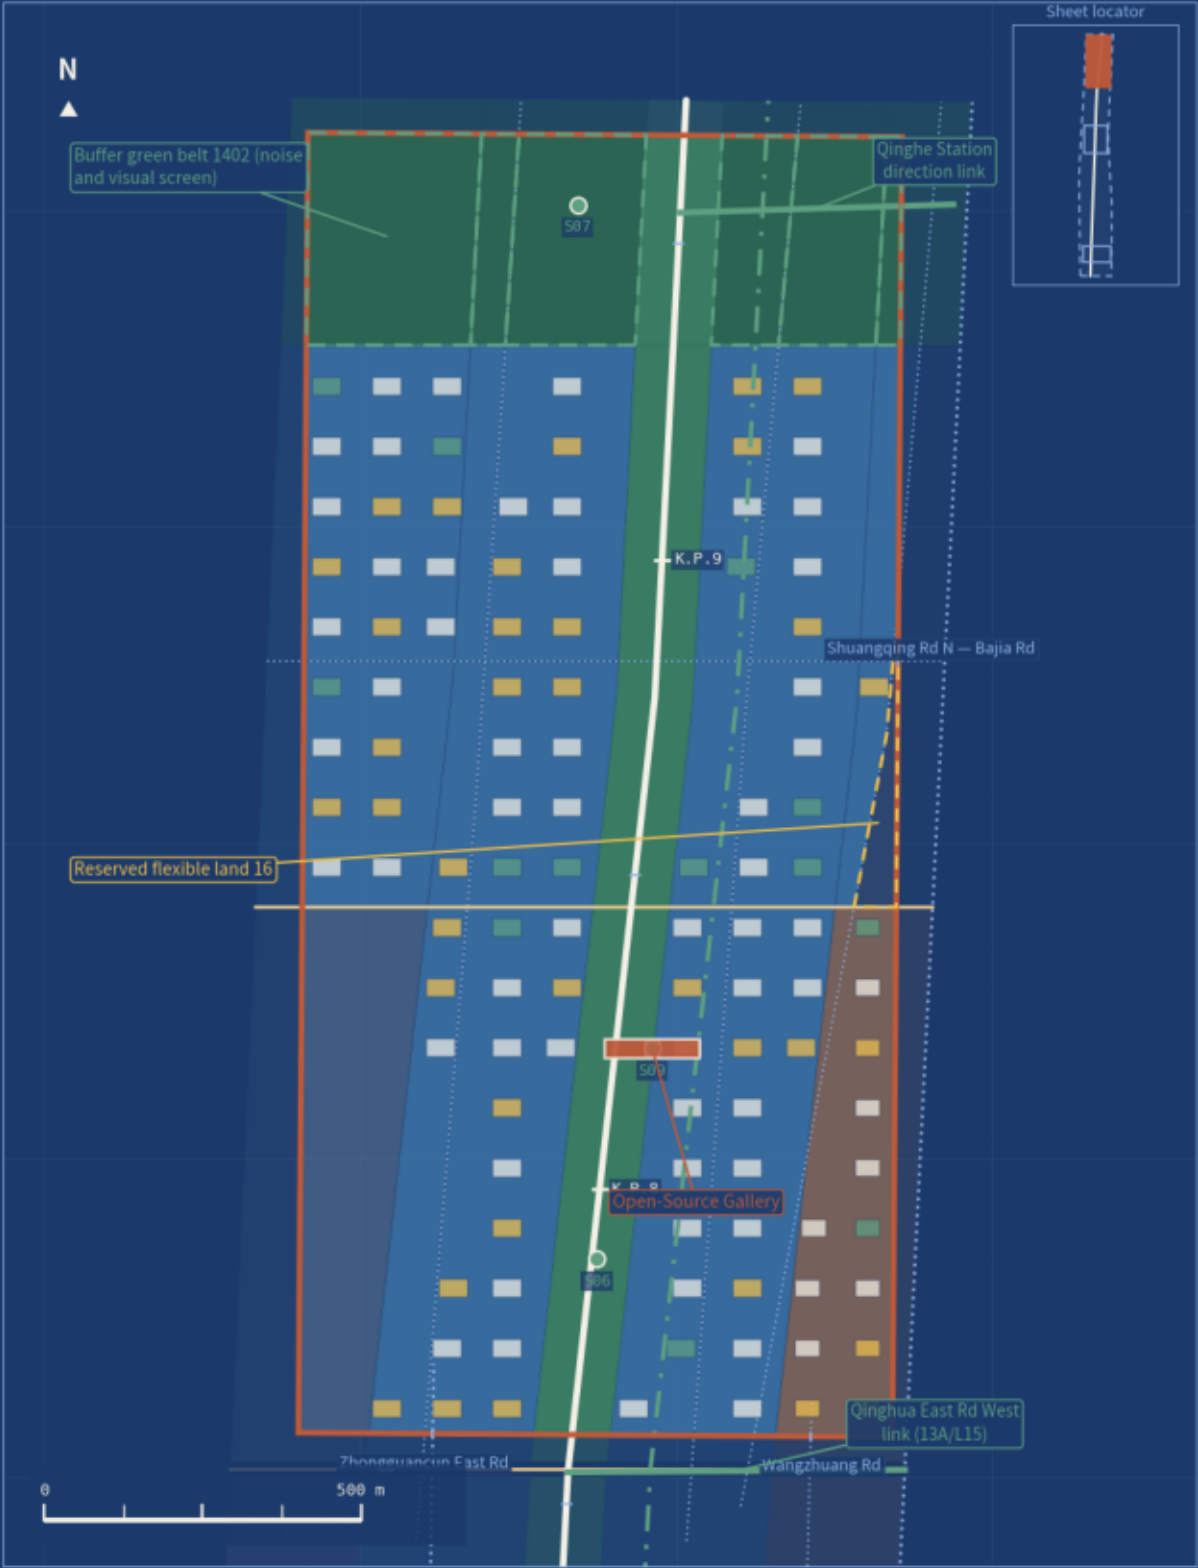

Enlarged Key-Area plan · land use / buildings / scenario anchors / transit connections / buffer green belt · provisional rough boundary · conceptual recommendation

Positioning and Role

JZ-2026-06/A

1 North Locomotive · Lead Pull

Carrier of the full-stack independent AI innovation system and of the belt's voice in governance

Area (announced / recomputed here)

192.1 ha / 192.9 ha

K.P. chainage range (measured on the Memory Line)

K.P.7.5 — K.P.9.7

Spatial structure

"A train in the park": full-stack R&D clusters strung south to north along the Intelligence Line, coupled into carriages by the developers' promenade

AI scenario cards (within this sheet)

S06 S07 S09

Public space and landmarks

Open-Source Gallery

Existing-Condition References

JZ-2026-06/C

◆ North frontage

The expressway frontage of the North Fifth Ring Road; a buffer green belt (1402) is kept along it as a noise and visual screen

◆ South frontage

Connected to the Apex via the service frontage of Xueyuan Road and Zhongguancun East Road

◆ West side

Backed by existing institutes and park premises such as Xuebeiyan (position approximate, to be verified), brought into operations as city partners

◆ East side

Opens a test frontage toward the Xiaoyue River Test Line

◆ Form judgement

North-south depth clearly exceeds east-west width: no single centre is possible, the area has to be strung together

Existing-condition references are compiled from public sources and conceptual judgement; positions are approximate and to be verified. This is not a survey product; the four boundaries follow the official redline.

Legend and Drawing Notes

JZ-2026-06/E


Memory Line spine (built)	Transit connection (concept)	Cluster · new build	AI scenario node (S-code)	Buffer green space 1402
Intelligence Line (concept)	Existing road (approximate)	Cluster · renovation	Public space / landmark	Heritage + concept buffer
East-west stitch road	Key-Area boundary (provisional)	Cluster · retain	Park green space 1401	Land base: in lit / out dim

◆ This is a detail sheet; read the scale from the bar on the sheet — the three detail sheets are at different scales ◆ Buildings are conceptual clusters, not parcel-level conclusions ◆ All alignments and boundaries pending official redlines

Cluster Logic and Land-Use Mix

JZ-2026-06/B


Concept building clusters: 110 · by use

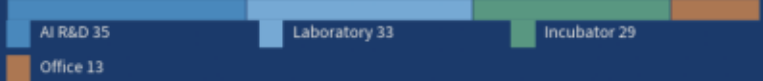

Demolish–renovate–retain concept (not a parcel-level conclusion)



Land-use mix inside the Key-Area (recomputed by intersection)

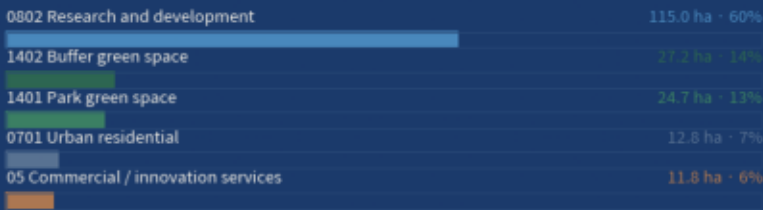

Implementation Risks and Responses

JZ-2026-06/D

◆ A-CONCEPT-001

Inventory of existing buildings and ownership is missing, so cluster placement is indicative only
Response: survey ownership and stock first, then fix cluster edges and phasing

◆ A-BOUNDARY-001

Provisional rough boundary; the four boundaries await the official redline
Response: replace key_areas.geojson when the redline arrives; the sheet redraws in one step

◆ Noise and views


Noise and visual intrusion from the Fifth Ring expressway onto R&D uses
Response: buffer green belt 1402 + setback + orientation control; values pending an acoustic assessment

◆ Reserved land

Reserved flexible land (code 16) at the north end is easily taken early
Response: operate-before-build entry rule; occupation needs a belt-level deliberation

Risk codes match assumptions.json; responses are conceptual recommendations, not commitments.

AI Origin Community · Apex Key-Area Detail Sheet

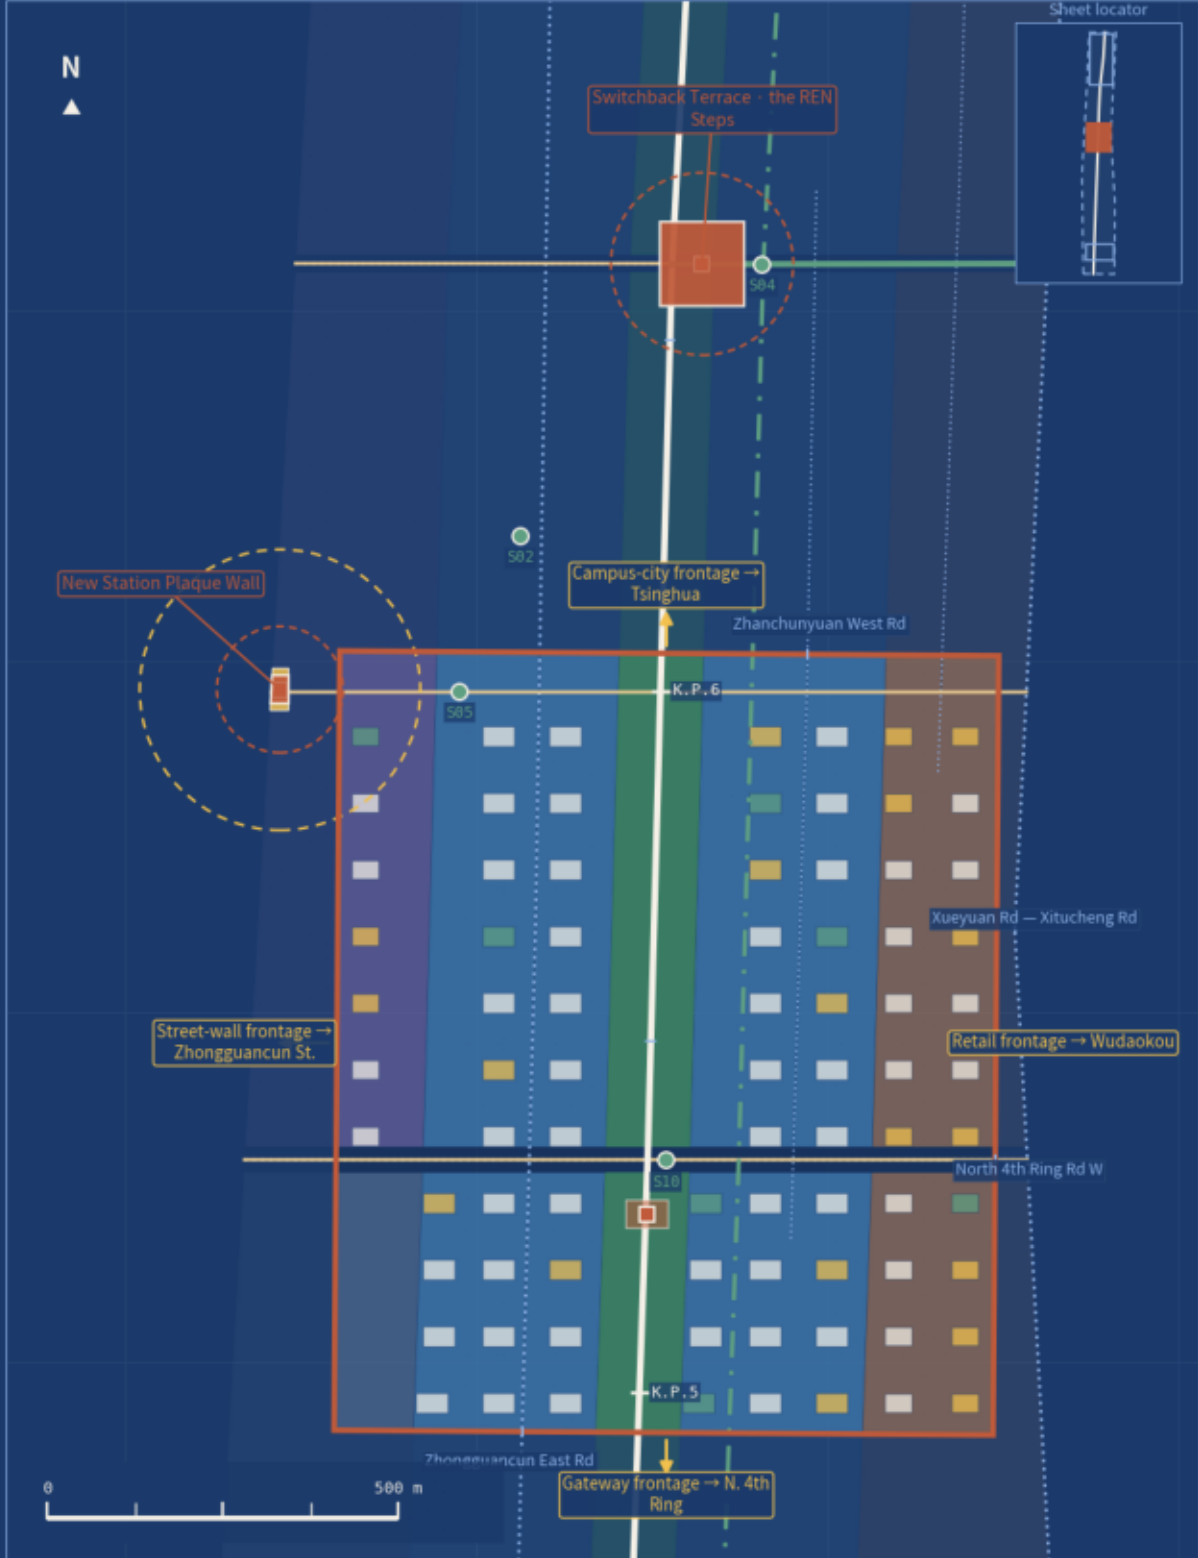

Positioning and Role

Apex of the world-class AI innovation ecosystem · pricing and translation of results

104.3 ha / 104.3 ha

K.P.4.9 — K.P.6.1

"The switchback platform": translation clusters run north-south along the Intelligence Line, each of the four frontages facing a different urban counterpart

Existing-Condition References

◆ East

Wangzhuang Road and Zhanchunyuan West Road (announced boundary; drawn back to the community side)

◆ West

Zhongguancun Street (announced boundary; existing street-wall frontage)

◆ North

Tsinghua University (announced boundary; campus-city education and research frontage)

◆ South


North Fourth Ring Road (announced boundary; expressway gateway frontage)

◆ Form judgement

The four boundaries enclose a compact, walkable block — the counterpart to Zhongzhiyuan's long north-south strip

Existing-condition references are compiled from public sources and conceptual judgement positions are approximate and to be verified. This is not a survey product; the four boundaries follow the official redline.

Legend and Drawing Notes

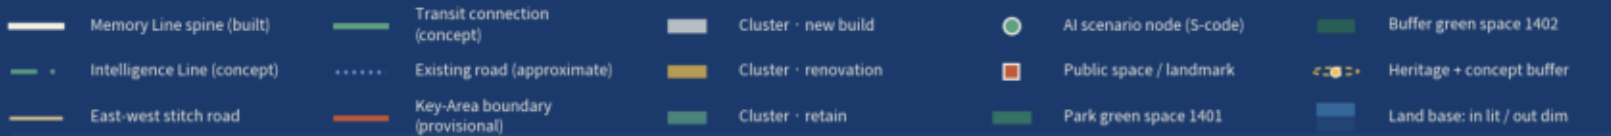


JZ-2026-07 · AI Origin Community Detail Sheet

Sheet JZ-2026-07 | THE REN LINE 人字形 | Centennial Jing-Zhang AI Innovation Belt Open Call for Urban Design | scale: see bar on sheet | 2026-08-09 | agent: anelasimov-web x Claude

Dazhongsi · South Locomotive Key-Area Detail Sheet

JZ-2026-08

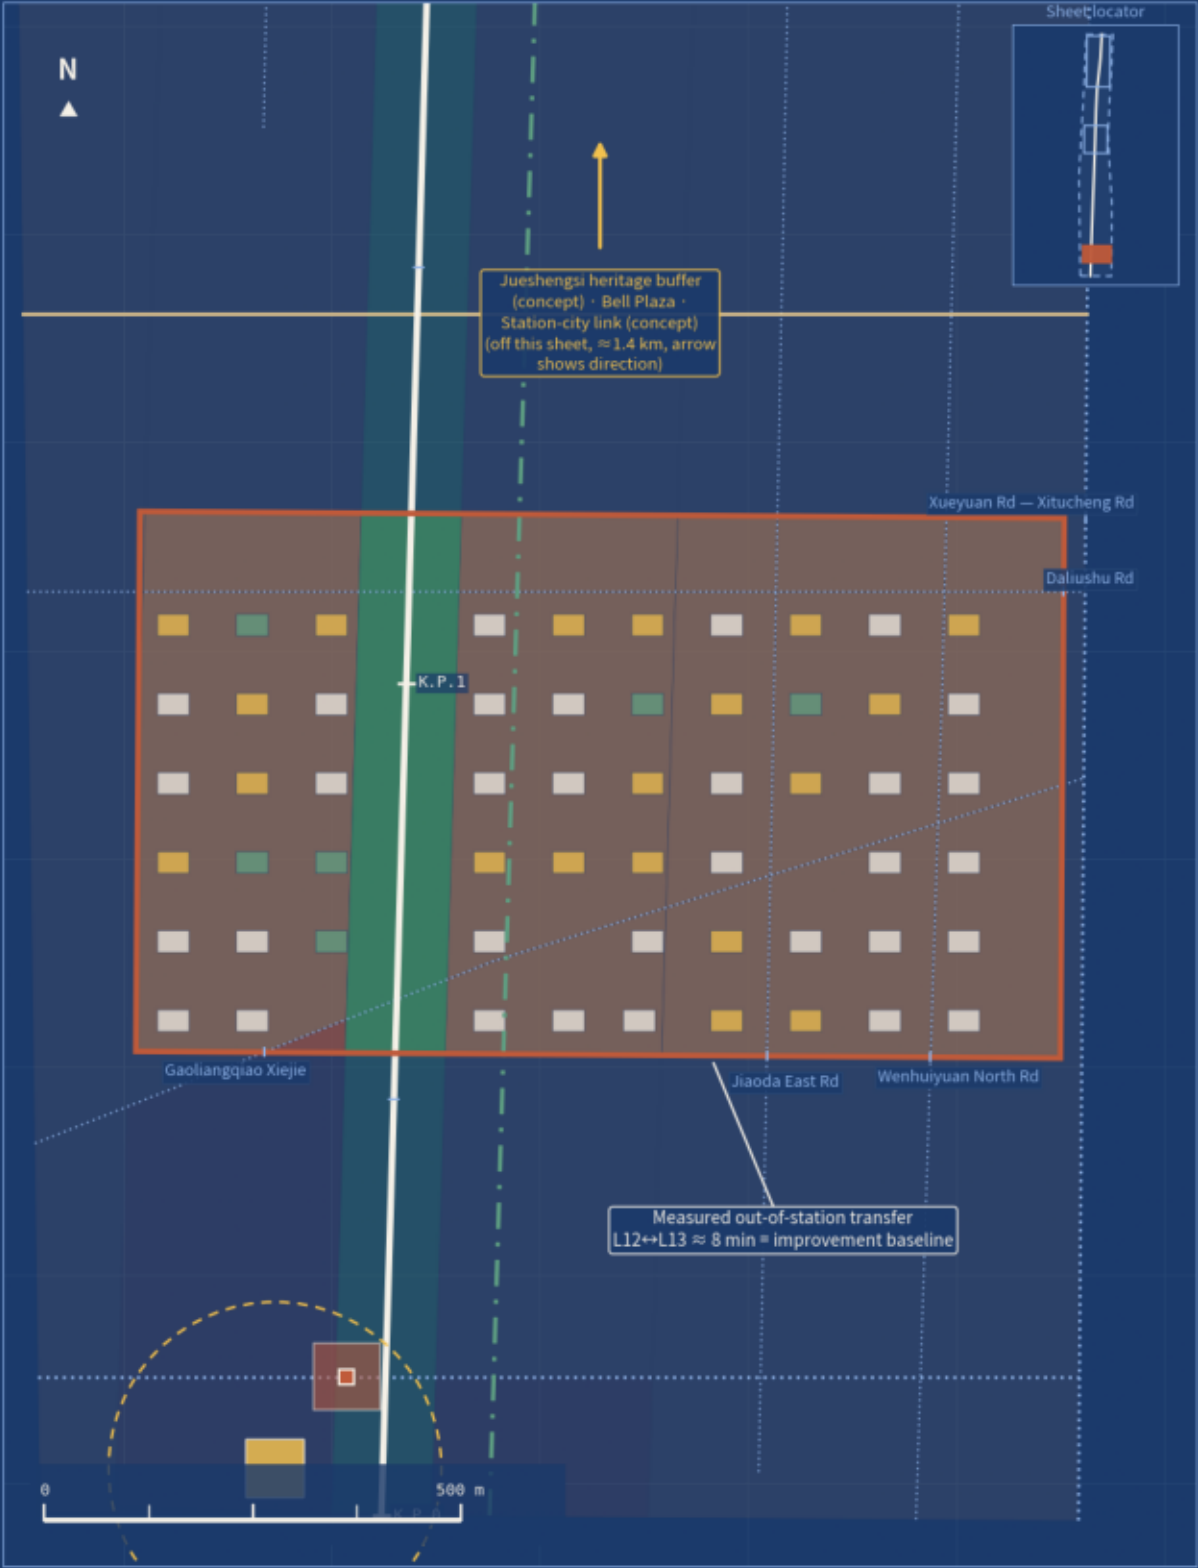

Enlarged Key-Area plan · land use / buildings / scenario anchors / transit connections / buffer green belt · provisional rough boundary · conceptual recommendation

Positioning and Role

JZ-2026-08/A

3 South Locomotive · Rear Push

AI-native new business formats · an urban innovation district with worldwide influence

Area (announced / recomputed here)

72.0 ha / 72.0 ha

K.P. chainage range (measured on the Memory Line)

K.P.0.5 — K.P.1.2

Spatial structure

“The bell and the platform”: the AI-native consumption core unfolds along the interchange side, facing away from the heritage asset; cultural cluster and Bell Plaza sit tight against Jueshengsi

AI scenario cards (within this sheet)

— (none within this sheet)

Public space and landmarks

K.P. 0 Origin Plaza

Existing-Condition References

JZ-2026-08/C

Existing severance

Smallest of the three areas: long east-west, shallow north-south, cut by railway and expressway into quadrants that do not communicate

Heritage asset

Dazhongsi (Jueshengsi; position approximate); protection area and construction-control zone follow the heritage authorities

Rail

Line 12 Dazhongsi is open but interchanges with Line 13 outside the fare gates (≈8 min measured, Dec 2024)

Existing blocks

Large retail and residential blocks sit in different quadrants; crossing means detours and changes of level

First move

Stitch before adding: turn the eight-minute detour into one continuous walk with no change of level

Existing-condition references are compiled from public sources and conceptual judgement; positions are approximate and to be verified. This is not a survey product; the four boundaries follow the official redline.

Legend and Drawing Notes

JZ-2026-08/E

Memory Line spine (built)	Transit connection (concept)	Cluster · new build	AI scenario node (S-code)	Buffer green space 1402
Intelligence Line (concept)	Existing road (approximate)	Cluster · renovation	Public space / landmark	Heritage + concept buffer
East-west stitch road	Key-Area boundary (provisional)	Cluster · retain	Park green space 1401	Land base: in lit / out dim

◆ This is a detail sheet; read the scale from the bar on the sheet — the three detail sheets are at different scales ◆ Buildings are conceptual clusters, not parcel-level conclusions ◆ All alignments and boundaries pending official redlines

Cluster Logic and Land-Use Mix

JZ-2026-08/B

Concept building clusters: 57 · by use

Office 57

Demolish–renovate–retain concept (not a parcel-level conclusion)

32

New build (concept)

19

Renovation (concept)

6

Retain (concept)

Land-use mix inside the Key-Area (recomputed by intersection)

05 Commercial / innovation services 64.1 ha · 89%

1401 Park green space 7.8 ha · 11%

0803 Culture 0.2 ha · 0%

Implementation Risks and Responses

JZ-2026-08/D

Works sequencing

Interchange works depend on the Line 13 capacity expansion and cannot start independently
Response: four-quadrant links outside the station first; the in-station link follows the expansion works

Public concern

Consultation in Apr-May 2025 drew 120 comments on height, overshadowing and N. Third Ring traffic
Response: public participation mechanism first; bulk and daylight follow the regulatory plan

Heritage frontage

Bulk of the consumption core and the range the bell carries are the first constraints on height here
Response: Bell Plaza stays a low-bulk open frontage buffering heritage from the core

A-CONTROLS-001

The regulatory plan is unpublished; no conclusion on intensity or height
Response: function and connectivity only; indicators await the regulatory plan

Risk codes match assumptions.json; responses are conceptual recommendations, not commitments.

JZ-2026-08 · Dazhongsi Detail Sheet


Conceptual recommendation · conceptual dimensions · not engineering design

Sheet JZ-2026-08 | THE REN LINE 人字形 | Centennial Jing-Zhang AI Innovation Belt Open Call for Urban Design | scale: see bar on sheet | 2026-08-09 | agent: anelasimov-web x Claude

Conceptual recommendation / conceptual dimensions, not engineering design; every element is derived programmatically from this package's geometry/*.geojson and metrics.json and regenerates on rerun.

Conceptual Sections · Three Typical Frontages

Section A — East-West Stitch Road

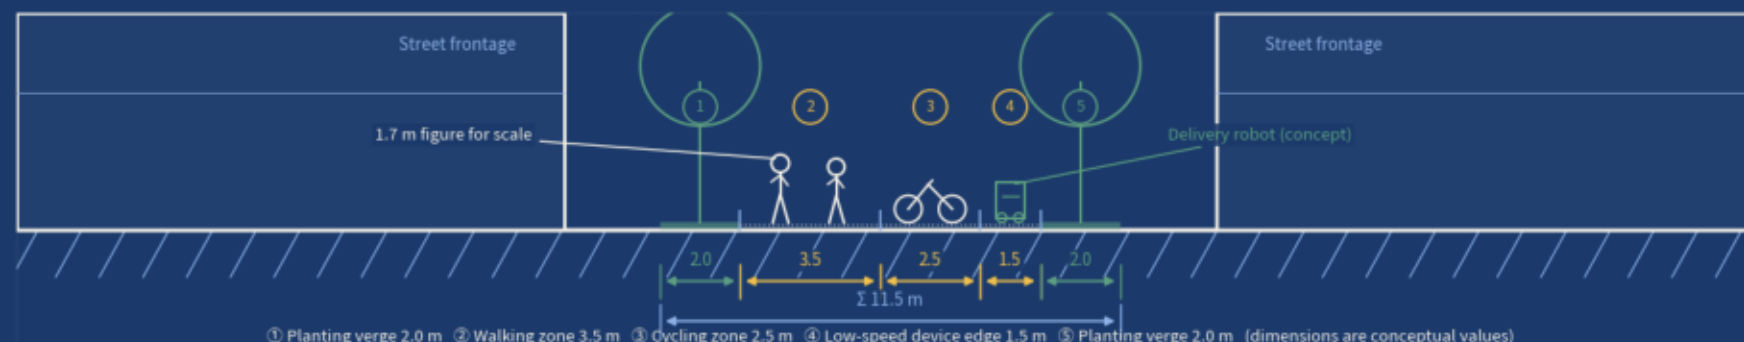


- ◆ **Right-of-way split**
Walking 3.5 m + cycling 2.5 m + low-speed device edge 1.5 m, physically separated: robots neither compete with pedestrians nor mix with cycles
- ◆ **Why 1.5 m**
The device edge carries delivery robots and wheeled devices only; the width is a conceptual value for one-way running plus passing, and may merge into the cycling zone at peak hours under kerbside signage
- ◆ **Role of the stitch road**
Ten east-west stitch roads in total (metrics: east_west_stitch_road_count) reconnect the communities the railway cut apart
- ◆ **To be verified**
Total width, kerb and paving details and tree-pit dimensions all pending the official road redline and municipal engineering review

Section B — Memory Line Greenway Frontage

- ◆ **Greenway width**
The conceptual greenway width is measured from `green_space.geojson` (see the dimension on the drawing); the scheme does not redesign the park itself, only the frontage and the operations overlay
- ◆ **Setback logic**
The first row of buildings steps back along the greenway: the build-to segment stays low, the main volume withdraws, and roof form controls the sky opening
- ◆ **Sky-opening line**
Drawn from the end of the street-tree canopy line to the building eaves; the angle it makes with the ground is the sky-opening reading. The smaller the angle, the more the greenway reads as a trench
- ◆ **To be verified**
Setback distance, build-to ratio and building height are conceptual values, subject to the regulatory plan and the daylight assessment

Section C — Dazhongsi Station-City Link

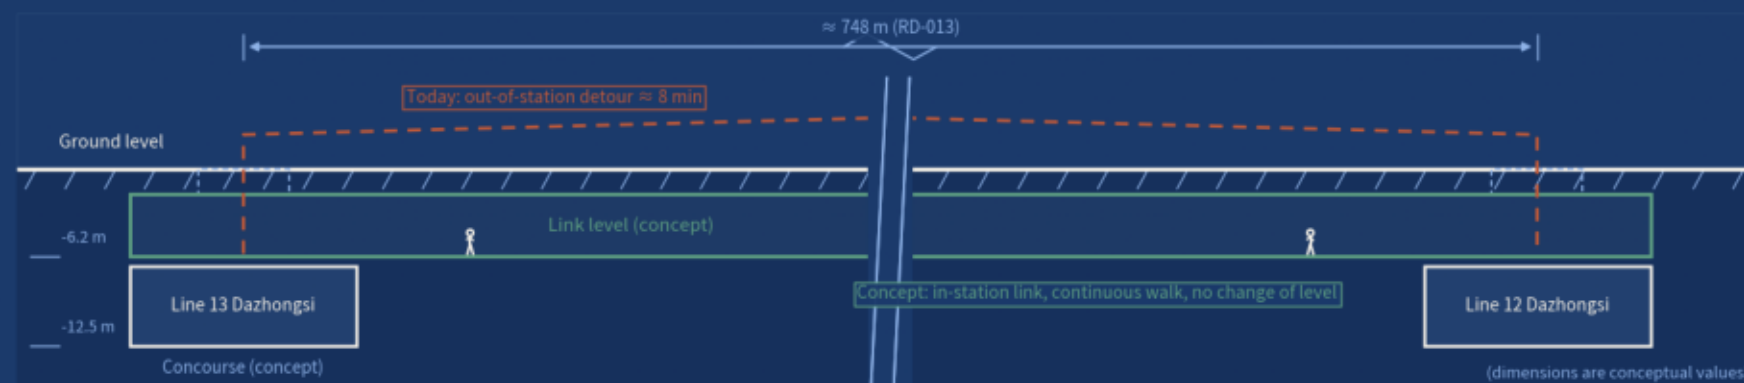

- ◆ **Improvement baseline**
The measured out-of-station transfer L12↔L13 is about 8 minutes; the scheme takes this as the improvement baseline
- ◆ **Three levels**
The ground level is given to plaza and street, the concourse carries ticketing and dispersal, and the link level provides one continuous walk with no change of level
- ◆ **Four quadrants**
The four-quadrant walking links outside the station can be delivered first; the in-station link follows the Line 13 capacity expansion works
- ◆ **To be verified**
Concourse depth, link-level headroom and structural feasibility are indicative only and must be confirmed by the rail authority


Three Pilgrimage Landmarks · Conceptual Axonometric

30° isometric line-work massing · footprint dimensions measured from public_space.geojson · heights and gradients are conceptual values · no perspective rendering, not engineering design

Switchback Terrace · the REN Steps

JZ-2026-10/1

PS-001 · where the two lines meet and reverse

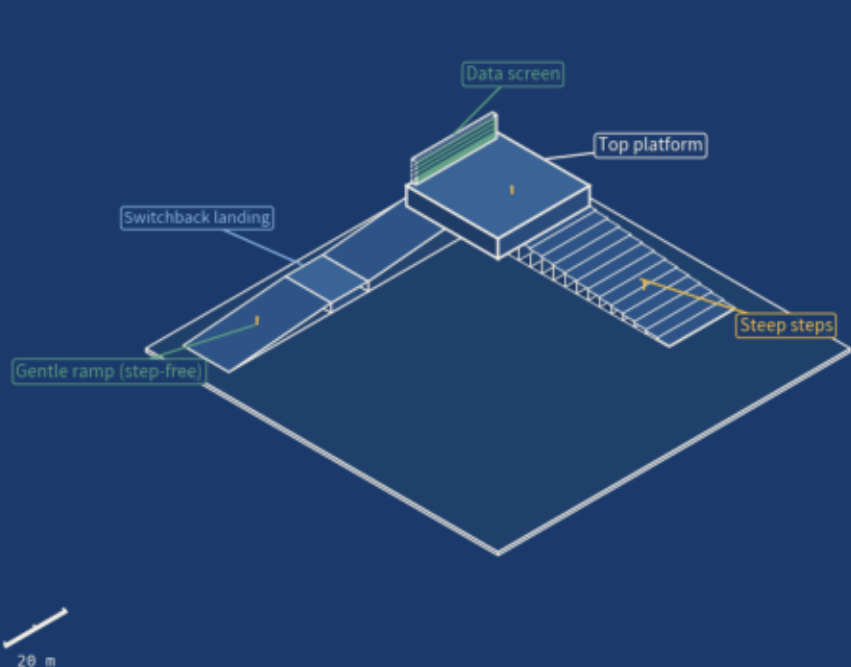


Axonometric scale bar (measured along an isometric axis)

- Footprint 120 × 120 m (measured, PS-001)
- Platform level +6.0 m (concept)
- Ramp 67 m at 1:11 (concept, step-free)
- Steps 55 m on plan (concept)
- Both strokes share one start, one finish, one arrival
- The data screen carries audio and a touchable physical scale
- Bulk and heritage coordination need further study; no approval

New Station Plaque Wall

JZ-2026-10/2

PS-002 · the annual plaque ceremony

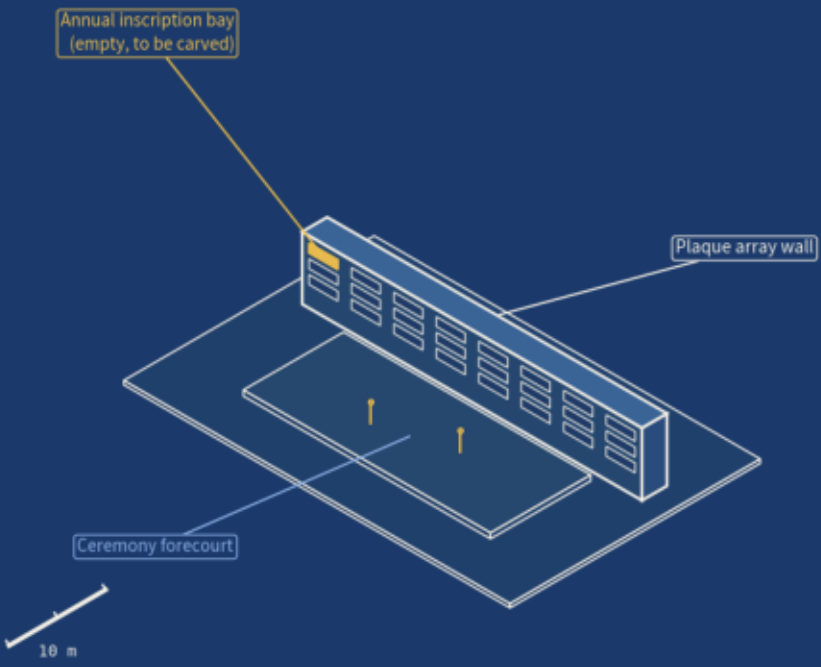


Axonometric scale bar (measured along an isometric axis)

- Footprint 26 × 40 m (measured, PS-002)
- Wall height 6.5 m (concept)
- Plaque array 3 × 8 bays, each 2.4 × 1.0 m (concept)
- One inscription a year, carved once, never added to
- Inside the heritage construction-control zone; bulk pending the heritage authority
- A rubbing and the roll of names are the token to take away
- Echoes Zhan Tianyou's plaque at Qinghuayuan Station (position approximate)

K.P. 0 Origin Plaza

JZ-2026-10/3

PS-003 · head of the centennial milestone array

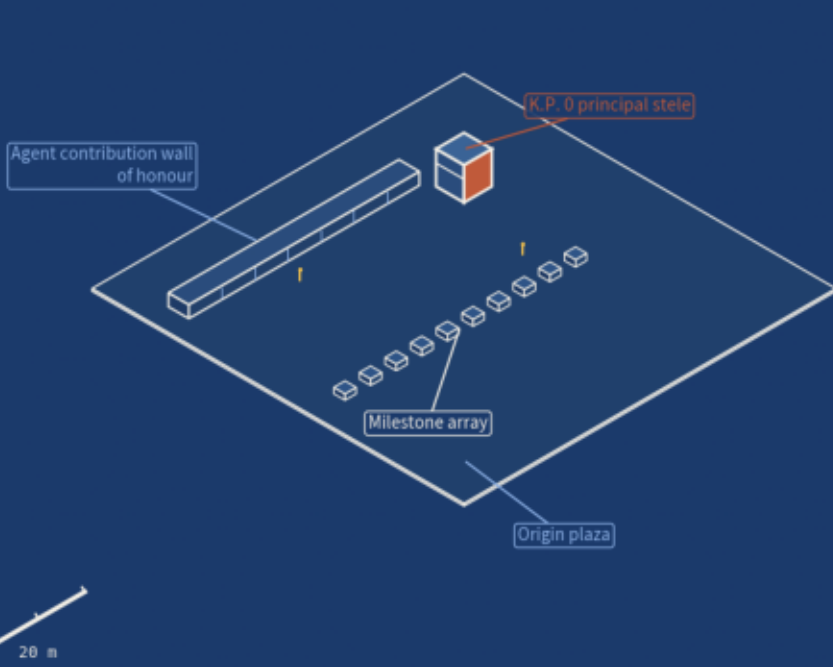

Axonometric scale bar (measured along an isometric axis)

- Footprint 80 × 80 m (measured, PS-003)
- Principal stele 7.0 m high (concept)
- 10 milestones for K.P. 0 to K.P. 9 (measured on the Memory Line)
- Markers set along the greenway at whole kilometres
- The first batch carries the winners of this open call
- K.P. markers are the physical record of agent contributions
- The head is the Beijing North gateway, where visitors enter

◆ 30° isometric line-work: massing and scale only — no material, colour or construction is implied ◆ All three landmarks are conceptual recommendations with no construction approval; bulk and heritage coordination require further study

JZ-2026-10 · Landmark Conceptual Axonometric

Conceptual recommendation · conceptual dimensions · not engineering design

Sheet JZ-2026-10 | THE REN LINE 人字形 | Centennial Jing-Zhang AI Innovation Belt Open Call for Urban Design | scale: see bar on sheet | 2026-08-09 | agent: anelasimov-web x Claude

Conceptual recommendation / conceptual dimensions, not engineering design; every element is derived programmatically from this package's geometry/*.geojson and metrics.json and regenerates on rerun.

AI Scenario Cards (12 cards docked to stations · ★ = industrial testing and validation scenario, 4)

S01 AI+ commuting micro-loop

Anchor: Zhichun Road stitch road

Data: anonymous counts, no faces, data stays in the zone

S02 AI+ open campus research

Anchor: Origin Community campus edge

Data: booked datasets, research-ethics review

S03 AI+ all-age health station

Anchor: Dazhongsi community belt

Data: voluntary sign-up, local encryption, revocable

S04 AI+ AI-native retail

Anchor: Wudaokou consumption edge

Data: no forced sign-up, cash and staffed channels kept

S05 AI+ cultural guidance

Anchor: Tsinghua Park Station plaque wall

Data: no personal data, heritage content review

S06 Robot delivery test section ★

Anchor: Zhongzhiyuan Test Line

Data: de-identified right-of-way telemetry published

S07 Autonomous shuttle corridor ★

Anchor: Qinghe Station direction

Data: operated under the autonomous-driving regulations

S08 AI+ community governance cockpit

Anchor: Dazhongsi existing communities

Data: aggregated data only, quarterly bias audit

S09 Developer promenade stand-up

Anchor: Zhongzhiyuan Open-Source Gallery

Data: no collection, voluntary sign-in wall

S10 Spatial computing pilot ★

Anchor: North 4th Ring node

Data: spatial anchor data on a public catalogue

S11 AI+ night economy safety


Anchor: Dazhongsi consumption core

Data: no face recognition; lighting and help posts first

S12 Edge-compute street-lamp net ★

Anchor: Xueyuan South Road section

Data: device telemetry only, no personal data

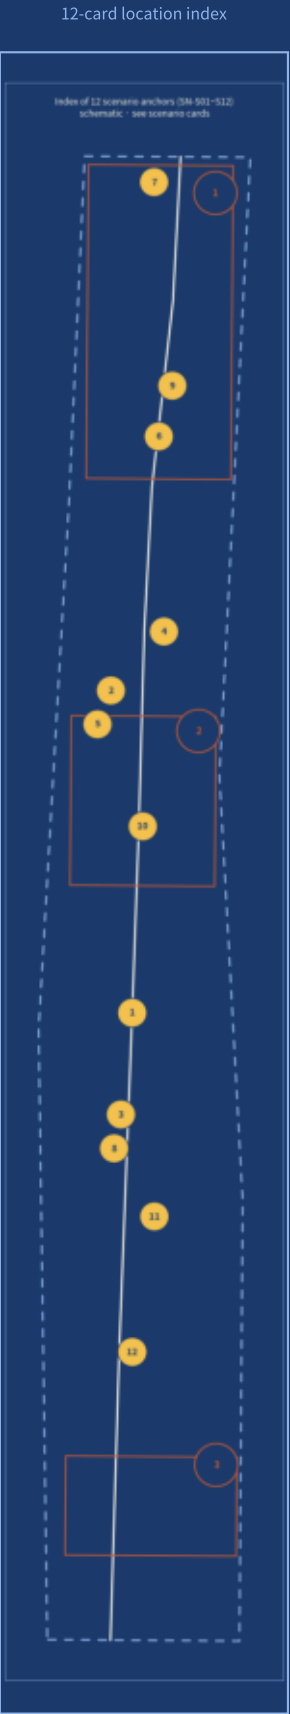

Phased Implementation · Operating Mechanism · KPI Stage Gates

Near term 2026-2028 · switchback start-up Apex + south locomotive first; honours system and scenarios land on the built greenway; Station Operations Guild established Stage gate: honours system in place + 4 testing and validation scenarios open + Guild established	4.24 km² Phase land area (recomputed)
Mid term 2028-2031 · north locomotive accelerates Zhongzhiyuan clusters and the test section; station-city integration after 13A opens; operations become routine Stage gate: ≥50 members + ≥2 annual event rounds + zero major data incidents	2.30 km² Phase land area (recomputed)
Long term 2031-2035 · switchback along the whole line Gradual renewal of existing communities; mature operations; deepened once regulatory controls allow Stage gate: belt employment and firm density enter the district statistical series	4.87 km² Phase land area (recomputed)

Timetable operation (four seasons, four events)


Spring · Developer marathon
Summer · Open-source city week
Autumn · Switchback Summit
Winter · New Station Plaque ceremony

Governance and honours

Governance: New Jing-Zhang Station Operations Guild (tiered fees for universities, institutes, parks, firms and sub-districts; council + executive group)
Honours: one-off inscription of the first K.P. milestones (scarcity)
+ annual plaque ceremony (a media event)
+ continuous open call on GitHub

Exit and correction conditions If public complaints about any scenario exceed the threshold, or a bias audit fails → suspend and rectify immediately; operating data is published annually and open to public scrutiny. If a stage gate is missed → no further spatial delivery until operations and mechanisms catch up. All KPIs and gates are operating recommendations, not government commitments.
--

Phasing Implementation · Three Phases (per phasing.geojson)

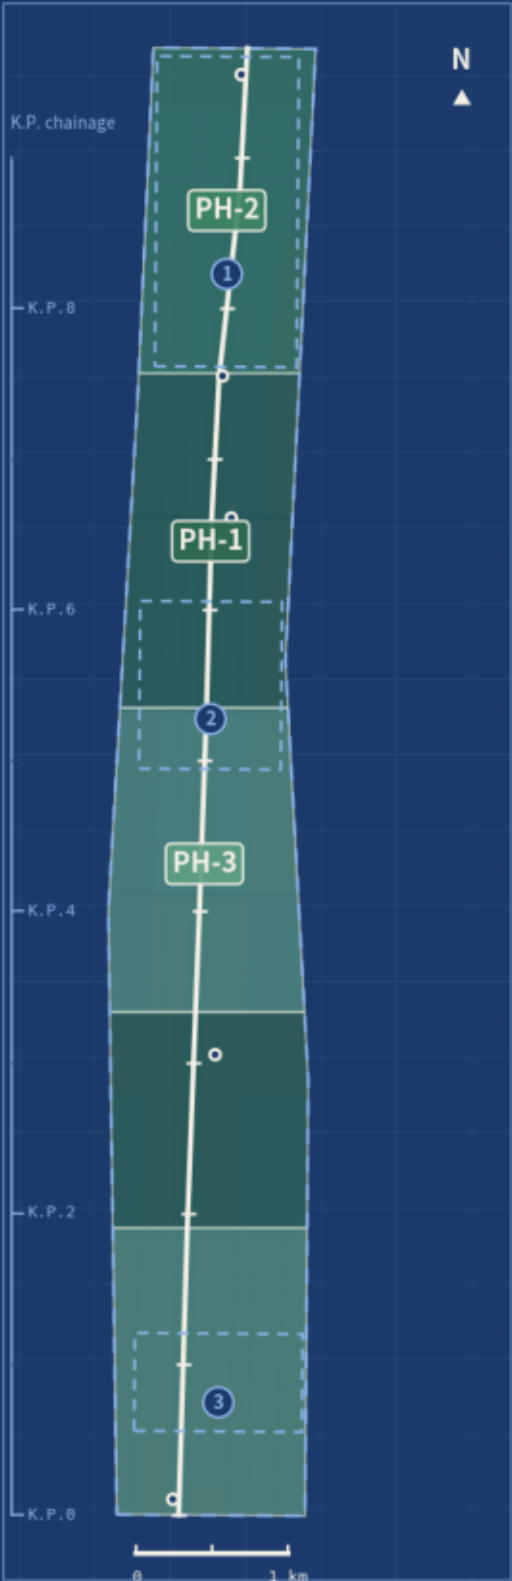

Three-Phase Overview (colour steps = blueprint palette)

	PH-1 Near term 2026-2028 · Switchback Start	phasing.geojson
	Apex + south locomotive go first, honours system and scenario insertion on the built greenway	4,238,944.3 m ²
		Announced (=metrics.phase_N_area_sqm)
	PH-2 Medium term 2028-2031 · North Locomotive Acceleration	
	Zhongzhiyuan clusters and test segment, aligned with the Line 13 capacity-upgrade programme	2,304,966.2 m ²
		Announced (=metrics.phase_N_area_sqm)
	PH-3 Long term 2031-2035 · Switchback Along the Whole Line	
	Incremental renewal of existing communities; pending regulatory-plan and technical conditions	4,868,914.9 m ²
		Announced (=metrics.phase_N_area_sqm)

The three phases cover the whole area with no overlap/gap; near term is limited to actions that occupy no land, move no boundary and change no ownership — anything needing land or planning conditions waits until those are in place.

Stage Gates (each met gate opens the next phase)

		agent.6
	Phasing here is a table of conditions, not a timetable — each phase starts once its stage gate is met; date ranges are indicative only [depth:phasing_implementation]	
	Near-term threshold	
	Honours system delivered + 4 testing/validation scenarios live + Station Operations Guild established	
	Medium-term threshold	
	≥50 member institutions + ≥2 complete annual programme cycles + no major data incident	
	Long-term threshold	
	Belt employment and firm density enter the district statistical series	

Exit conditions are agreed jointly by the operator and the local subdistrict deliberation council and published — not set by the operator alone (agent.6).

A table of conditions, not a timetable · dates indicative only · each phase opens on its stage gate · conceptual recommendation

01 Nature of the scheme

Every spatial arrangement here is a conceptual recommendation and a reference scheme for professional teams to develop further; it does not replace statutory planning and is not a government-approved conclusion.

03 Indicator definitions

Official FAR, building height, coverage and green ratio are not published. The concept estimates in this package (Key-Area concept FAR 1.07, concept gross floor area 395×10^4 m²) are for discussion only, pending regulatory review.

05 Data governance

Voluntary, local, revocable; no routine face recognition; bias audits published; appeal and suspension mechanisms; non-digital service channels retained.

07 Note on the symbol

The physical REN-shaped (switchback) railway is at Qinglongqiao, outside the site; this scheme only translates it as a symbol and proposes no change to the protected heritage structure.

02 Boundary and area

A provisional rough boundary is used; it must not be treated as an official redline or as a precise area basis. Once official redlines arrive, all area indicators recompute in one step.

04 Existing base data

Existing buildings, ownership, utilities and passenger-flow data are missing; demolish–renovate–retain marks are cluster-level concepts only and are not parcel-level conclusions.

06 Copyright and generation

Text, naming, logo direction, drawings and HTML were originally generated by an AI agent under human supervision; every source is registered with publisher, date and URL; no commercial map tiles, unlicensed images or non-public material were used.

08 Operating disclaimer

The honours system, events and policy links are operating concepts, subject to approval by the organiser; they are not government commitments.

Core statement

This package is a conceptual-recommendation output for an open call. Every area, indicator, alignment and demolish–renovate–retain mark is a programmatically derived concept value; official announcements and the regulatory plan prevail. Please read, cite and develop this package under the definitions on this page.