



01 区位与三层范围分析

统筹研究范围 / 总体设计范围 / 重点区域范围套合，叠加区域协同方向

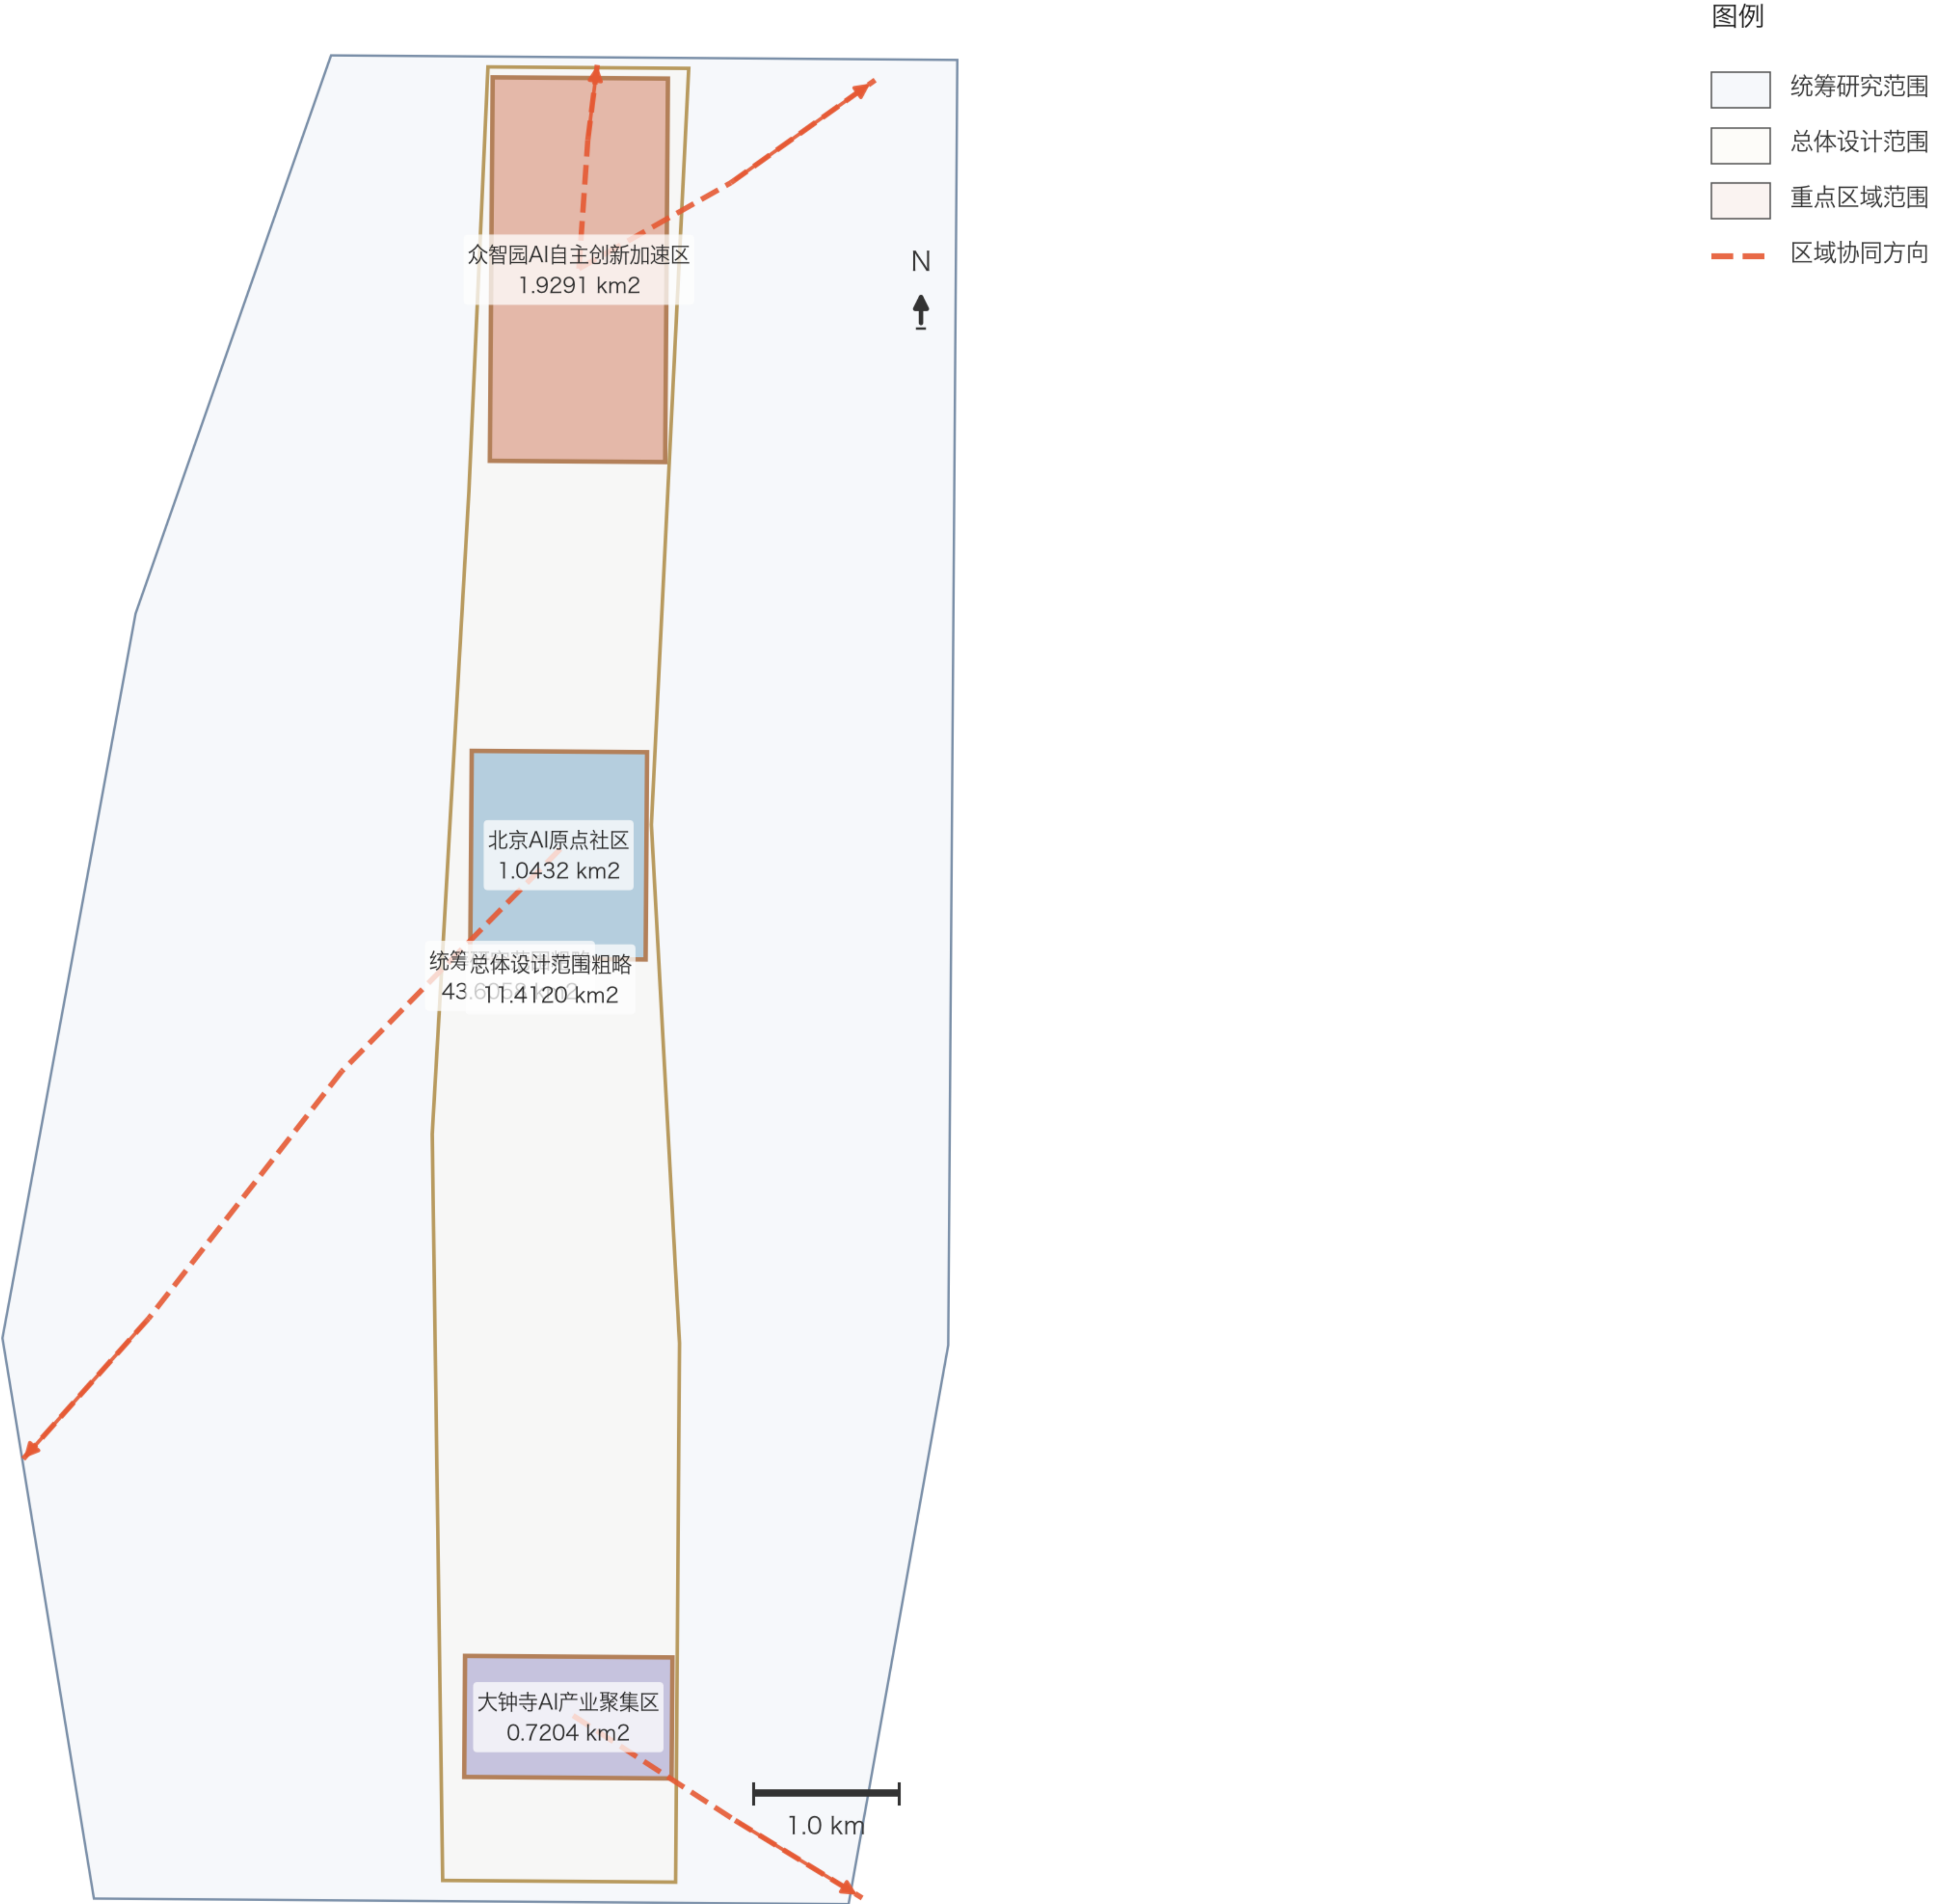

02 空间结构总图

三区两翼 + 京张文化脊 + 东西缝合廊 + 智创回路

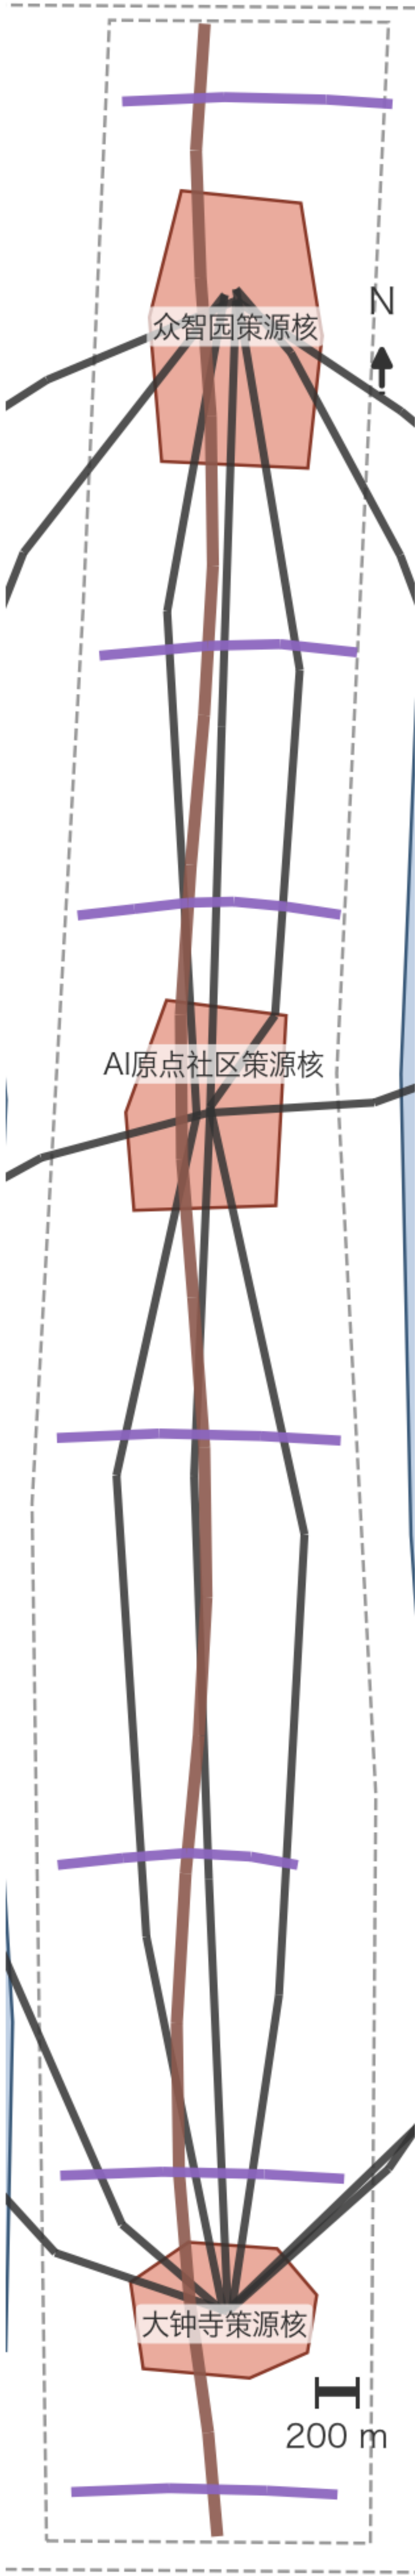


空间结构

- 中关村科技服务翼
- 三区策源核
- 智创回路
- 京张铁路遗产线
- 东西缝合廊/桥

03 土地利用规划图

按用地代码分色，面积与占比由 Geod 反算

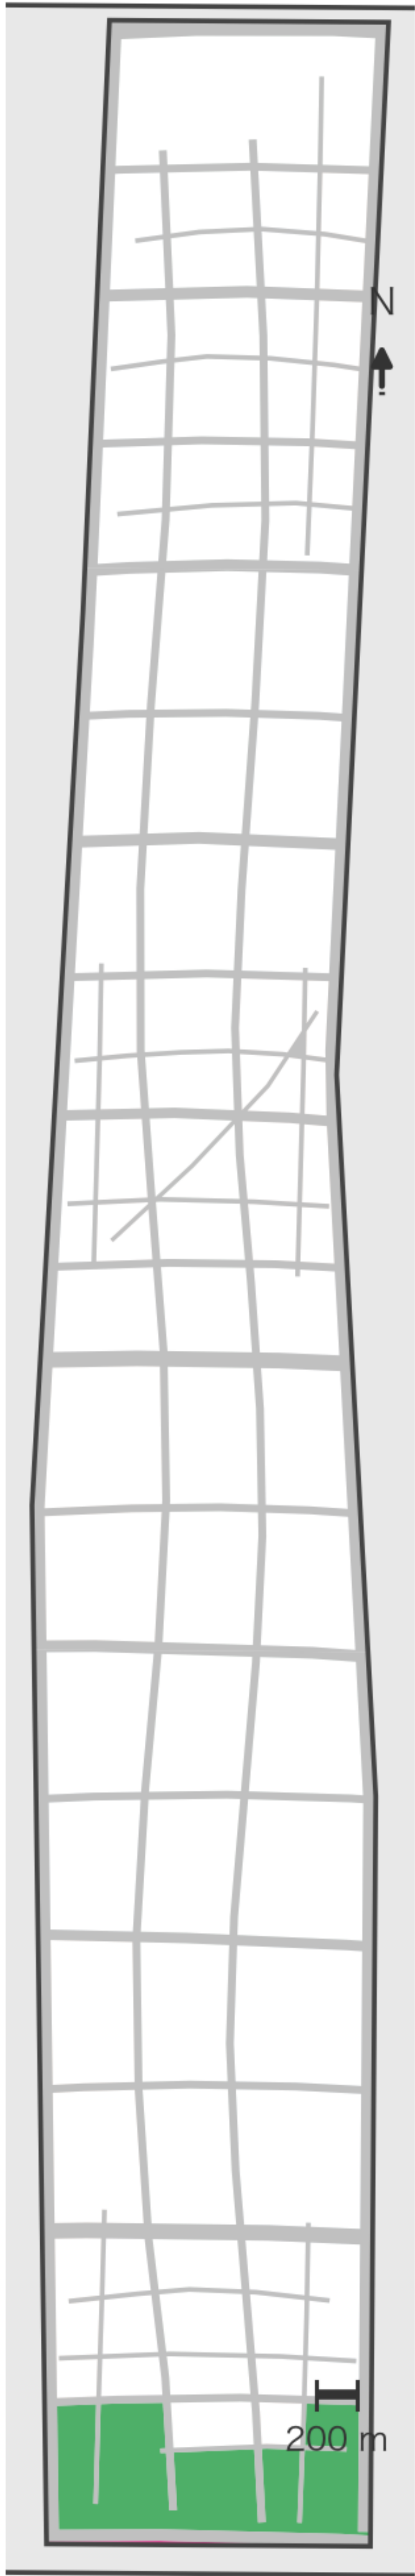


土地利用（按面积降序）

- 1401 公园绿地
362.0 ha (31.7%)
- 1207 城镇村道路用地
250.2 ha (21.9%)
- 0802 科研用地
215.7 ha (18.9%)
- 0804 教育用地
88.3 ha (7.7%)
- 05 商业服务业用地
74.8 ha (6.6%)
- 0805 体育用地
45.4 ha (4.0%)
- 0701 城镇住宅用地
44.5 ha (3.9%)
- 0702 城镇社区服务设施用地
37.1 ha (3.3%)
- 0803 文化用地
22.2 ha (1.9%)
- 0806 医疗卫生用地
1.1 ha (0.1%)


04 道路交通与慢行系统图

道路分级设色 + 站域影响区 + 缝合廊桥

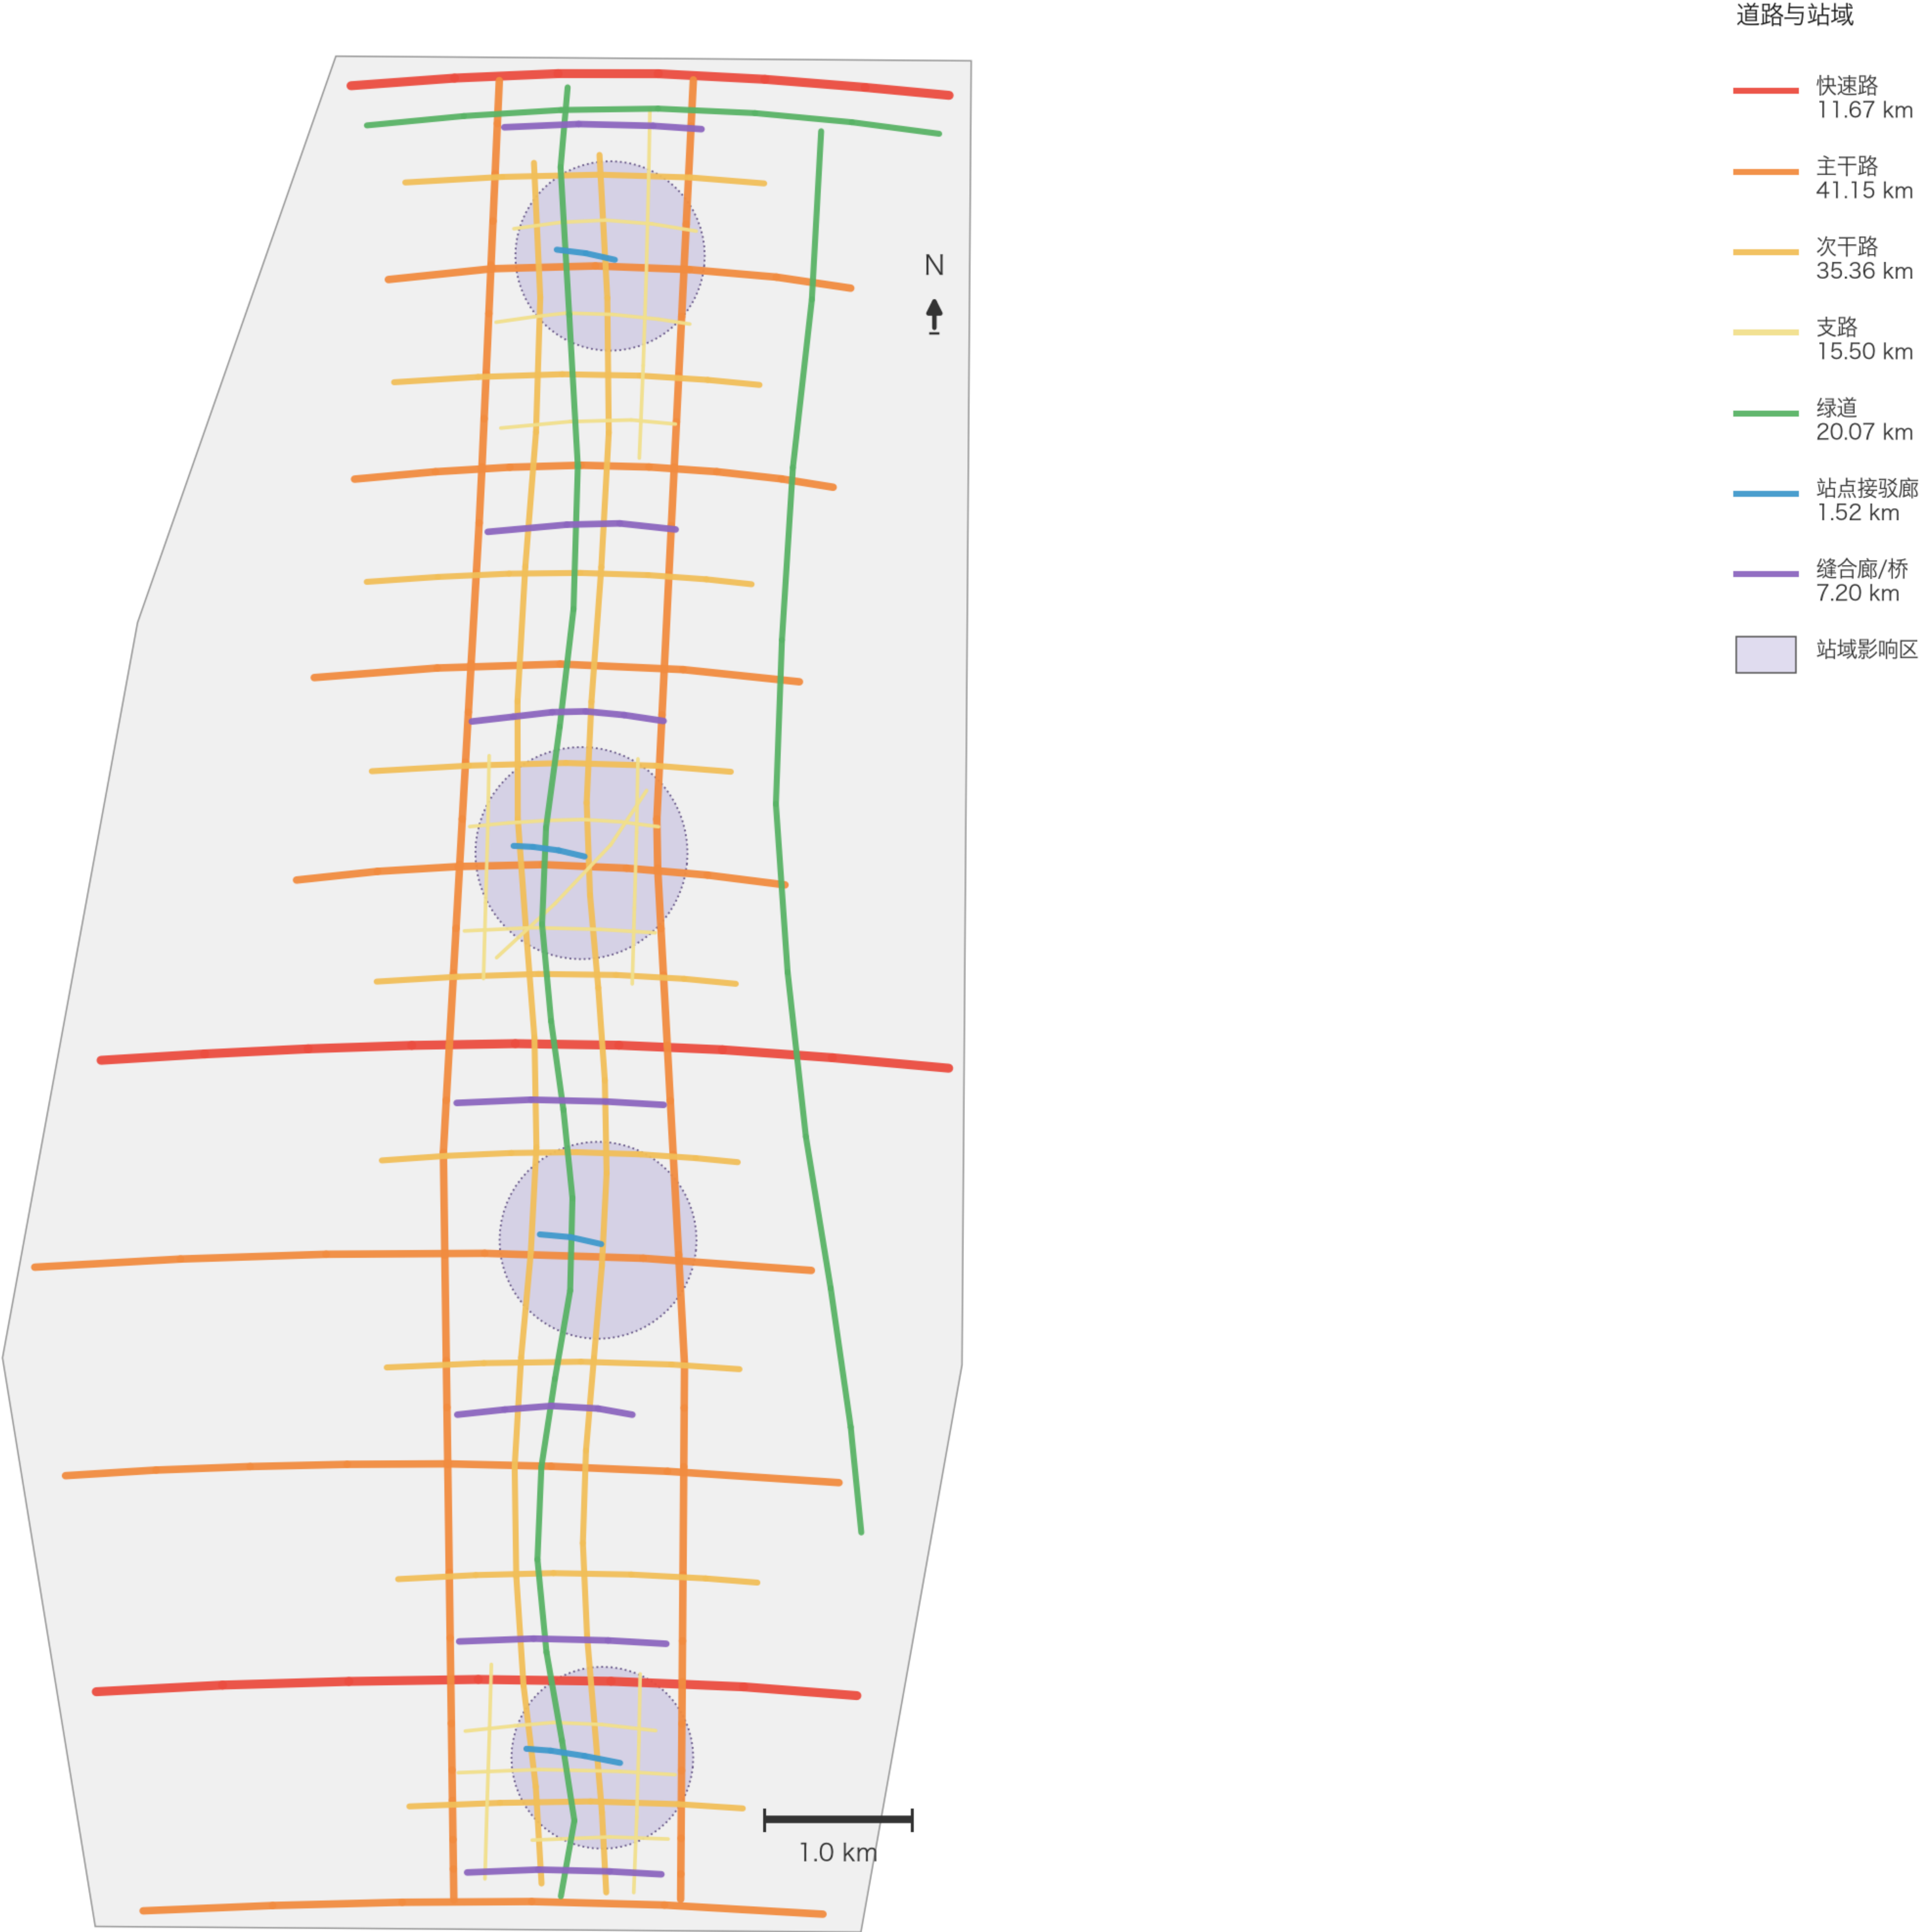

05 公共空间与绿地系统图

绿脊、社区公园、滨水绿带与公共空间、三处地标

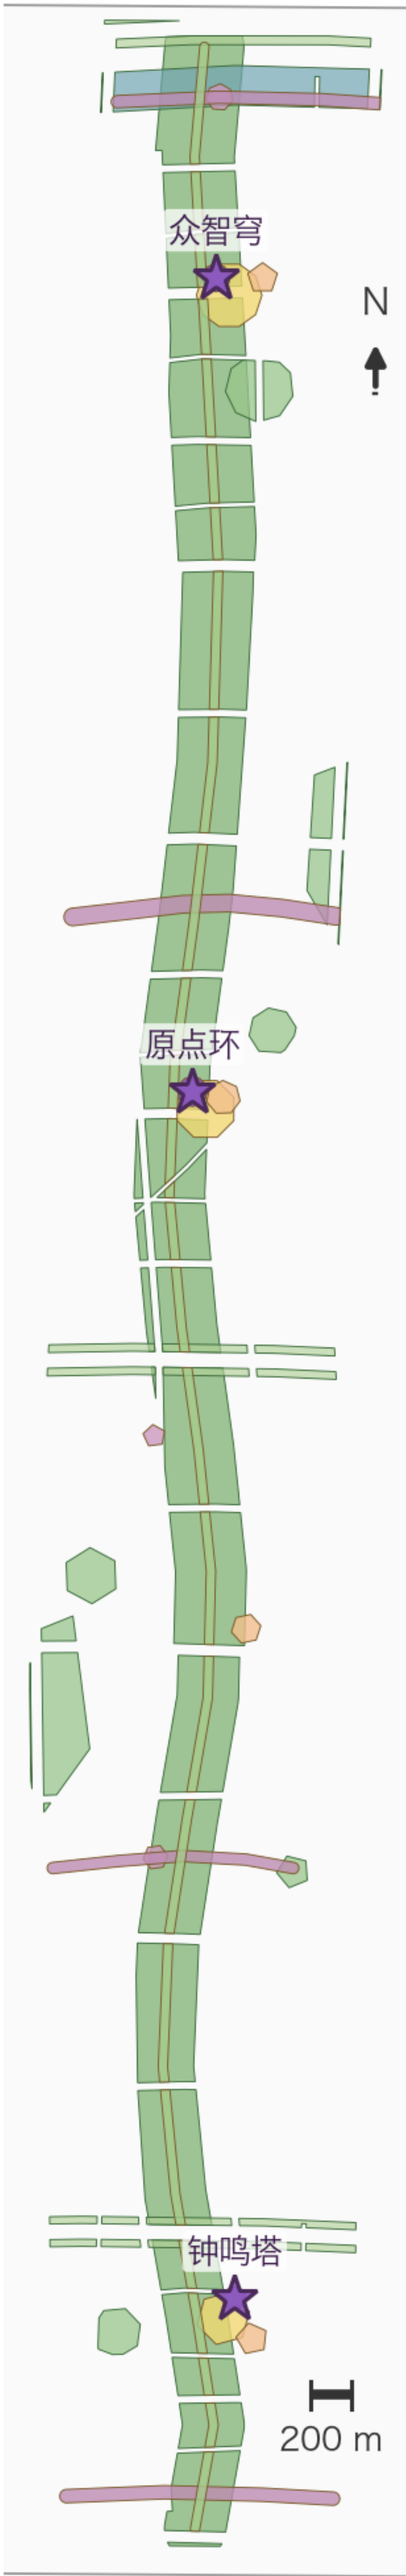

绿地与公共空间

- 京张遗址公园绿脊 228.1 ha
- 防护绿带 15.9 ha
- 滨水绿带 14.8 ha
- 楔形绿地 13.1 ha
- 社区公园 12.8 ha
- 线性公共空间 31.7 ha
- 缝合廊 22.0 ha
- 片区广场 11.4 ha
- 站前广场 3.8 ha
- AI地标 2.5 ha
- 缝合节点 1.8 ha

06 分期实施图

四期实施范围与面积（按 Geod 反算）

