

百年京张AI创新带 城市设计开源征集

方案名：智源·京张 — 智能化AI活力城市


三大定位：

- 智能化AI活力城市
- 世界级AI创新生态
- 百年京张文化带




01 区位与三层范围分析

统筹研究范围 / 总体设计范围 / 重点区域范围套合，叠加区域协同方向

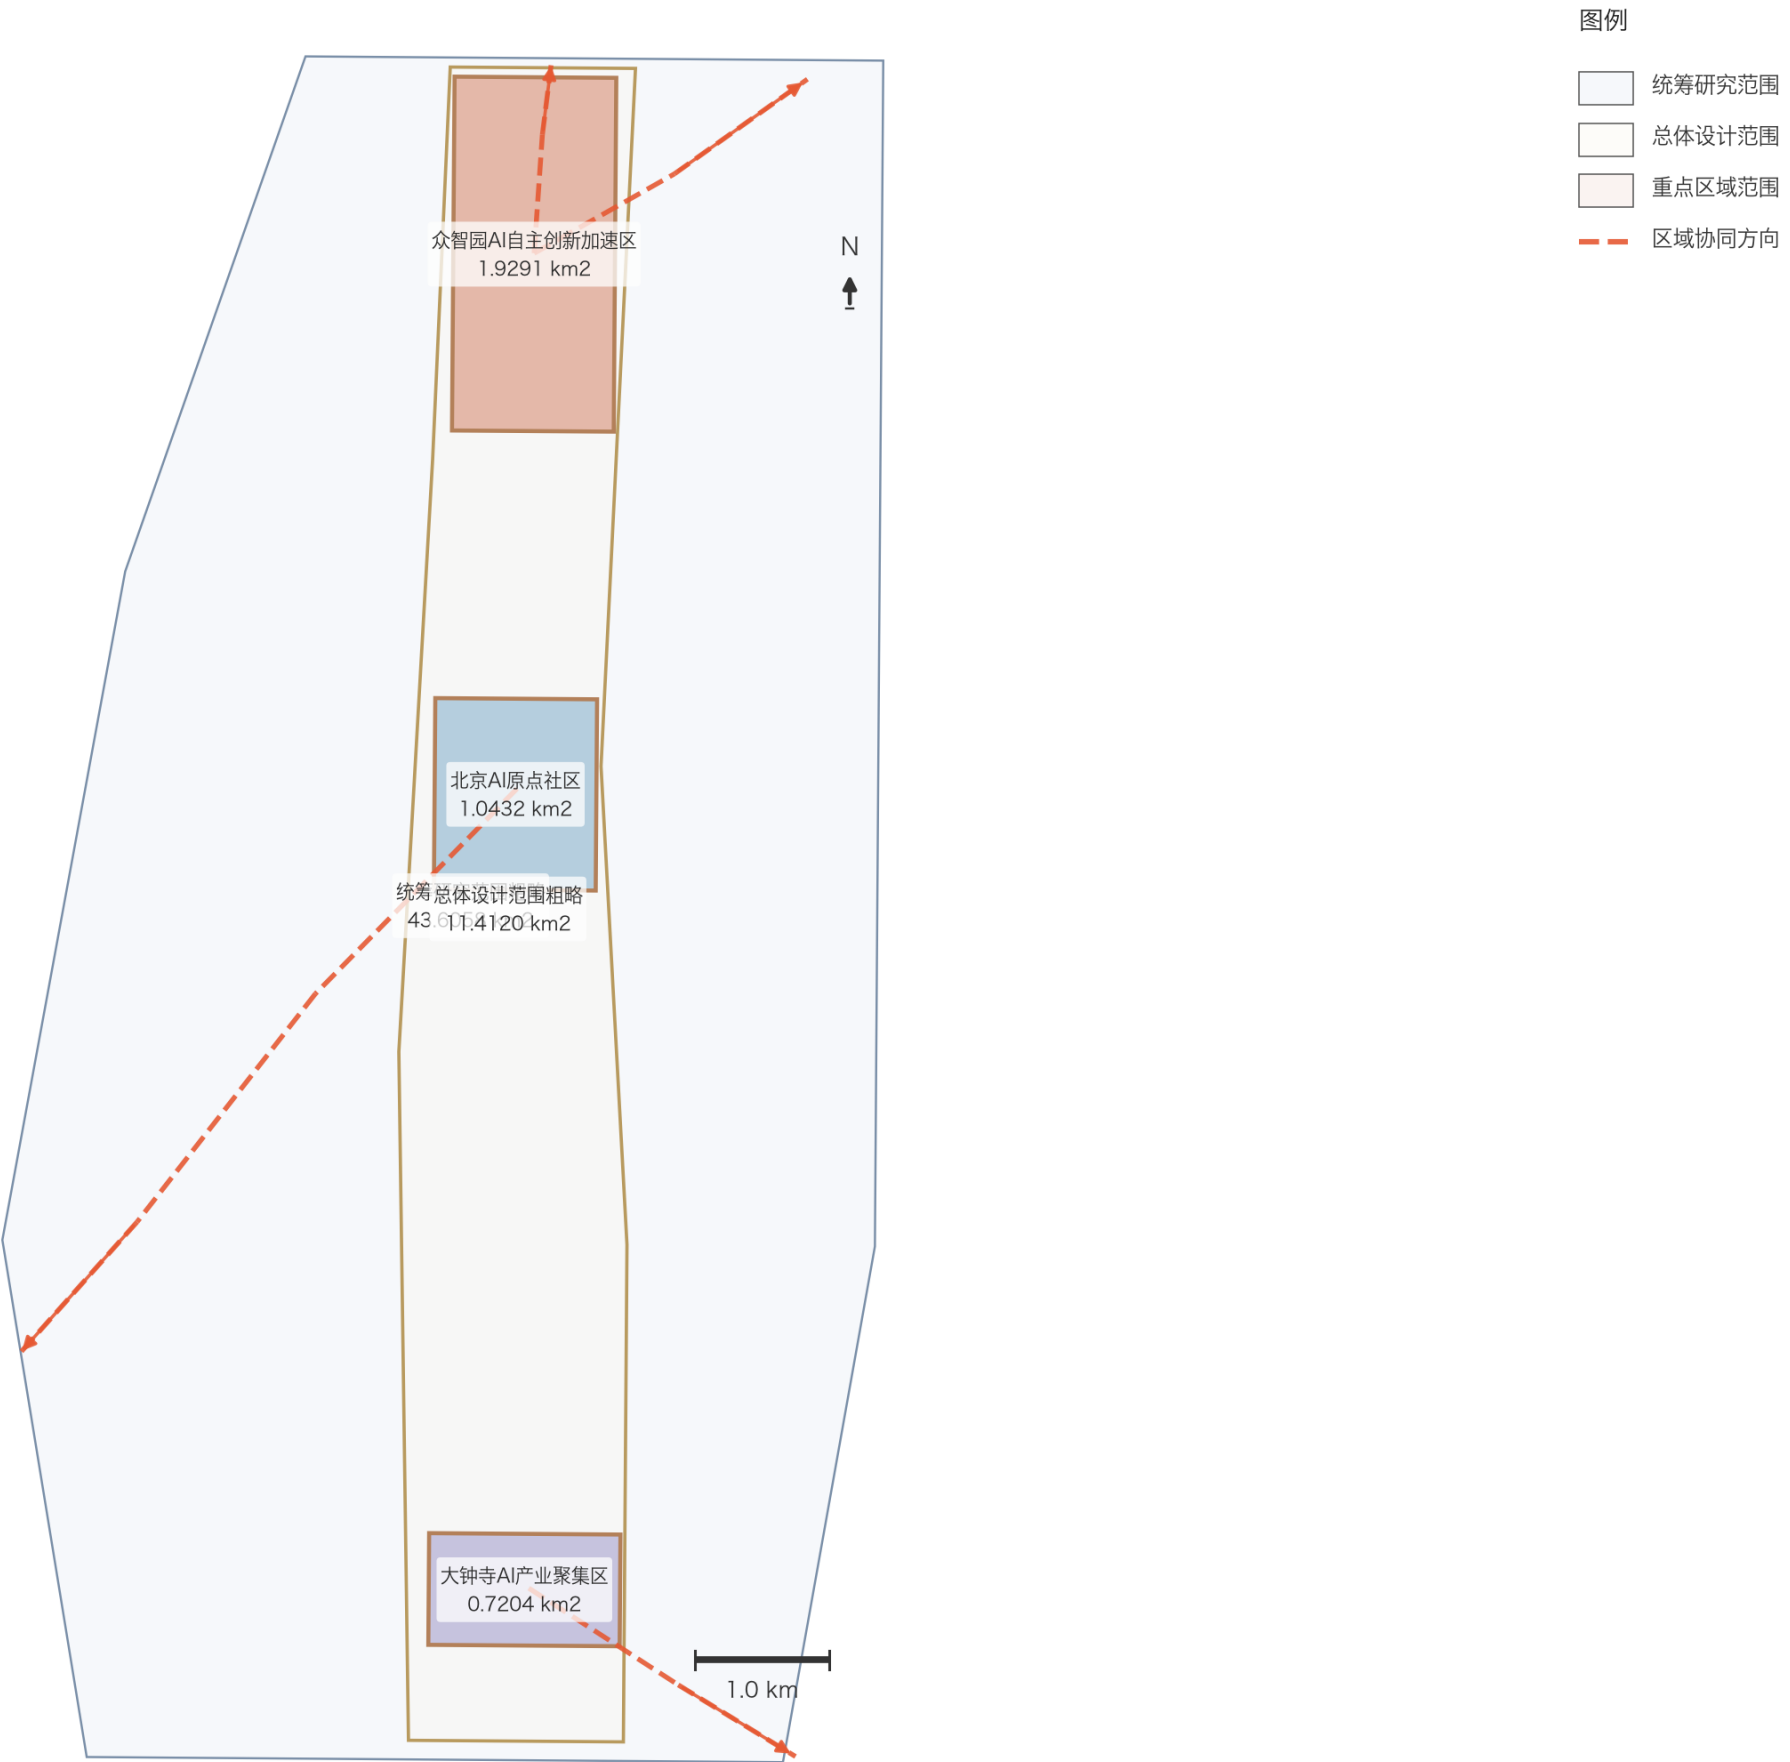

02 空间结构总图

三区两翼 + 京张文化脊 + 东西缝合廊 + 智创回路

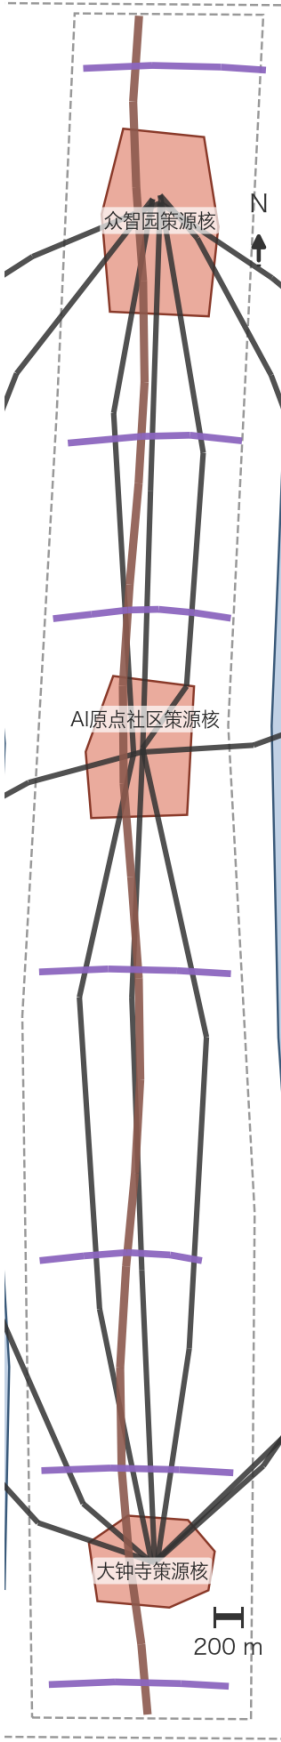


空间结构

- 中关村科技服务翼
- 三区策源核
- 智创回路
- 京张铁路遗产线
- 东西缝合廊/桥

03 土地利用规划图

按用地代码分色，面积与占比由 Geod 反算

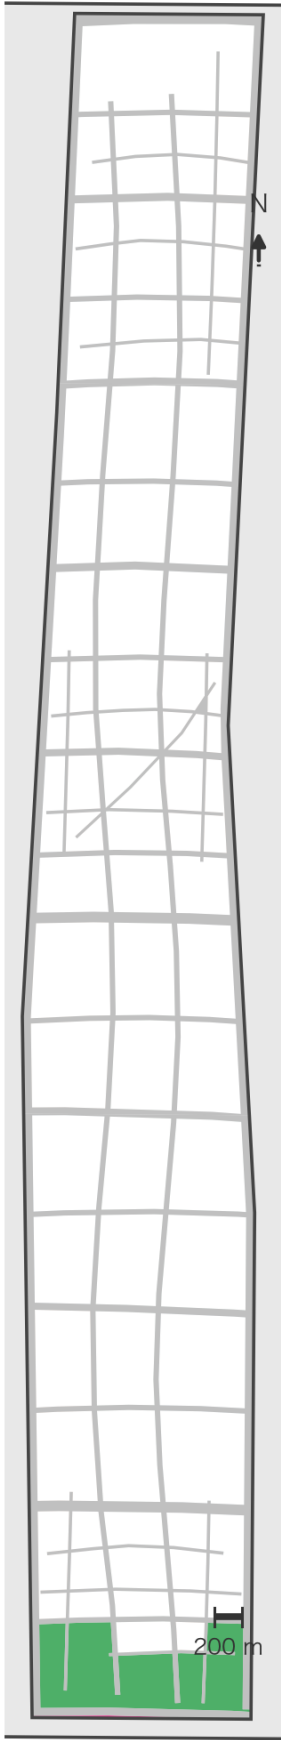


土地利用（按面积降序）

- 1401 公园绿地
362.0 ha (31.7%)
- 1207 城镇村道路用地
250.2 ha (21.9%)
- 0802 科研用地
215.7 ha (18.9%)
- 0804 教育用地
88.3 ha (7.7%)
- 05 商业服务业用地
74.8 ha (6.6%)
- 0805 体育用地
45.4 ha (4.0%)
- 0701 城镇住宅用地
44.5 ha (3.9%)
- 0702 城镇社区服务设施用地
37.1 ha (3.3%)
- 0803 文化用地
22.2 ha (1.9%)
- 0806 医疗卫生用地
1.1 ha (0.1%)


04 道路交通与慢行系统图

道路分级设色 + 站域影响区 + 缝合廊桥

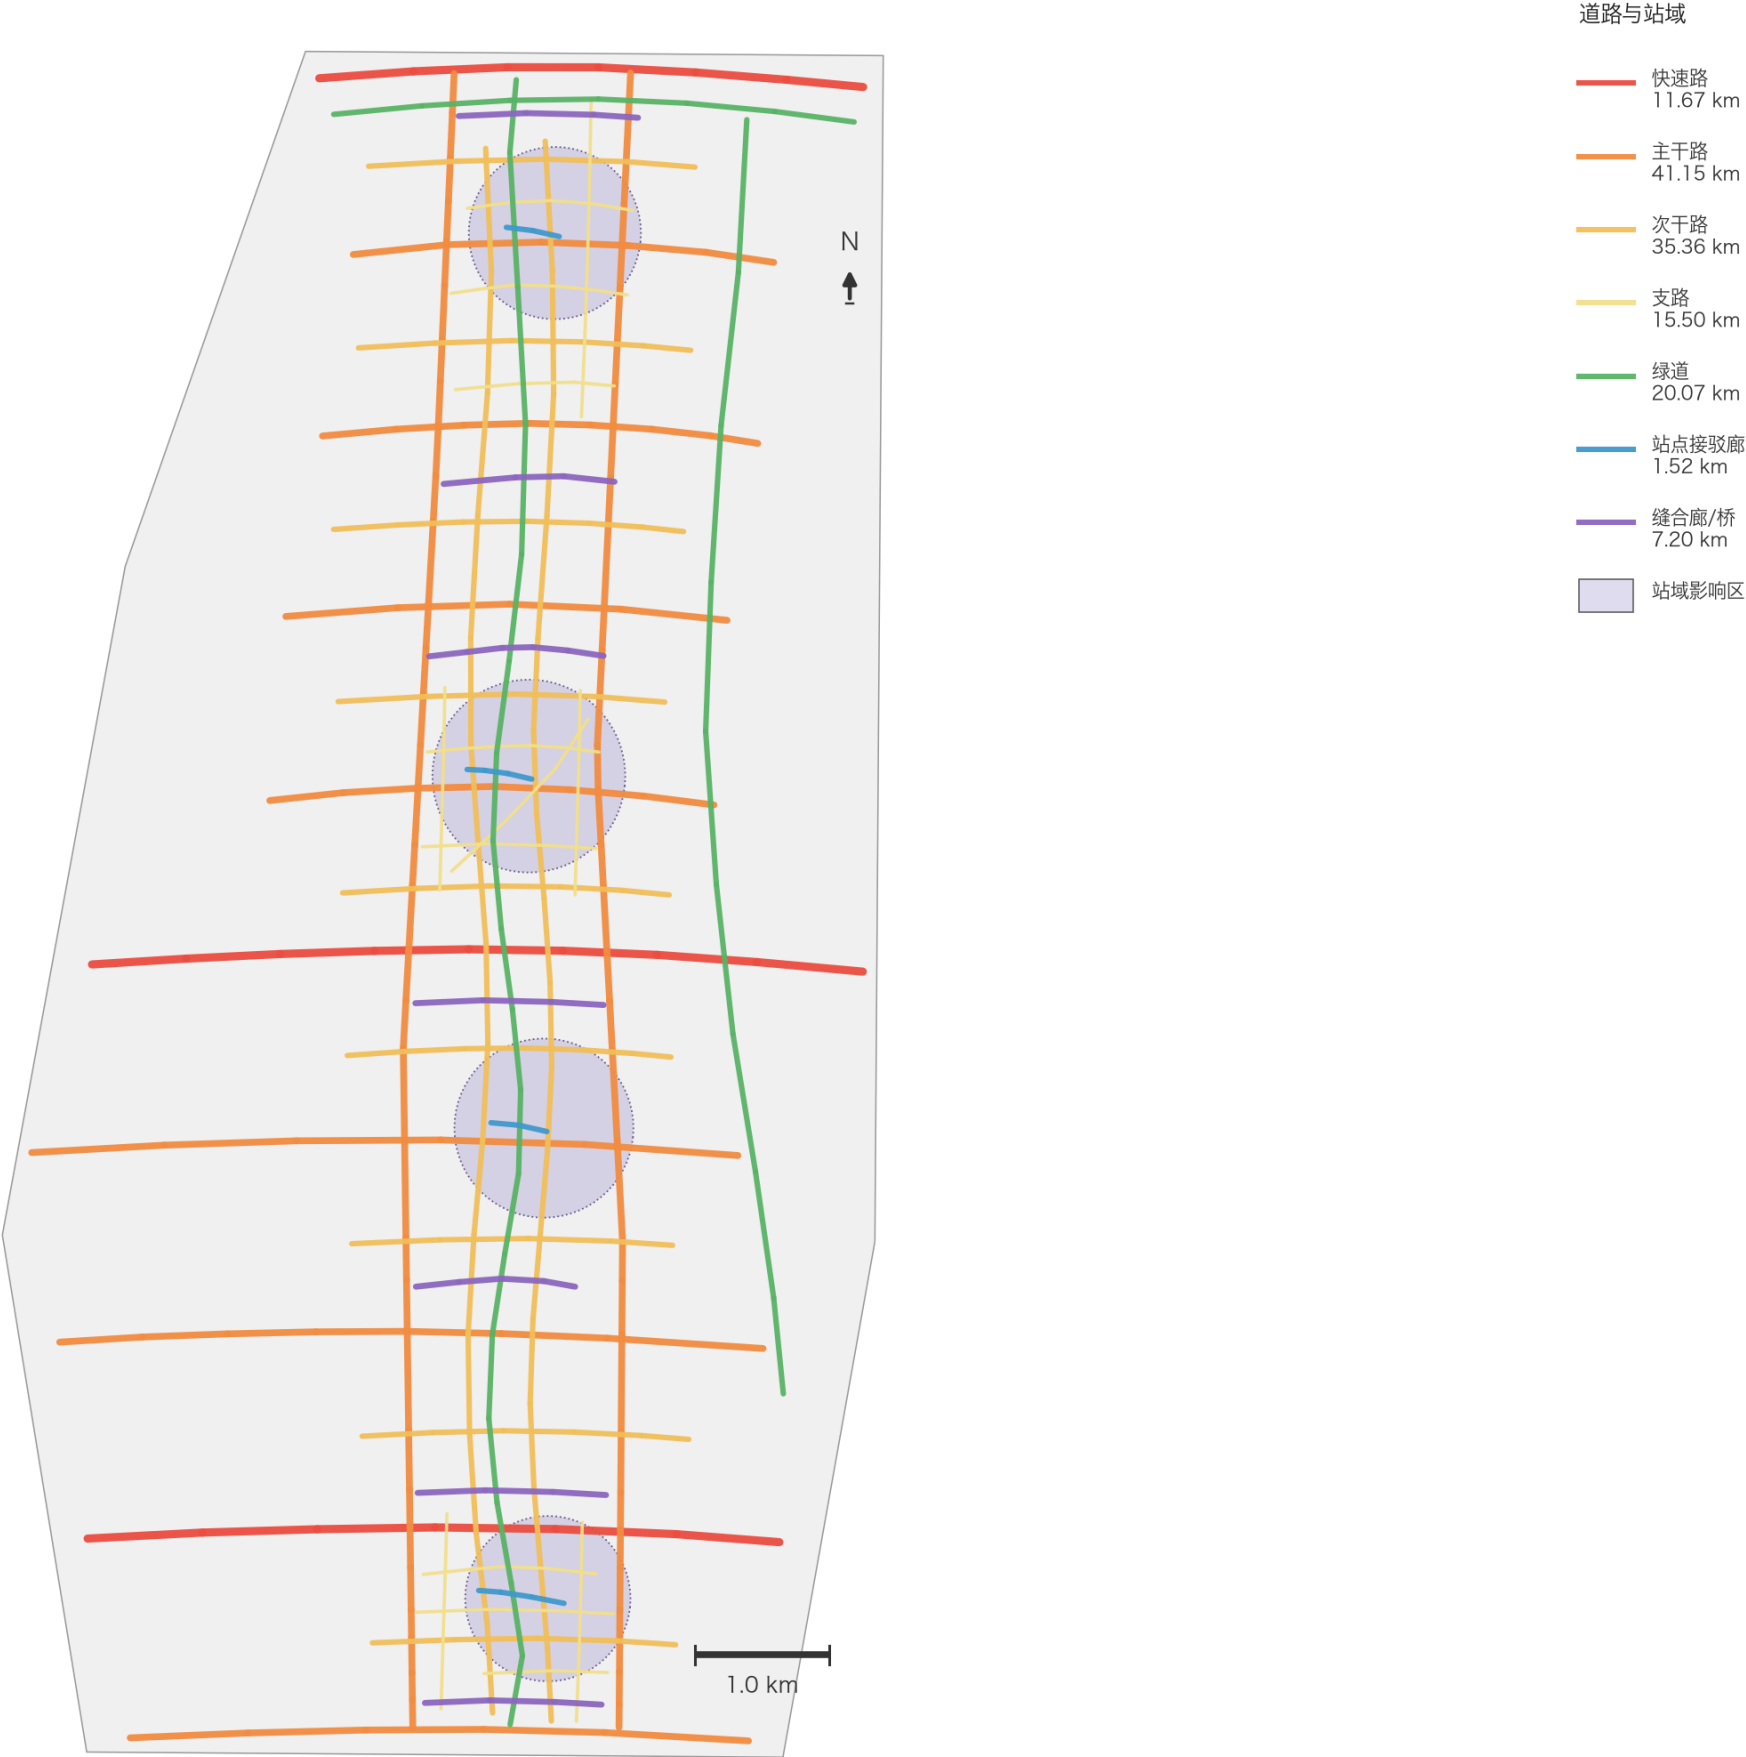

05 公共空间与绿地系统图

绿脊、社区公园、滨水绿带与公共空间、三处地标

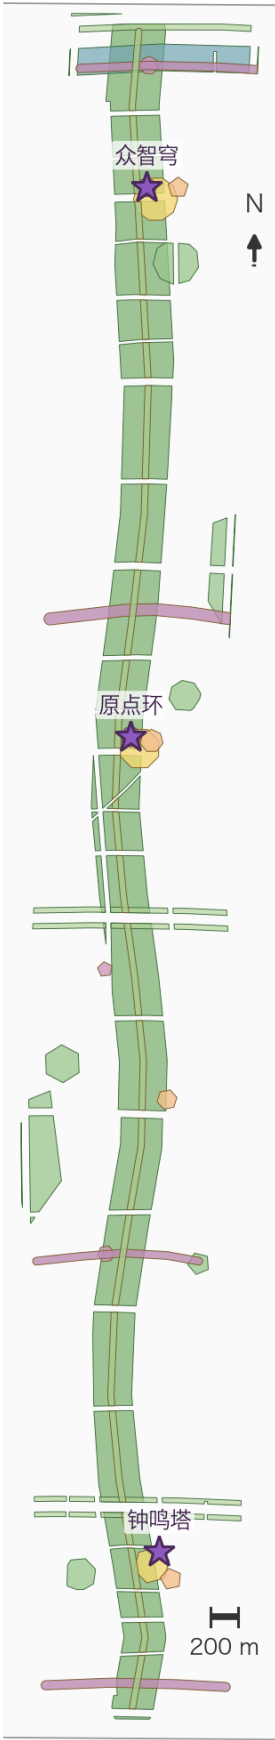


绿地与公共空间

- 京张遗址公园绿脊 228.1 ha
- 防护绿带 15.9 ha
- 滨水绿带 14.8 ha
- 楔形绿地 13.1 ha
- 社区公园 12.8 ha
- 线性公共空间 31.7 ha
- 缝合廊 22.0 ha
- 片区广场 11.4 ha
- 站前广场 3.8 ha
- AI地标 2.5 ha
- 缝合节点 1.8 ha


06 分期实施图

四期实施范围与面积（按 Geod 反算）

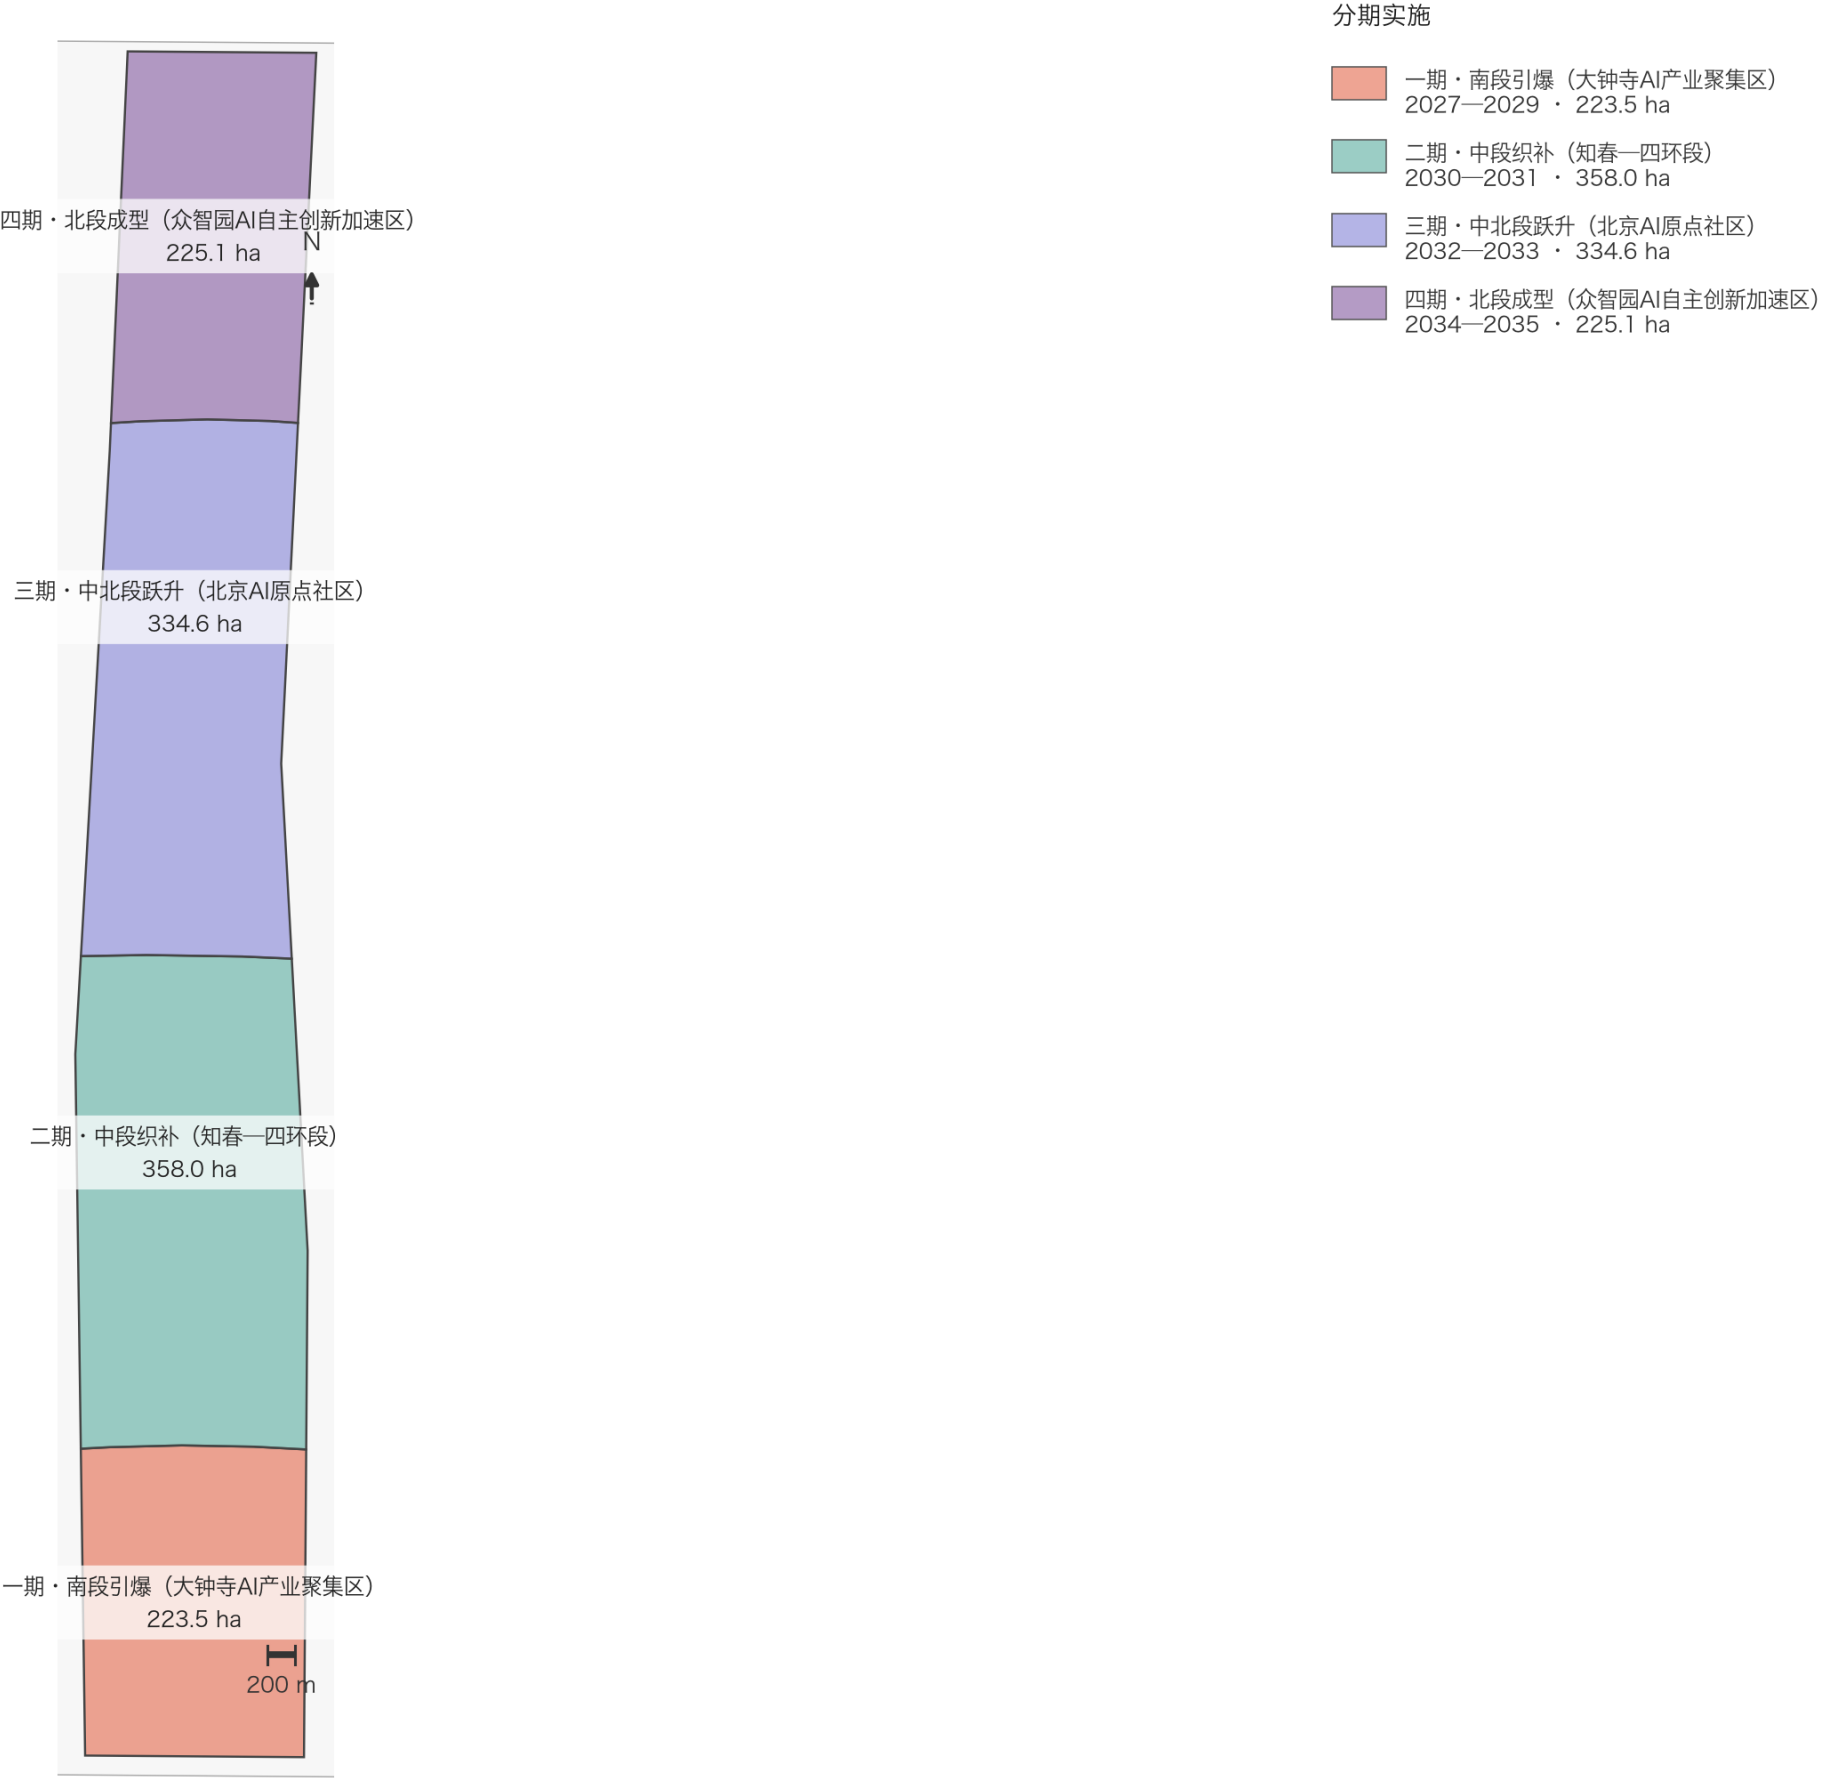


07a 重点区域放大：众智园AI自主创新加速区

众智园AI自主创新加速区粗略范围

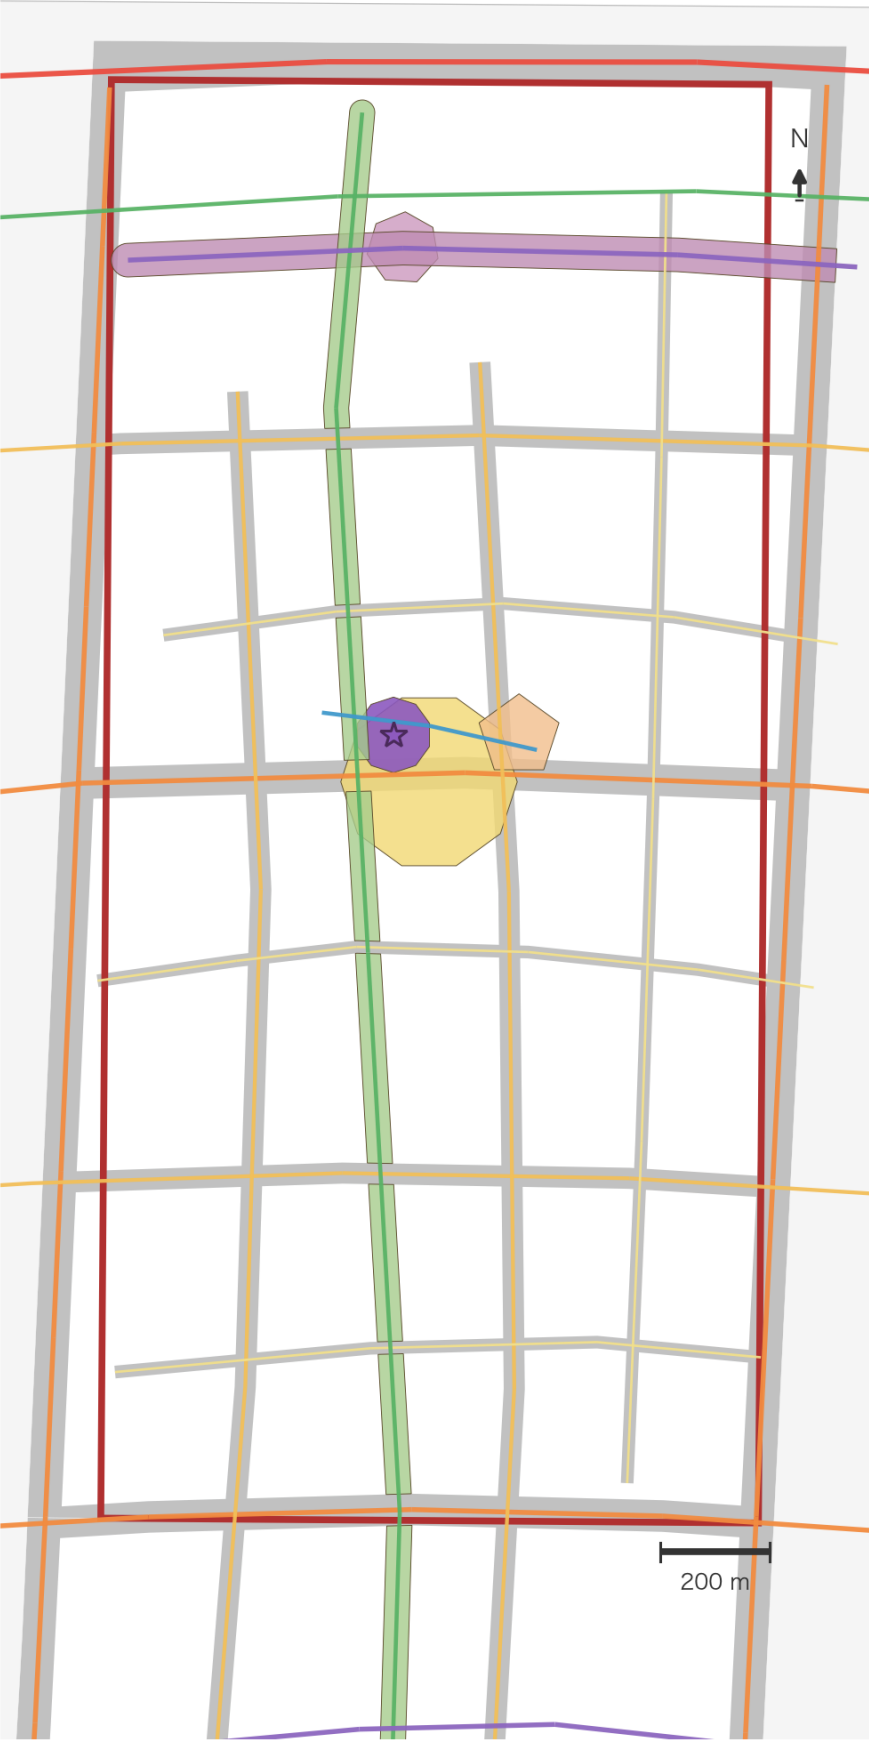


07b 重点区域放大：北京AI原点社区

北京AI原点社区粗略范围

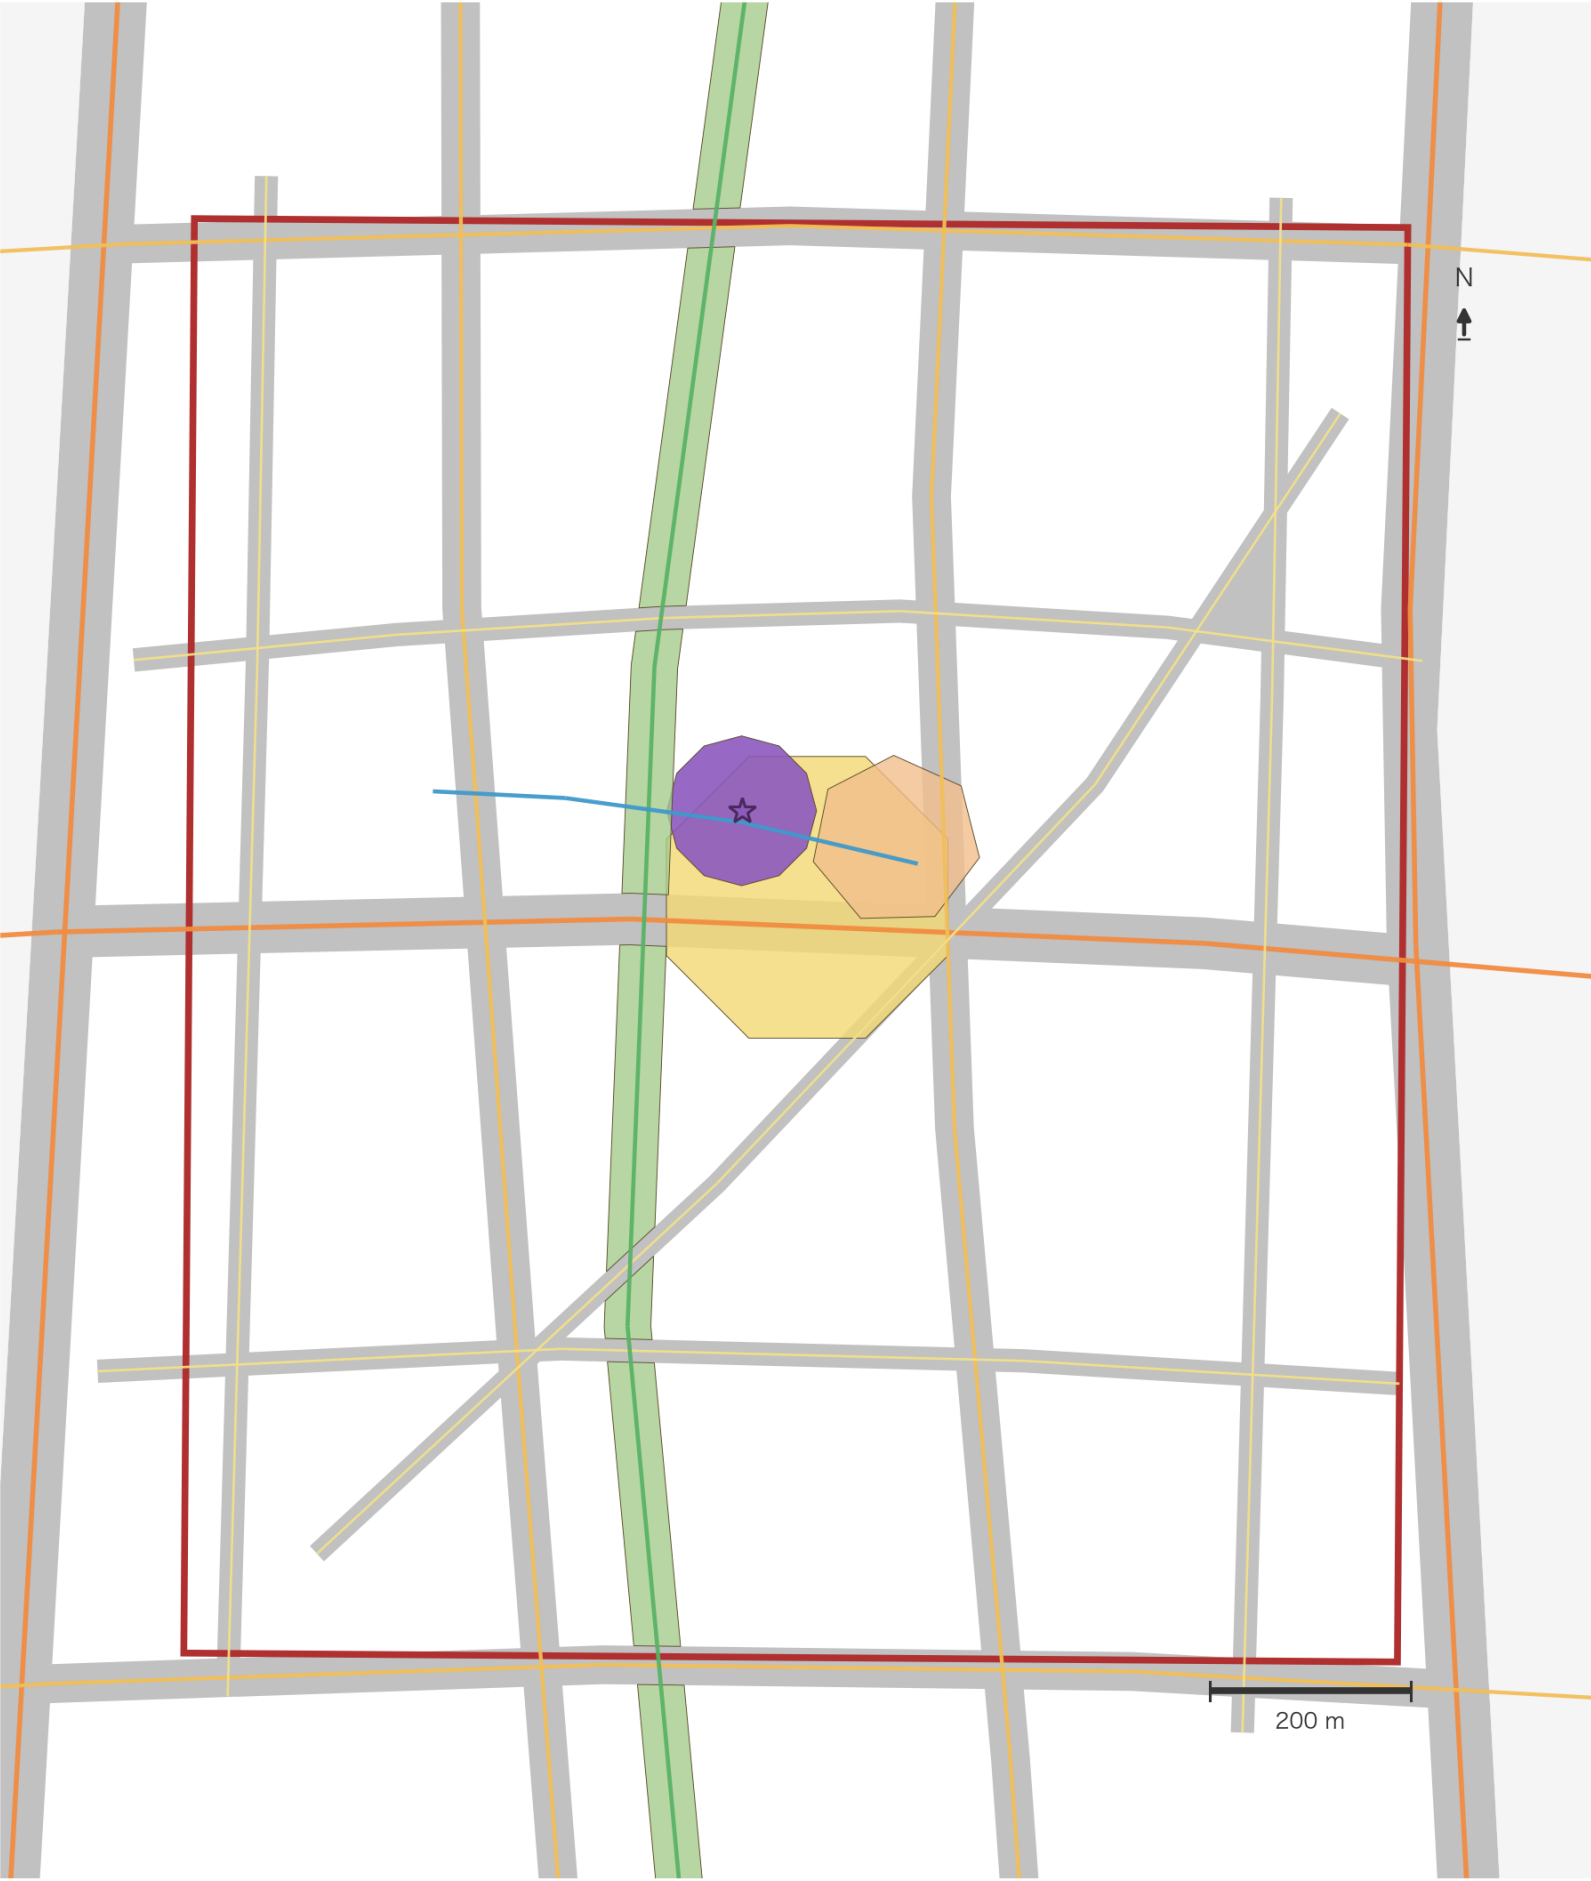


07c 重点区域放大：大钟寺AI产业聚集区

大钟寺AI产业聚集区粗略范围

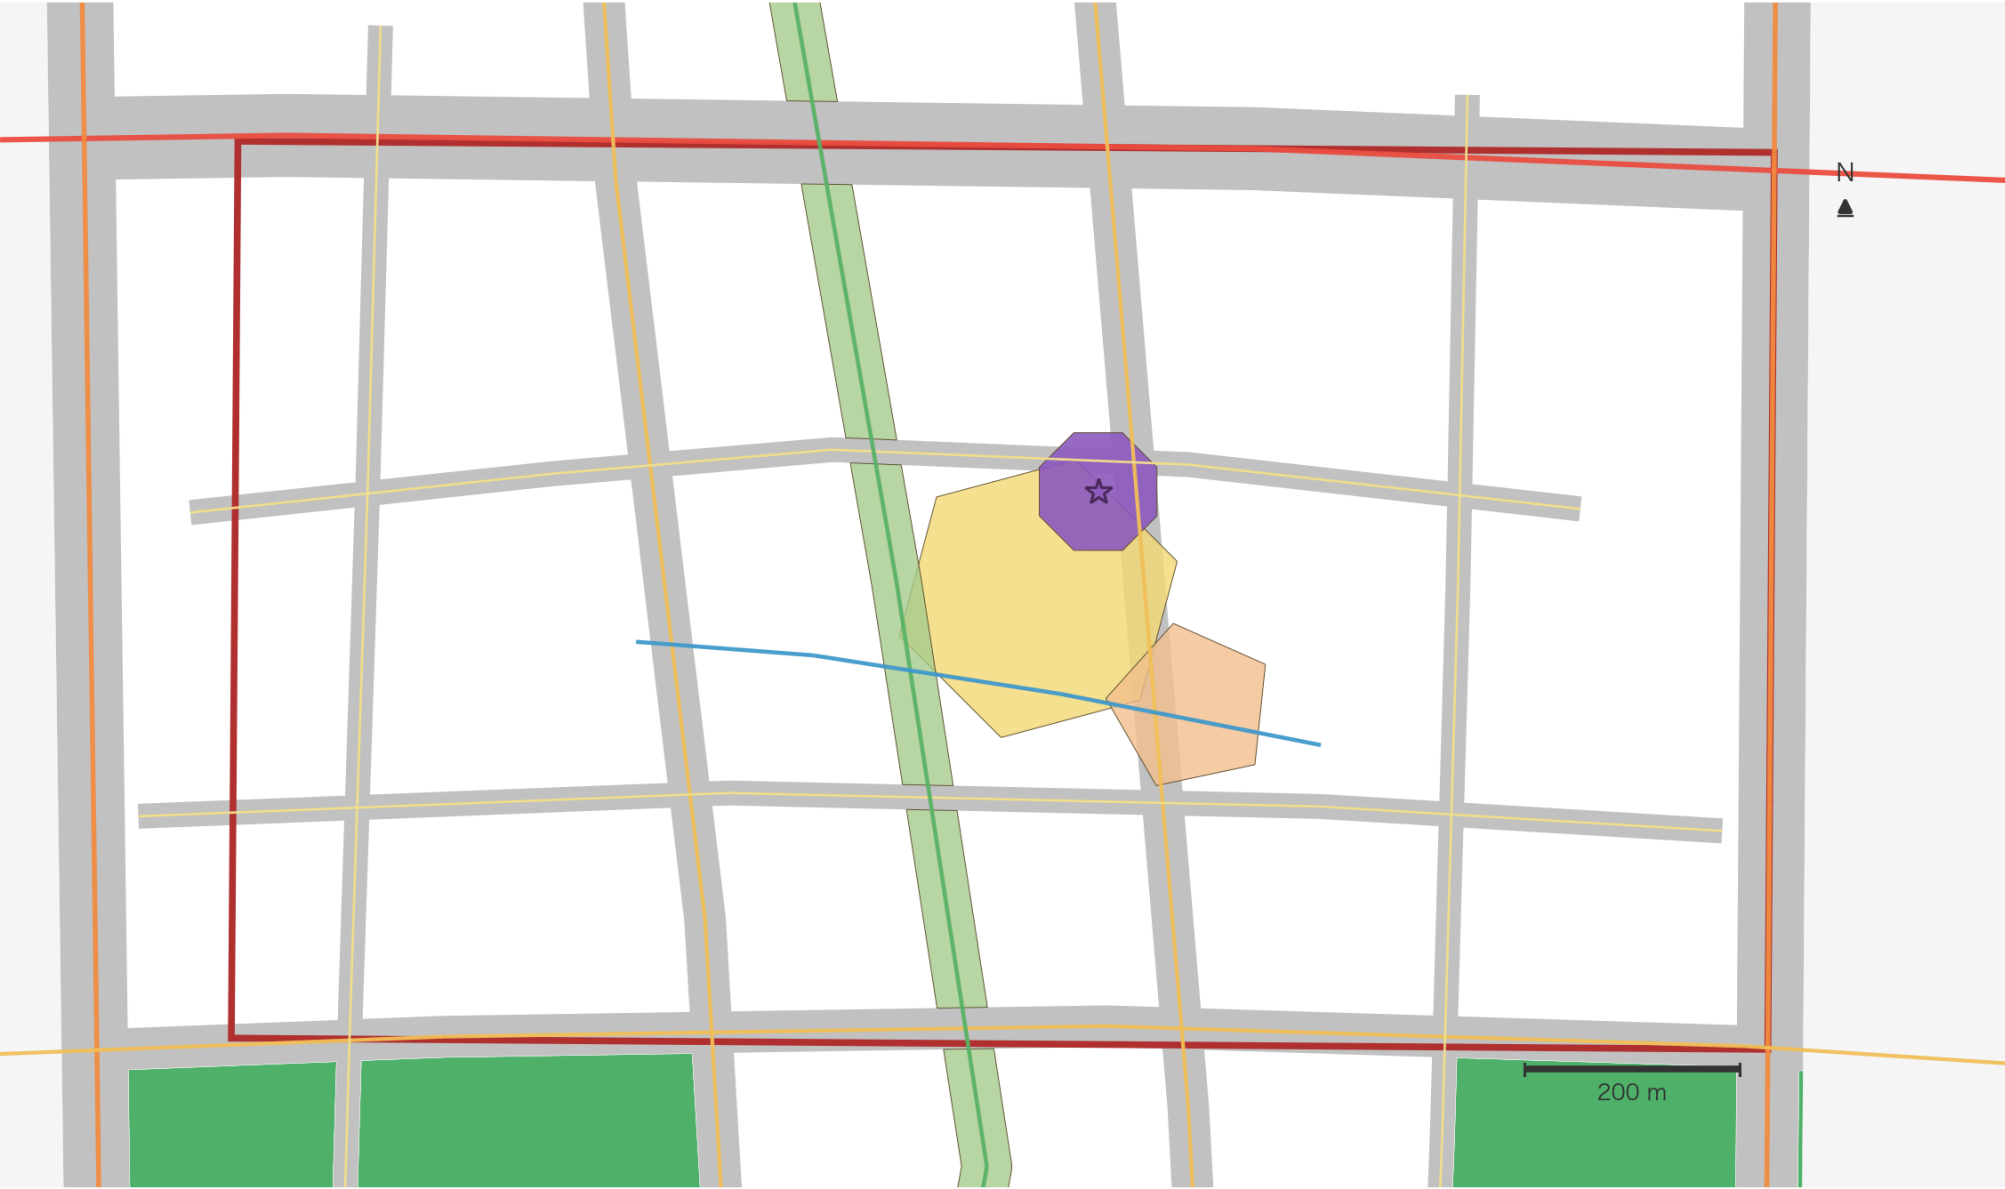

08 约束条件图

遗产保护范围 + 控高分区 + 铁路与水系

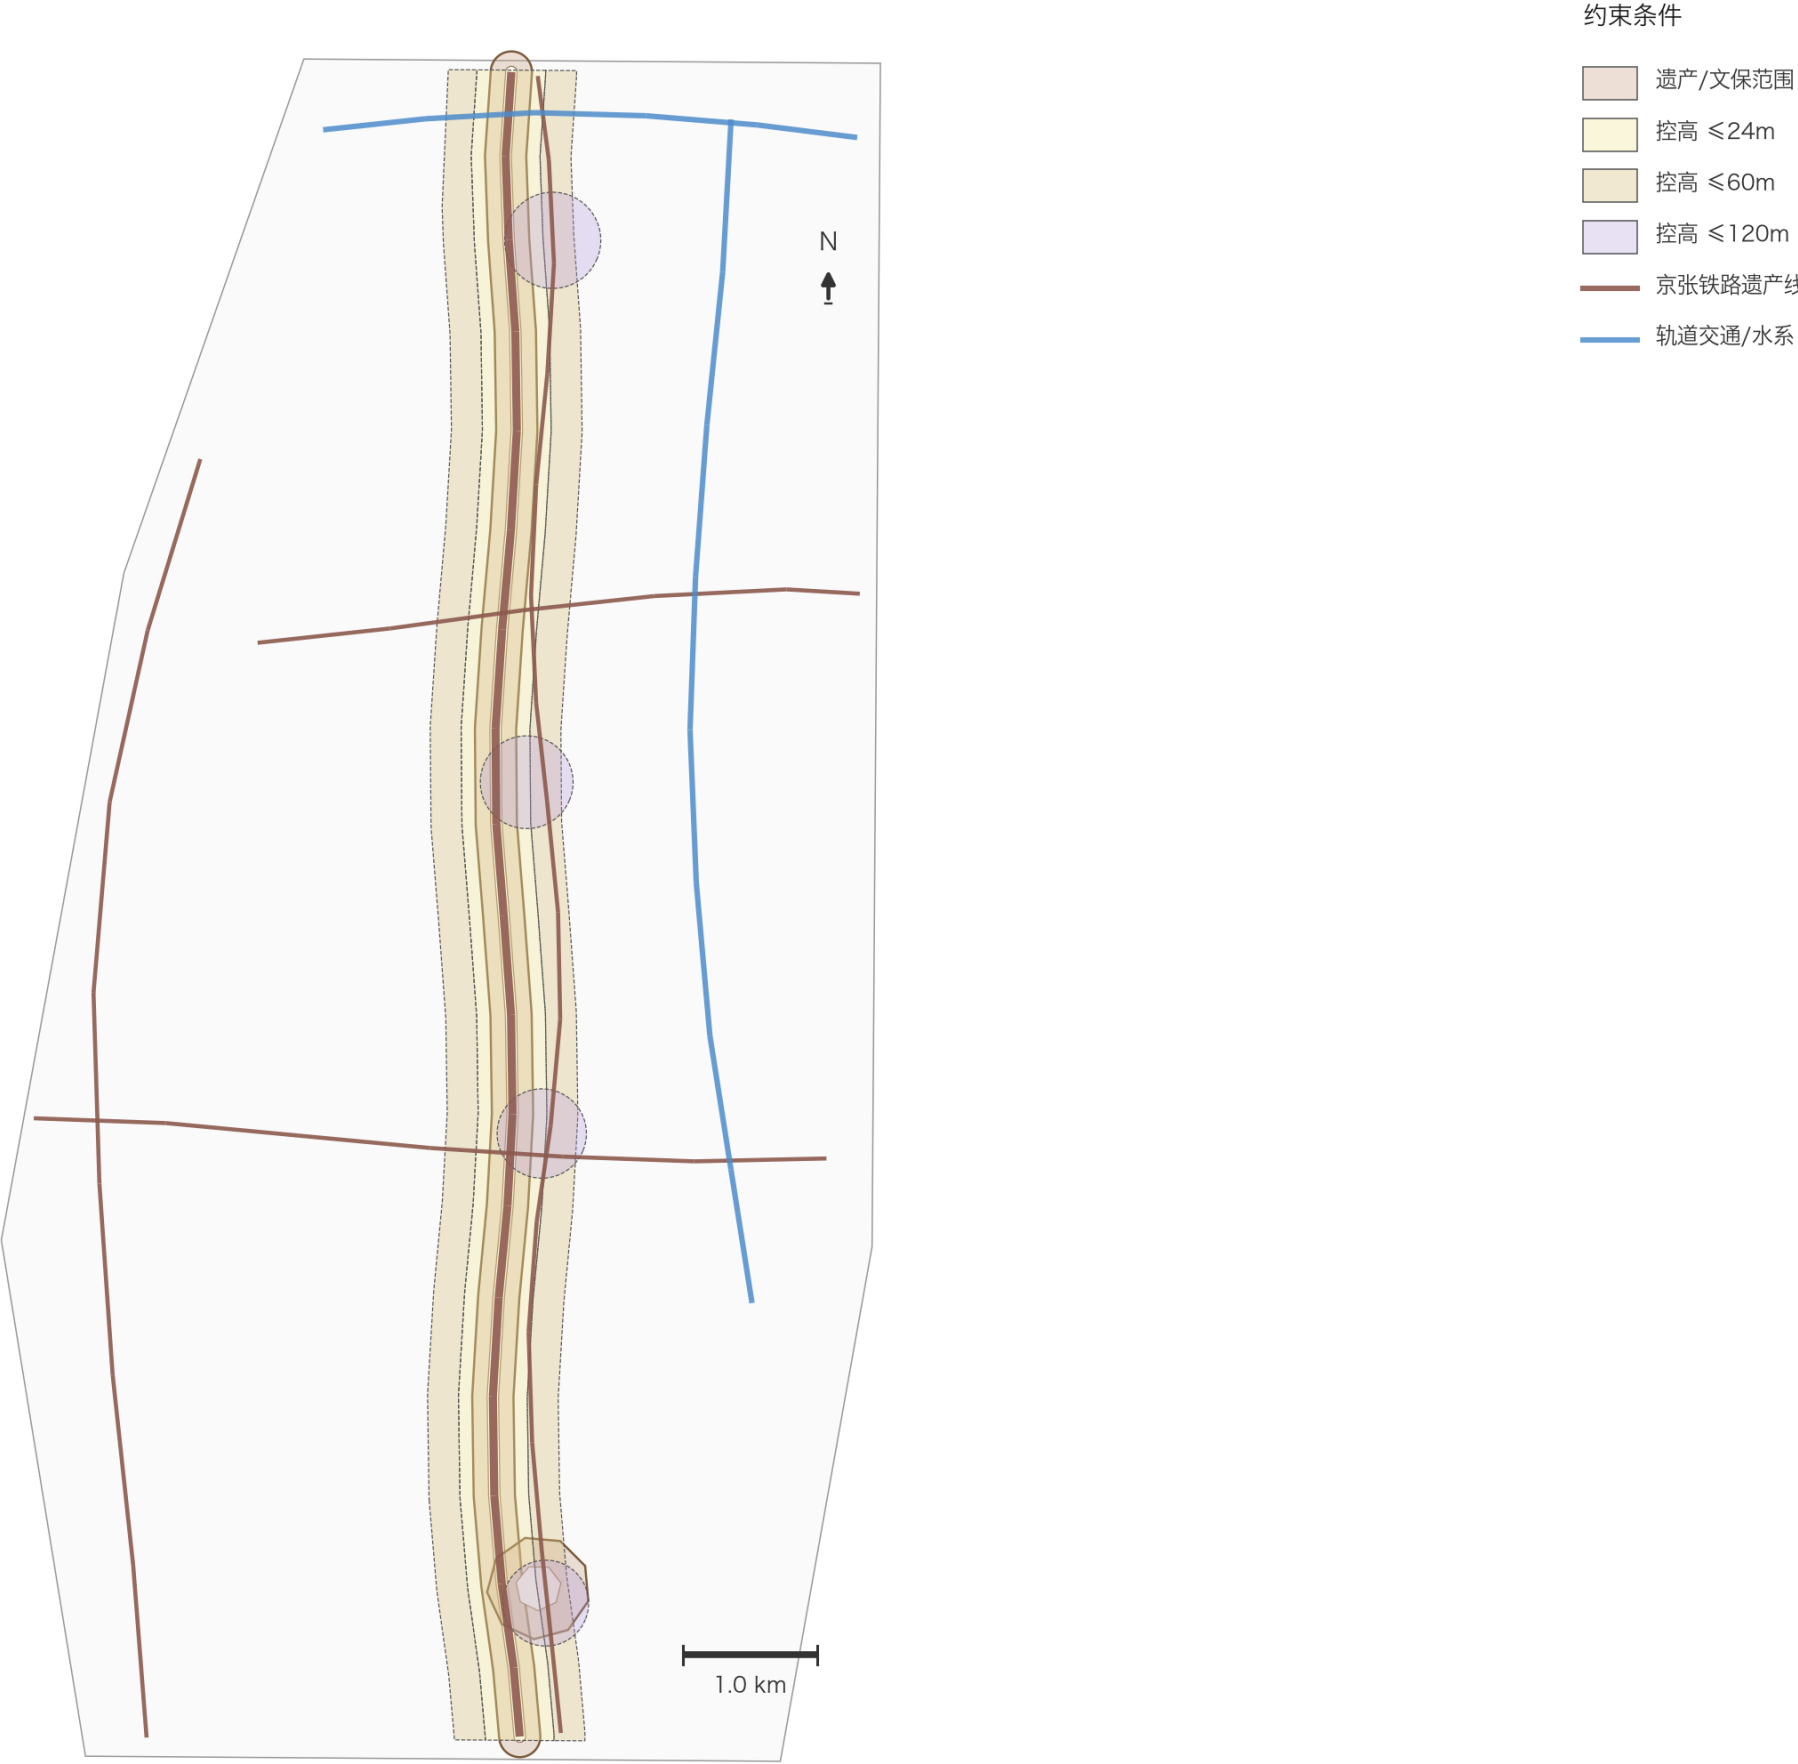

指标汇总页

所有数值均由 pyproj.Geod 反算，坐标系 WGS84；投影 EPSG:32650 仅用于图形绘制。

三层范围

ID	名称	面积(km2)	计算方法	来源
PROV-KEY-001	众智园AI自主创新加速区粗略范围	1.9291	Geod.geometry_area_perimeter	key_areas.geojson
PROV-KEY-002	北京AI原点社区粗略范围	1.0432	Geod.geometry_area_perimeter	key_areas.geojson
PROV-KEY-003	大钟寺AI产业聚集区粗略范围	0.7204	Geod.geometry_area_perimeter	key_areas.geojson
PROV-RESEARCH-001	统筹研究范围粗略替代边界	43.6058	Geod.geometry_area_perimeter	site_boundary.geojson
PROV-SITE-001	总体设计范围粗略替代边界	11.4120	Geod.geometry_area_perimeter	site_boundary.geojson

土地利用（前10）

代码	名称	面积(ha)	占比	来源
1207	城镇村道路用地	104.28	9.1%	land_use.geojson
1207	城镇村道路用地	90.01	7.9%	land_use.geojson
1207	城镇村道路用地	55.94	4.9%	land_use.geojson
1401	公园绿地	47.10	4.1%	land_use.geojson
1401	公园绿地	44.00	3.9%	land_use.geojson
0802	科研用地	25.36	2.2%	land_use.geojson
0805	体育用地	24.48	2.1%	land_use.geojson
0802	科研用地	24.35	2.1%	land_use.geojson
0701	城镇住宅用地	23.23	2.0%	land_use.geojson
0701	城镇住宅用地	21.23	1.9%	land_use.geojson

道路分级

等级	长度(km)	占比	计算方法	来源
arterial	41.15	31.1%	Geod.line_length	roads.geojson
secondary	35.36	26.7%	Geod.line_length	roads.geojson
greenway	20.07	15.2%	Geod.line_length	roads.geojson
branch	15.50	11.7%	Geod.line_length	roads.geojson
expressway	11.67	8.8%	Geod.line_length	roads.geojson
pedestrian	7.20	5.4%	Geod.line_length	roads.geojson
transit_connection	1.52	1.1%	Geod.line_length	roads.geojson

绿地总面积: 284.7 ha | 公共空间总面积: 73.2 ha

建筑总数: 89 个

道路总长度: 132.48 km