


跨项目完整旅程共同交付

正式竞赛图册

项目完成，不等于人的完整旅程完成

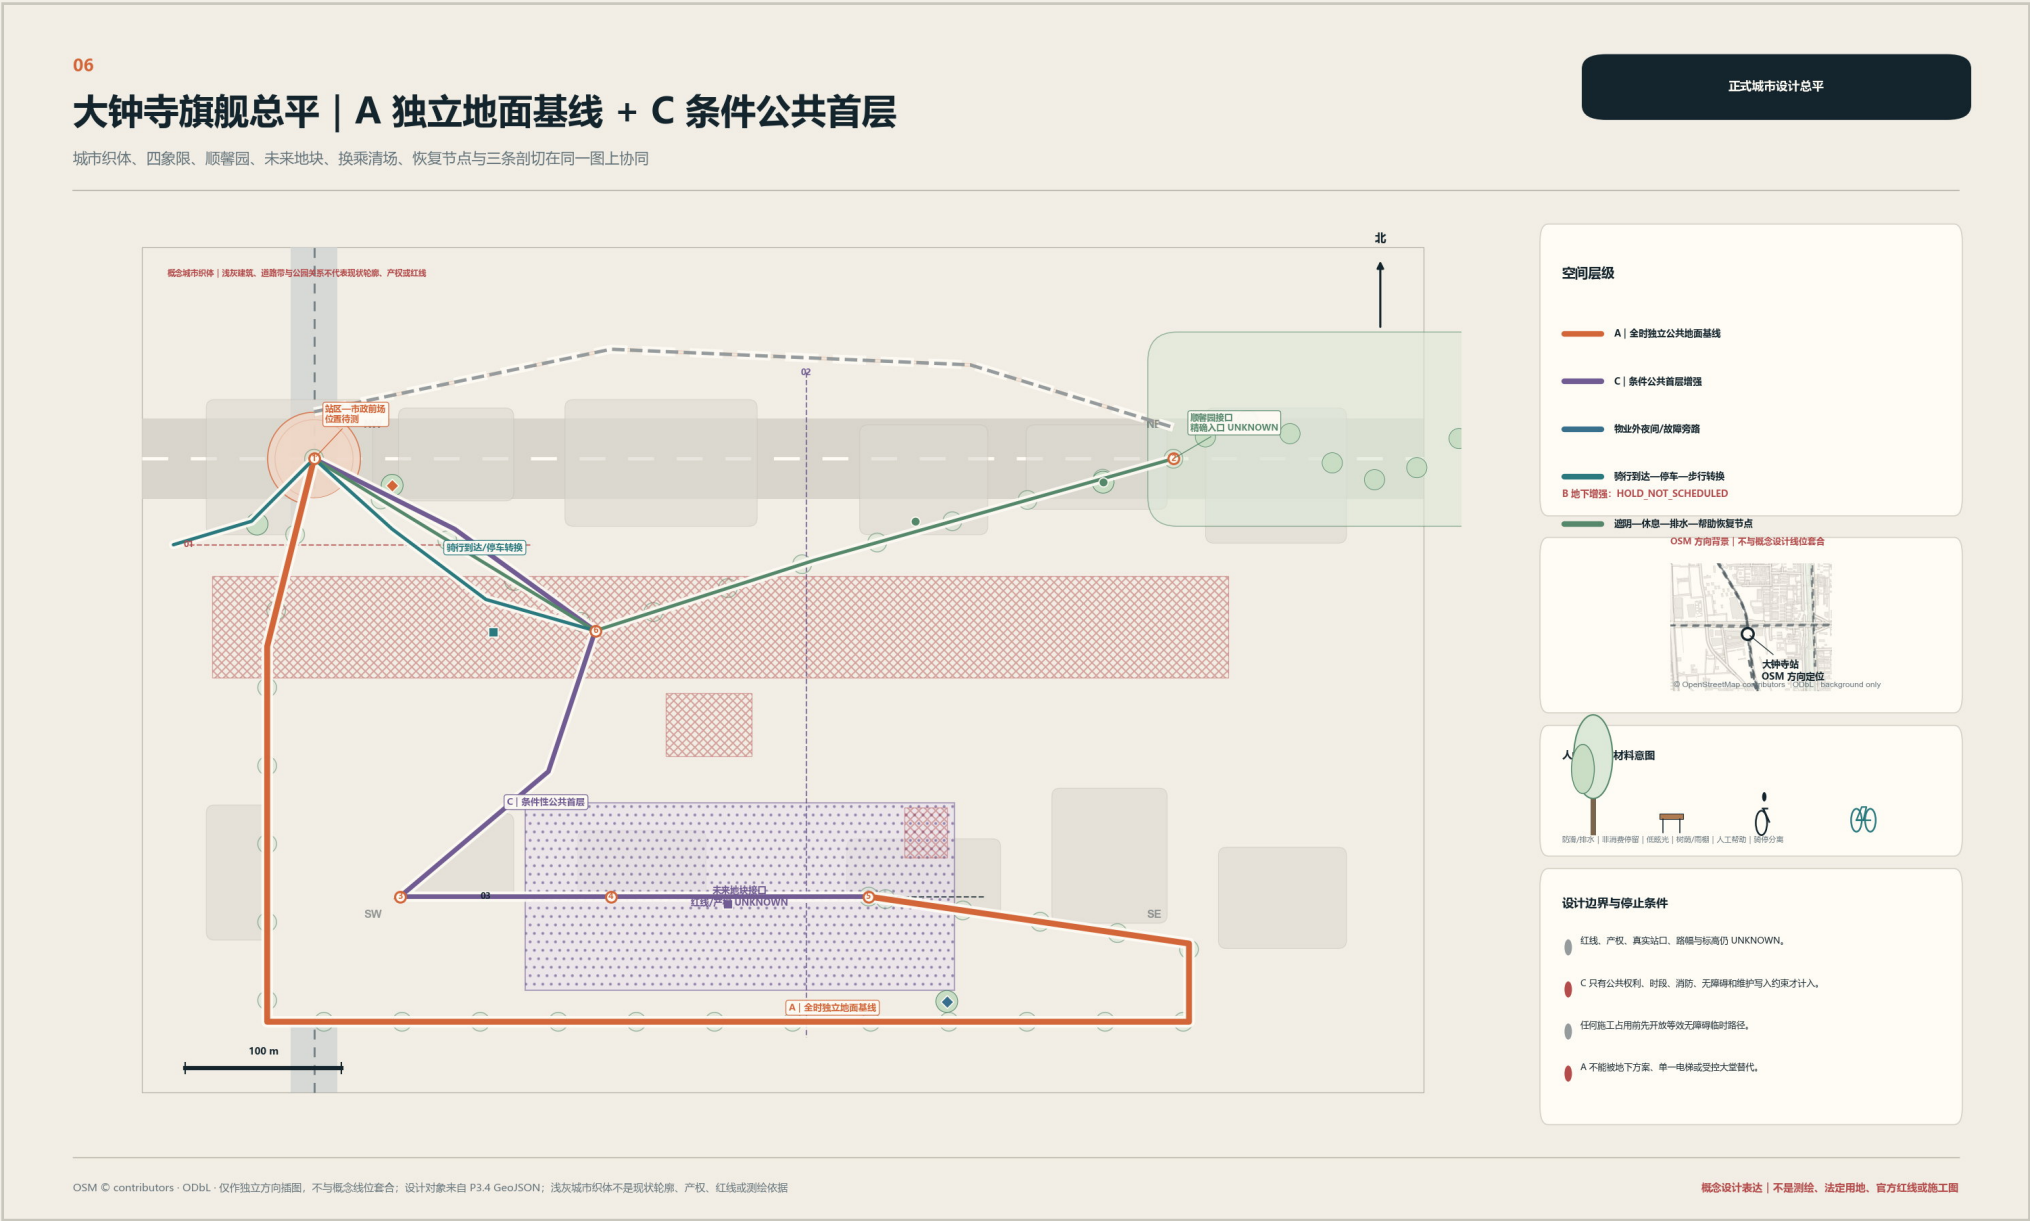

评委阅读路径 | 30 秒、3 分钟、10 分钟

百年京张 AI 创新带城市设计 | 以人的端到端公共空间为跨项目共同交付单元

 30 秒

项目完成 ≠ Journey 完成
跨项目空间接口
大钟寺 A+C

 3 分钟

三区不同处理
坏条件下仍可用
AI 只发现与复审

 10 分钟

尺度、边界、法规、分期
责任与维护
UNKNOWN、证据、双语、权利

大钟寺

旗舰深化 | A+C / B HOLD

清河—众智园

接住端点 | QH-A01

AI 原点


保留重审 | No major intervention

official SITE_BOUNDARY / KEY_AREA 缺失；精确位置、权属和现场性能继续 UNKNOWN

01

项目建成，不等于人的完整旅程建成

三层范围、三重点区与跨项目状态链 | 第一眼看空间，第二眼看 Journey

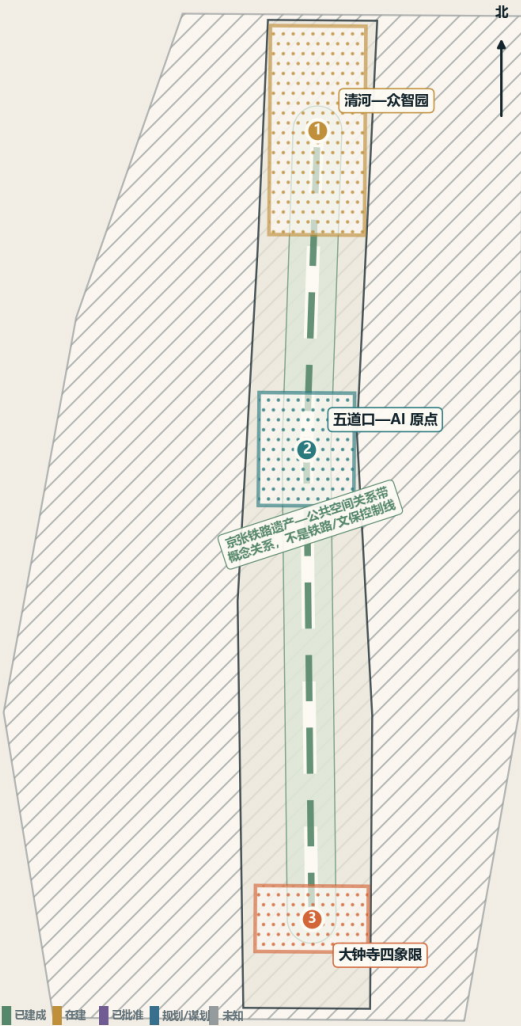

来源：design_briefjson; provisional_boundaries.geojson; Phase 2 官方工程状态台账（本次审计基线 2026-08-13）

正式城市设计图

三层范围 | 尺度事实与空间边界分开

43.6 km²

11.4 km²

3

统筹研究范围（公告面积）

总体设计范围（公告面积）

重点详细设计区（官方数量）

面积为官方发布事实；图示 polygon 仍为 provisional_rough，不是官方红线。

01 清河—众智园

站区端点 → 在建项目 → 市政/蓝绿 → 更新组团 → 物业/建筑



Built 仅证明项目状态；端到端可用性仍需现场与共同验收。

02 五道口—AI 原点

既有链 + 已批邻近项目；直接 OD 剩余问题仍需交付后重审



Built 仅证明项目状态；端到端可用性仍需现场与共同验收。

03 大钟寺四象限

站点 → 北三环 → 顺著园 → 更新地块 → 共享首层/目标象限



Built 仅证明项目状态；端到端可用性仍需现场与共同验收。

概念设计表达 | 不是测绘、法定用地、官方红线或施工图

为什么

按证据精度分三层

空间在哪里

43.6 / 11.4 km² + 三重点区

证据


官方任务书、Skill、site package

仍不知道

official polygons 与现场测绘

为什么单个项目完成仍可能丢失完整 Journey

Evidence → Journey → Interface failure → Spatial intervention → Re-audit

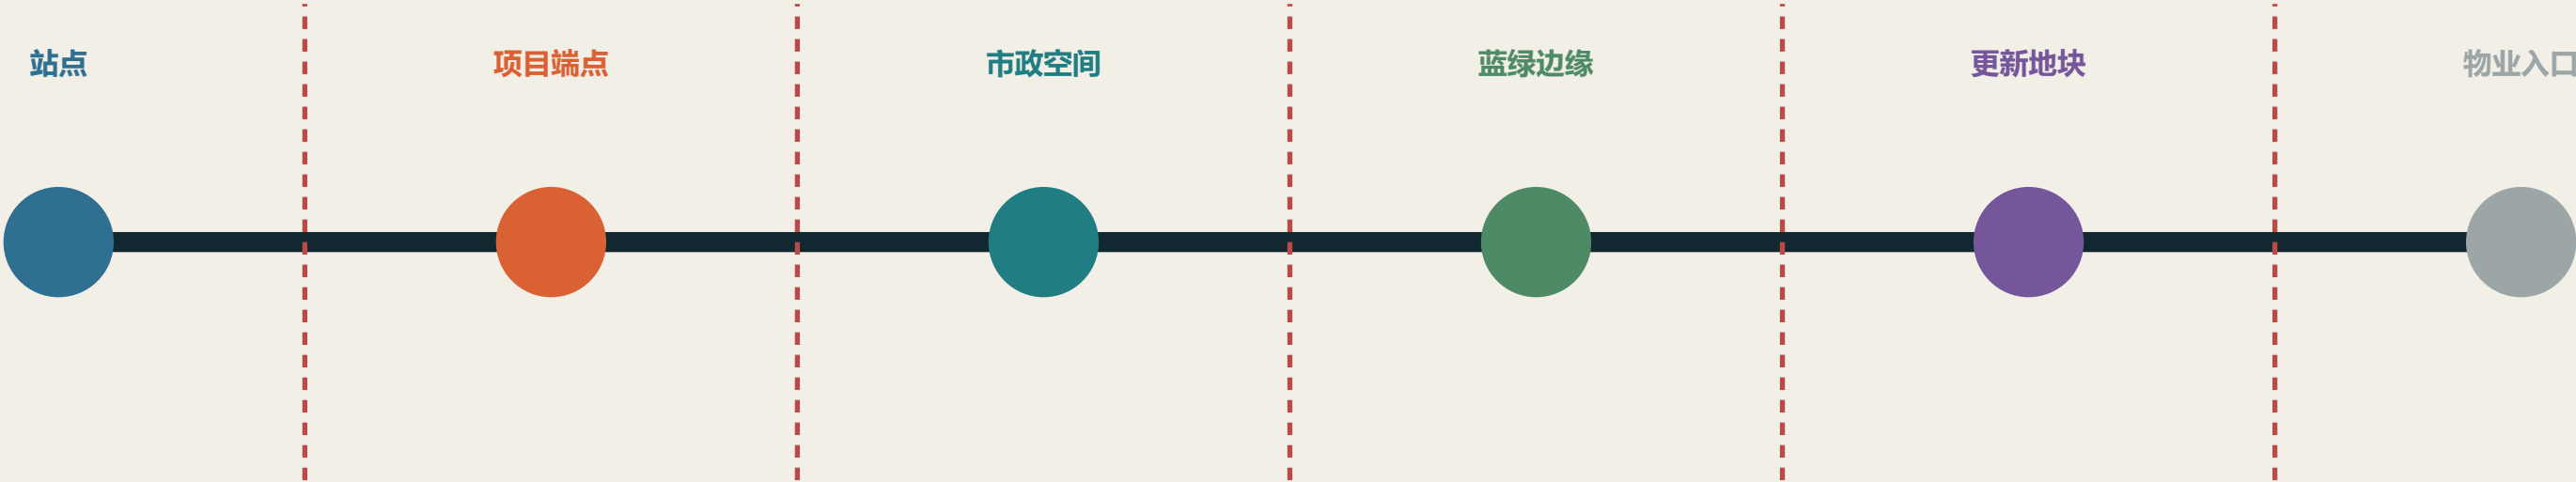

每条红色虚线都是一次项目责任换手：红线、工期、开放时段、产权或维护边界都可能在这里切断人的端到端 Journey。

43.6 km² 协同研究 + 约 11.4 km² 总体设计

正式图册

CONCEPTUAL DESIGN STRUCTURE / NOT STATUTORY LAND USE

02


概念城市设计结构 | 不是法定用地

遗产公共空间、创新研发、社区生活、公共服务、交通与蓝绿恢复共同组织 11.4 km²

正式城市设计图

三种城市织体 | 同一协议，不同空间形态


大钟寺 | 四象限 + A/C 双层公共性

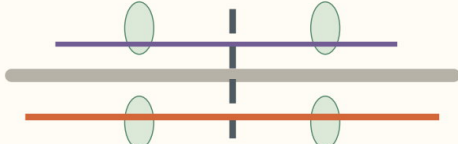

清河—众智园 | 六次空间换手



AI 原点 | 保留 + 重审 + 证据触发

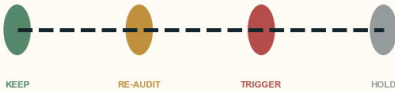

CONCEPTUAL DESIGN STRUCTURE | NOT STATUTORY LAND USE
现状土地用途、权属、控规图斑与开发强度仍需官方资料/专业复核。

来源: geometry/land_use.geojson, key_areas.geojson, public_space.geojson, green_space.geojson; 关系带由三重质心派生, 仅作概念结构

概念设计表达 | 不是测绘、法定用地、官方红线或施工图

为什么

总体层先组织公共关系

空间在哪里

轨道到达门 + 公共地面网 + 蓝绿恢复

证据


概念 GeoJSON 与可复算指标

仍不知道

控规、红线、FAR、高度和现状测绘

慢行、接驳与蓝绿恢复 | 在雨、夜与故障中仍可用

A public ground baseline survives rain, night, closure and equipment failure

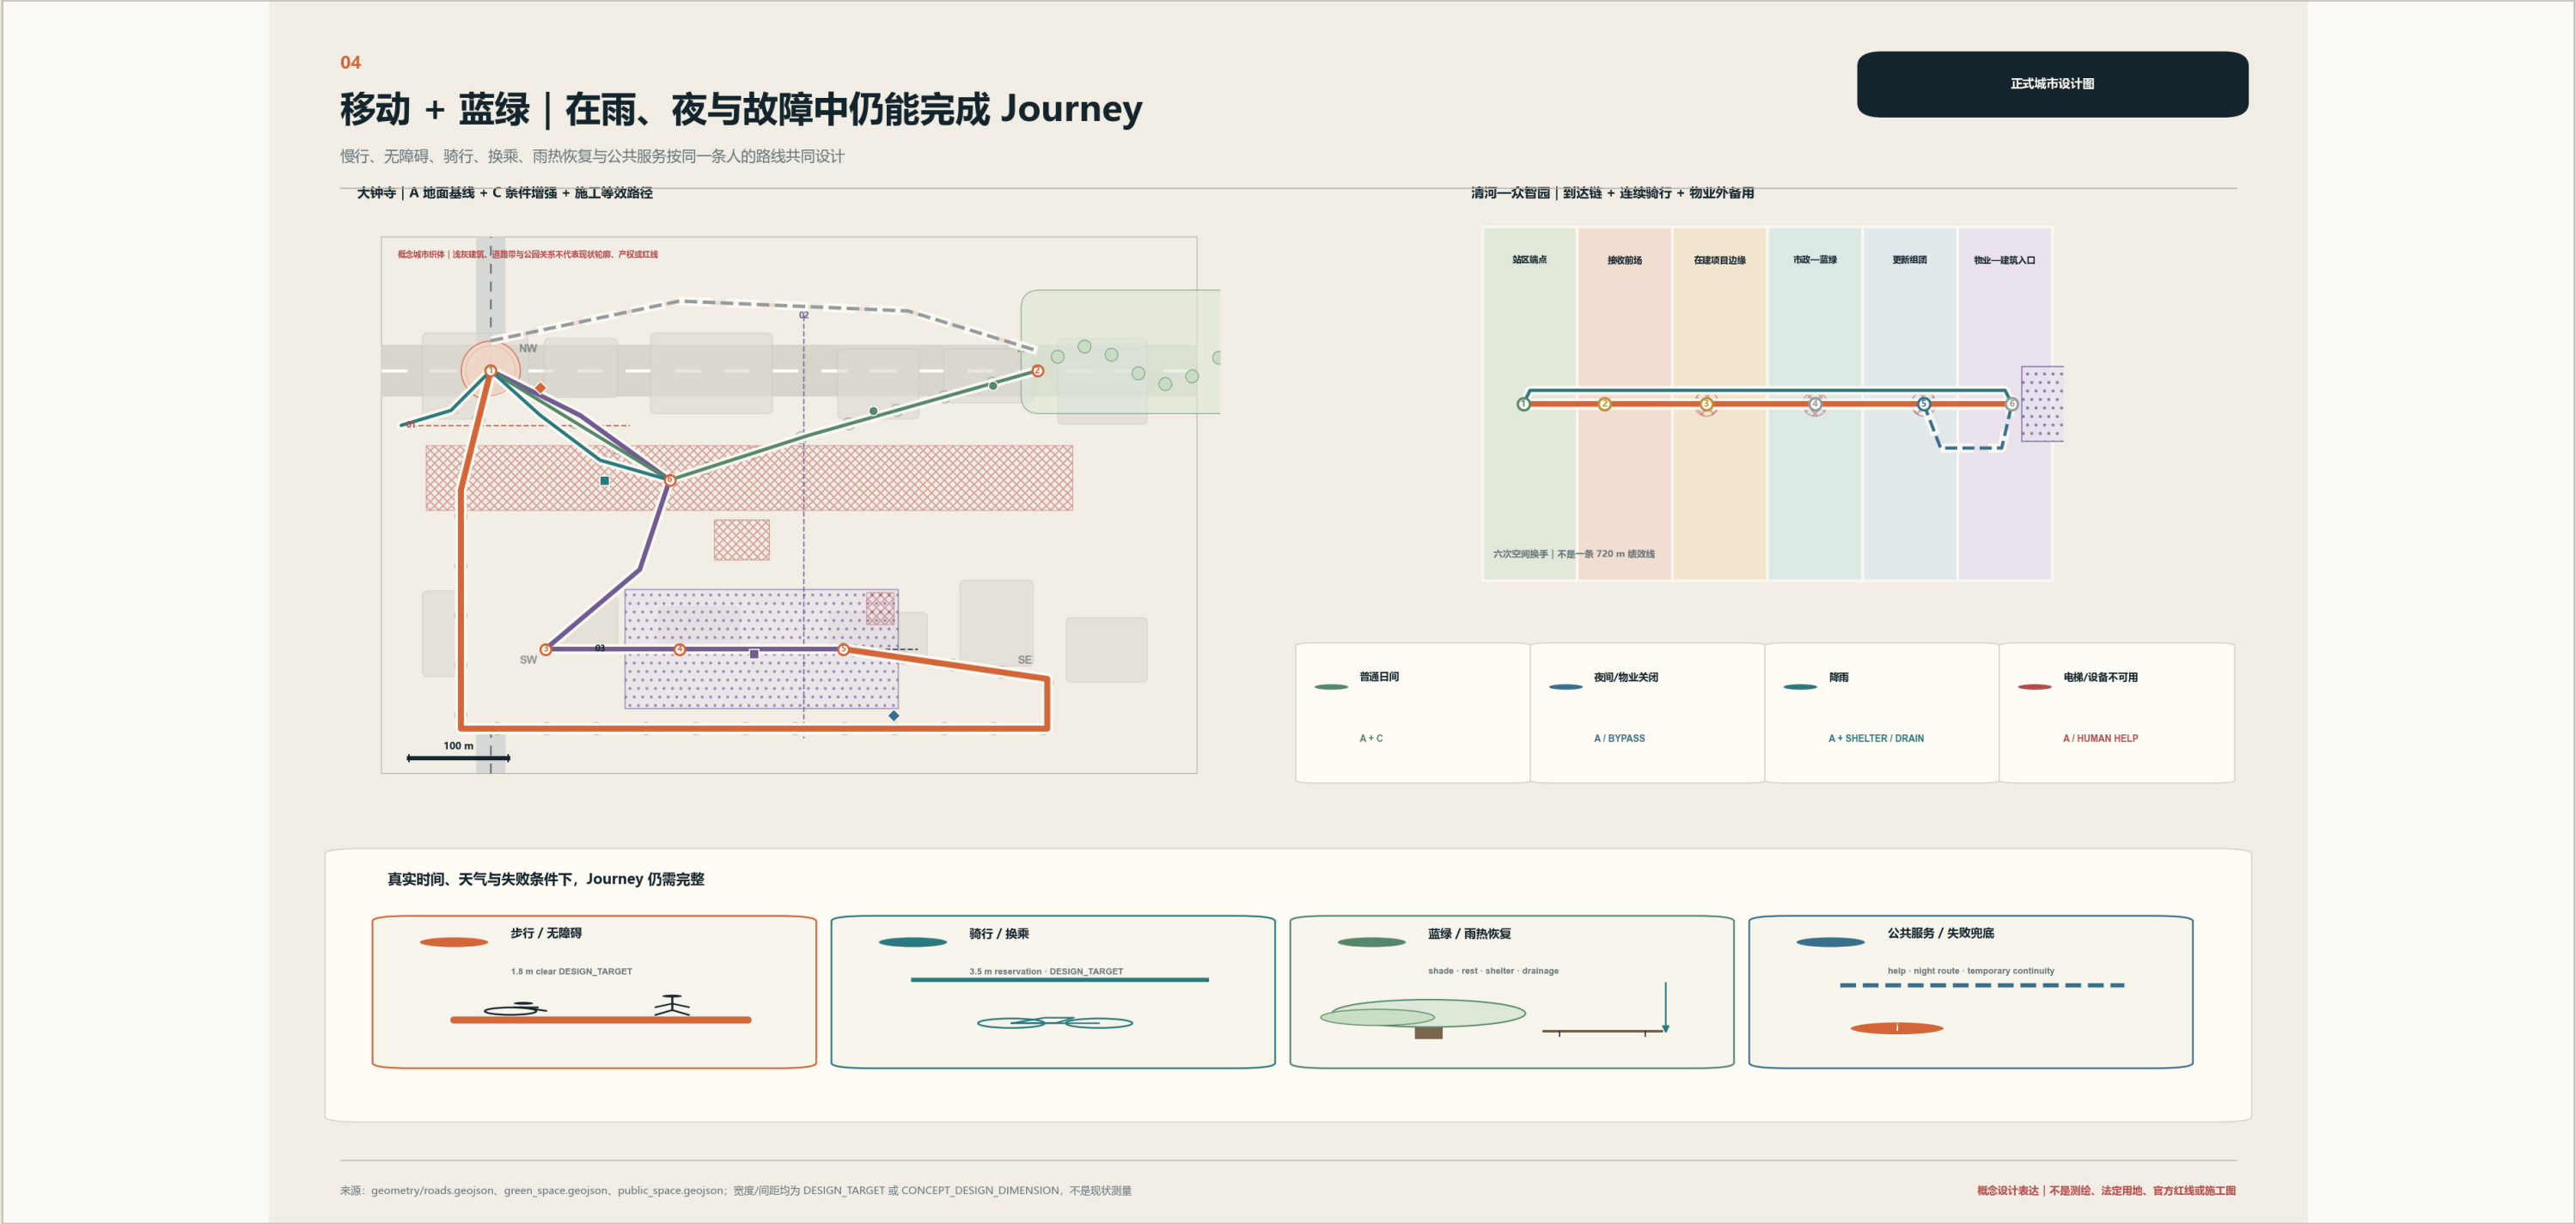

三重点区 | 不是同一模板的三个复制品


Dazhongsi A+C | Qinghe six handovers | AI Origin preserve + re-audit

03

三重点区 | 三种不同的详细设计判断


大钟寺：A+C 旗舰 | 清河：六次空间换手 | AI 原点：保留、重审、证据触发

A | 大钟寺旗舰：四象限公共空间 + 独立地面基线 A + 条件公共首层 C

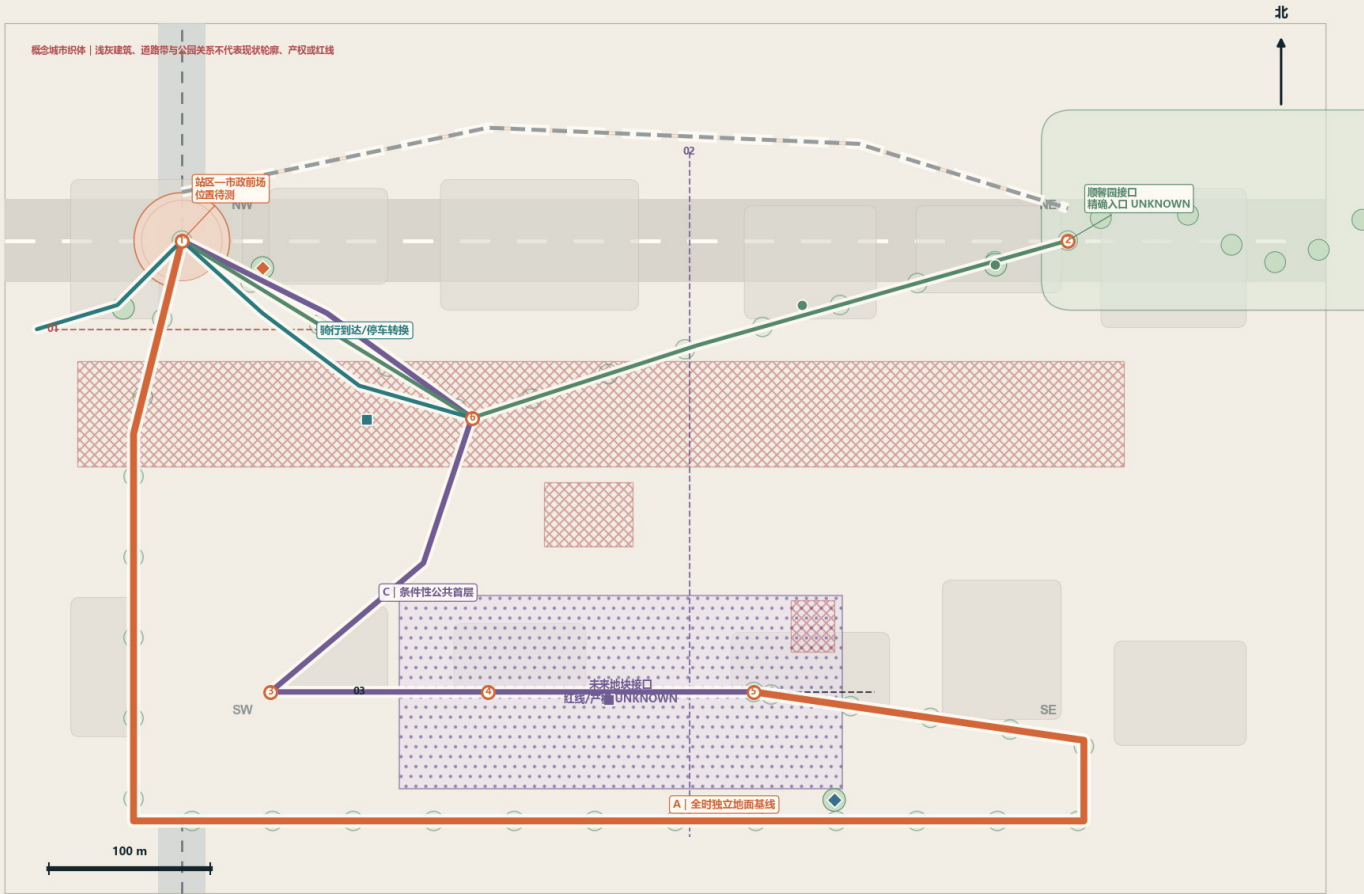


来源：P3.4 同源 GeoJSON + metrics；大钟寺浅灰织体为概念表达，不是现状轮廓；所有重点区 polygon 均为 provisional_constraint

B | 清河一众智园：六次城市空间换手

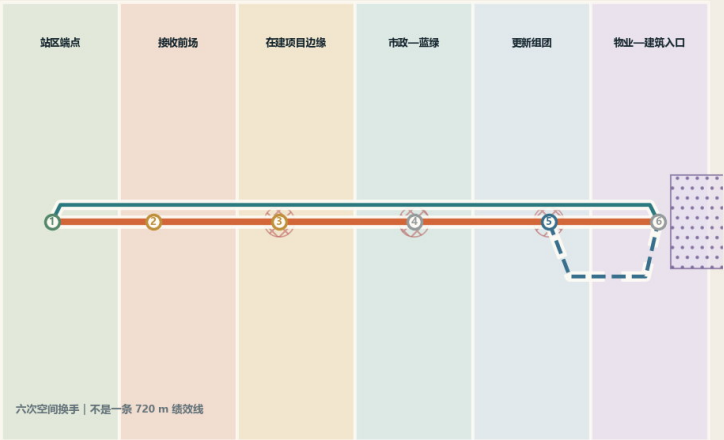

C | AI 原点：不新增重大工程的专业判断

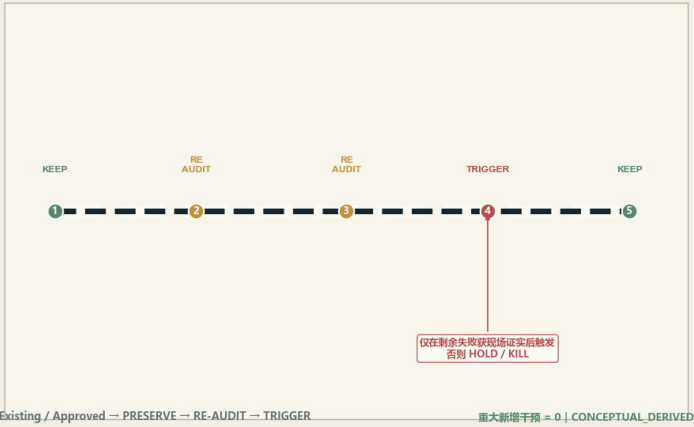

概念设计表达 | 不是测绘、法定用地、官方红线或施工图

为什么

工程状态不同，设计动作必须不同

空间在哪里

三处 provisional 重点区

证据

BUILT / APPROVED / PLANNED / UNKNOWN 链

仍不知道

official key-area polygons 与现场性能


大钟寺旗舰总平 | 四象限地面基线与条件增强

FLAGSHIP | A independent ground + C conditional ground floor | B HOLD

06

大钟寺旗舰总平 | A 独立地面基线 + C 条件公共首层

城市织体、四象限、顺馨园、未来地块、换乘清场、恢复节点与三条剖切在同一图上协同

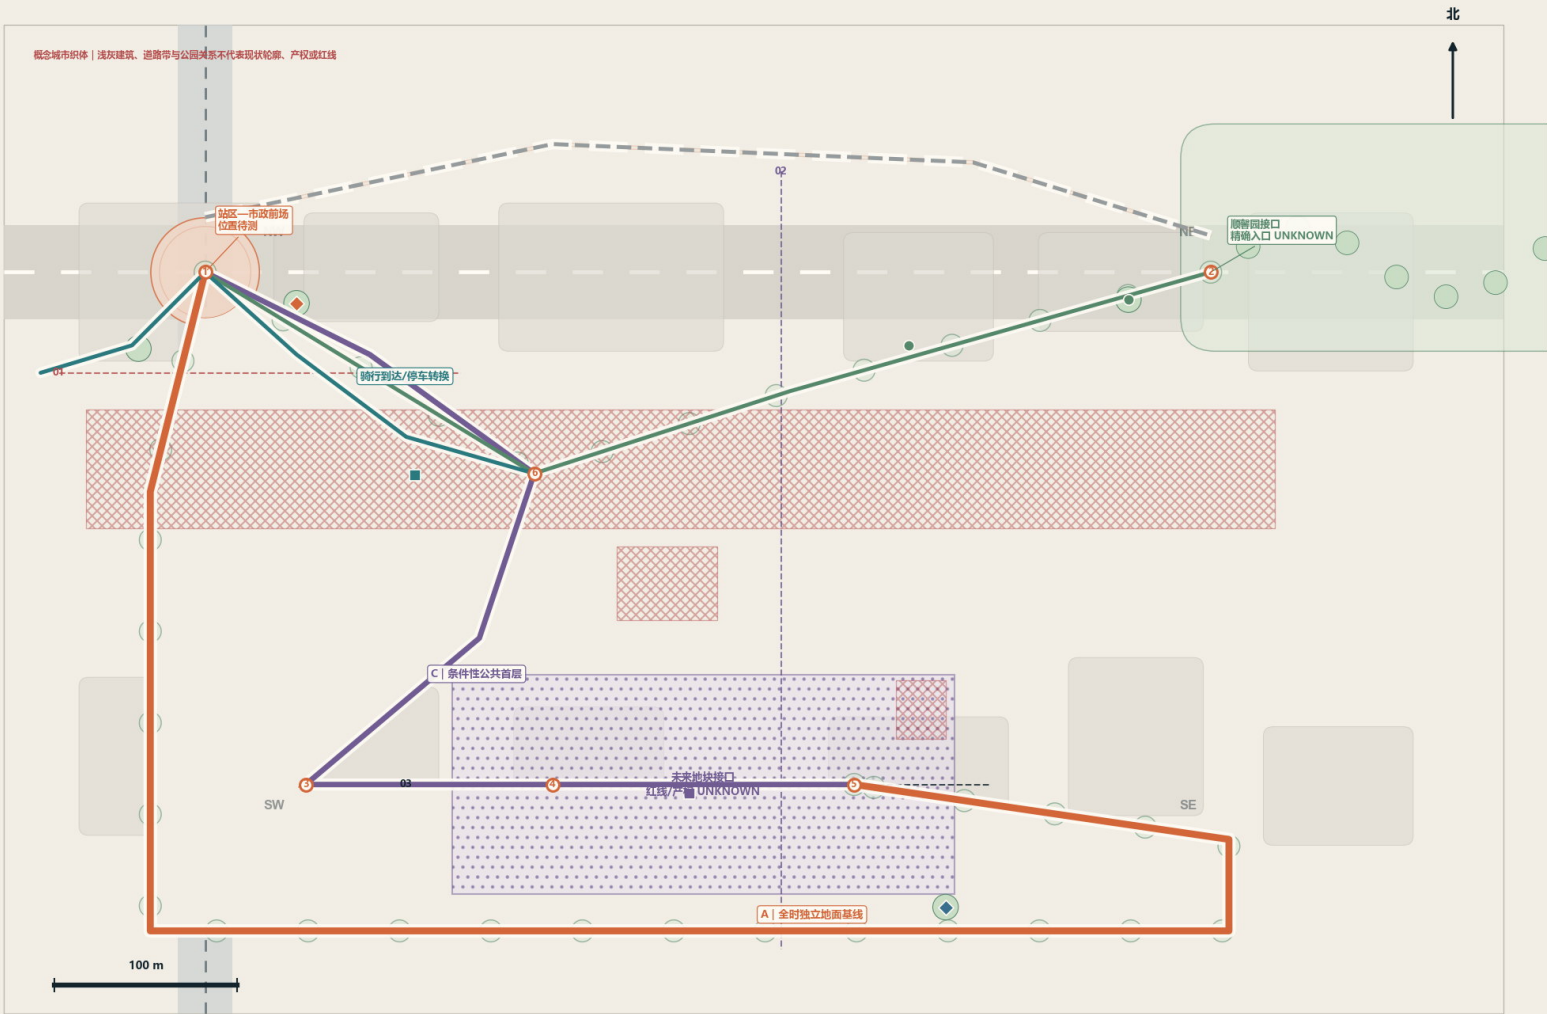

正式城市设计总平

空间层级

- A | 全时独立公共地面基线
- C | 条件公共首层增强
- 物业外夜间/故障旁路
- 骑行到达—停车—步行转换
- B 地下增强: HOLD_NOT_SCHEDULED
- 道路—休息—排水—帮助恢复节点

OSM 方向背景 | 不与概念设计线位套合



设计边界与停止条件

- 红线、产权、真实站口、路幅与标高仍 UNKNOWN.
- C 只有公共权利、时段、消防、无障碍和维护写入约束才计入。
- 任何施工占用前开放等效无障碍临时路径。
- A 不能被地下方案、单一电梯或受控大堂替代。

OSM © contributors · ODbL · 仅作独立方向插图，不与概念线位套合；设计对象来自 P3.4 GeoJSON；浅灰城市织体不是现状轮廓、产权、红线或测绘依据

概念设计表达 | 不是测绘、法定用地、官方红线或施工图

为什么

四象限不靠一个地标统一

空间在哪里

站口—市政—公园—未来地块

证据


六接口、A/C、三断面和停止条件

仍不知道

精确站口、红线、权属与竣工状态

大钟寺六接口 | 每次换手都有空间、责任与停止条件

A independent | C conditional | B HOLD_NOT_SCHEDULED

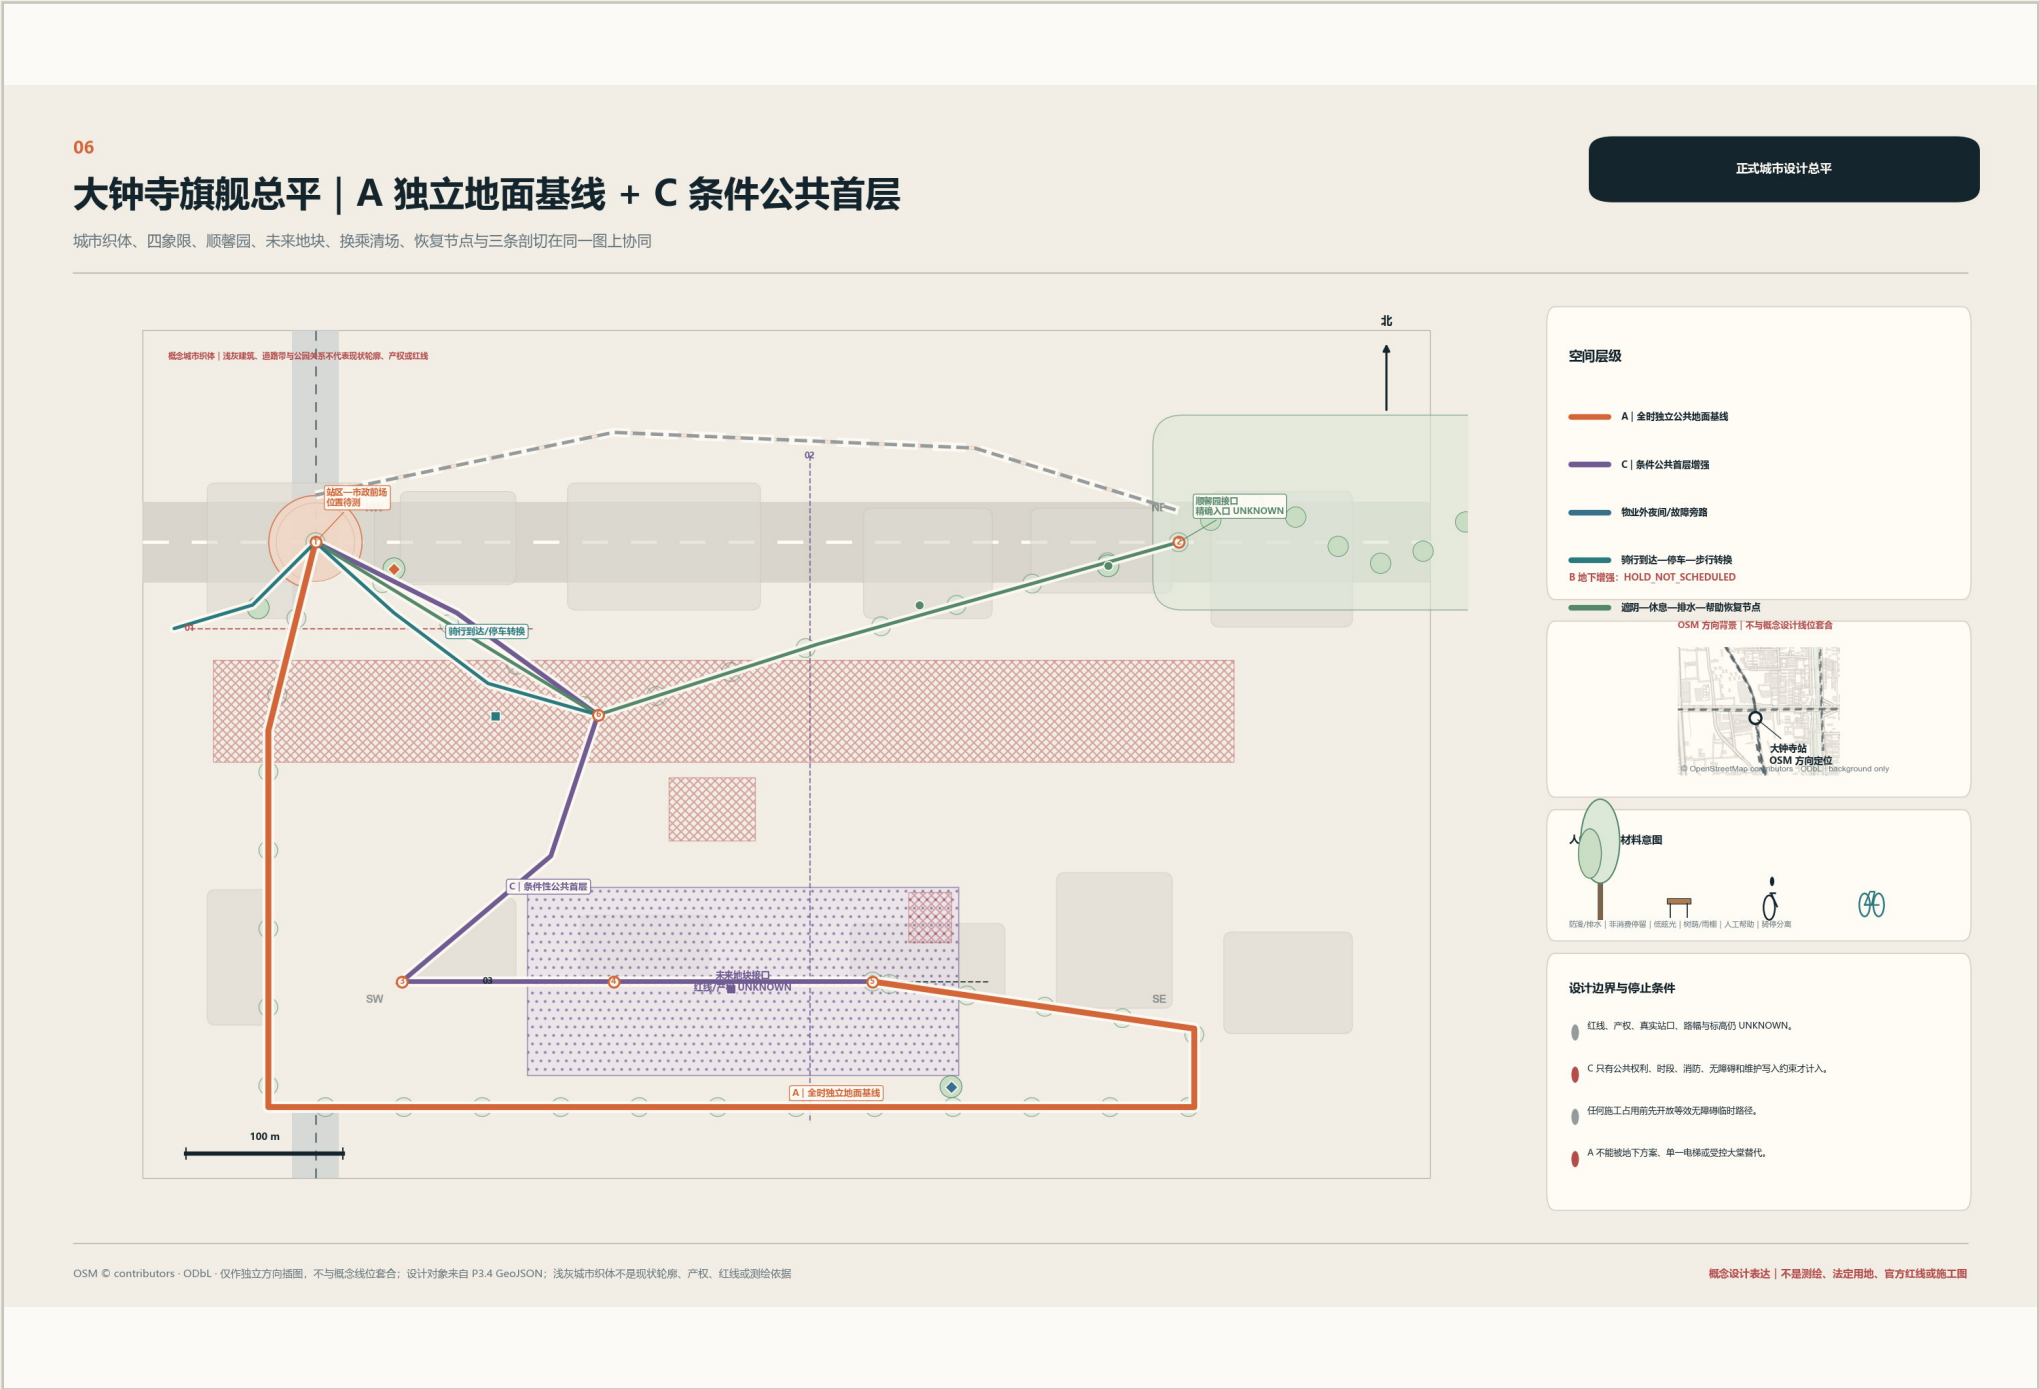

01 站口 → 市政前场

站区/市政共同接收

02 换乘清场

多模式不侵占净线

03 道路 → 顺馨园

遮阳、休息、排水、帮助

04 公园 → 未来地块

A 在物业外独立连续

05 地块边 → 公共首层 C

权利/消防/无障碍/维护门

06 施工/关闭/故障

等价临时路与夜间旁路

FIELD + PROFESSIONAL + APPROVAL UNKNOWN

07A

剖面 01 | 站区换乘清场：步行、轮椅、骑行、接送互不侵占

规范依据给出最低/目标语义；真实路幅、车道、站口、信号、客流与标高仍待测绘和专业复核

正式城市设计剖面



依据：GB 55019-2021 (1.8 m、2.4×7.0 m) + DB11/T 1116-2024 (站口 50 m 内 4.0 m 推荐、骑行连续性)；均需交通/无障碍/消防复核

概念设计表达 | 不是测绘、法定用地、官方红线或施工图

1.8 m 净线为设计目标，不是现状测量

4.0 m 包络待客流/交通/转弯轨迹复核

停车、接送、配送不得占用净线

FIELD + PROFESSIONAL + APPROVAL UNKNOWN


07B

剖面 02 | 顺馨园接口恢复：遮阴、避雨、停留、排水与帮助进入同一序列

保留已建公园，只补项目界面；树位、根系、入口、排水、照明与运维边界仍 UNKNOWN

正式城市设计剖面

现状 UNKNOWN 规范依据 设计目标 专业复核门

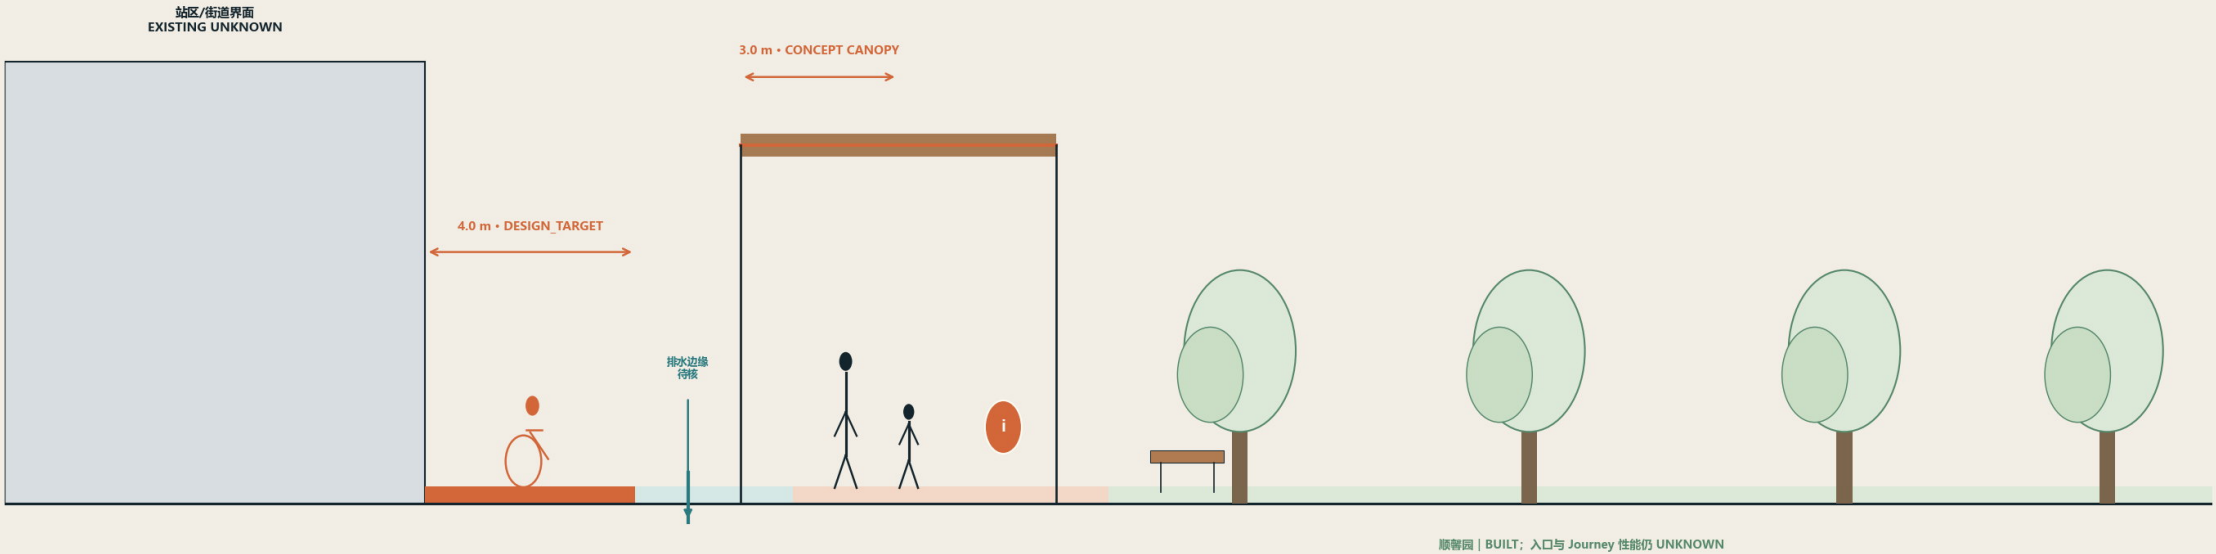

依据：顺馨园官方登记/开放信息 + GB 55019-2021 + 北京海绵城市地方标准；雨棚 3.0 m 与 50 m 恢复间距均为概念/设计目标，不是规范最低值

概念设计表达 | 不是测绘、法定用地、官方红线或施工图

入口净线先于新增设施

遮阴/避雨、座椅、排水与帮助不侵占通行

树根、排水、眩光或维护失败则缩减/取消

剖面 03 | 物业外 A + 条件性 C

正式图册


FIELD + PROFESSIONAL + APPROVAL UNKNOWN

07C

剖面 03 | 物业外 A + 条件 C：关闭、故障或审批失败时仍有公共地面路

C 是增强，不是主路线；公共权利、开放时段、消防、无障碍、结构与维护任何一项未闭合即退回 A

正式城市设计剖面

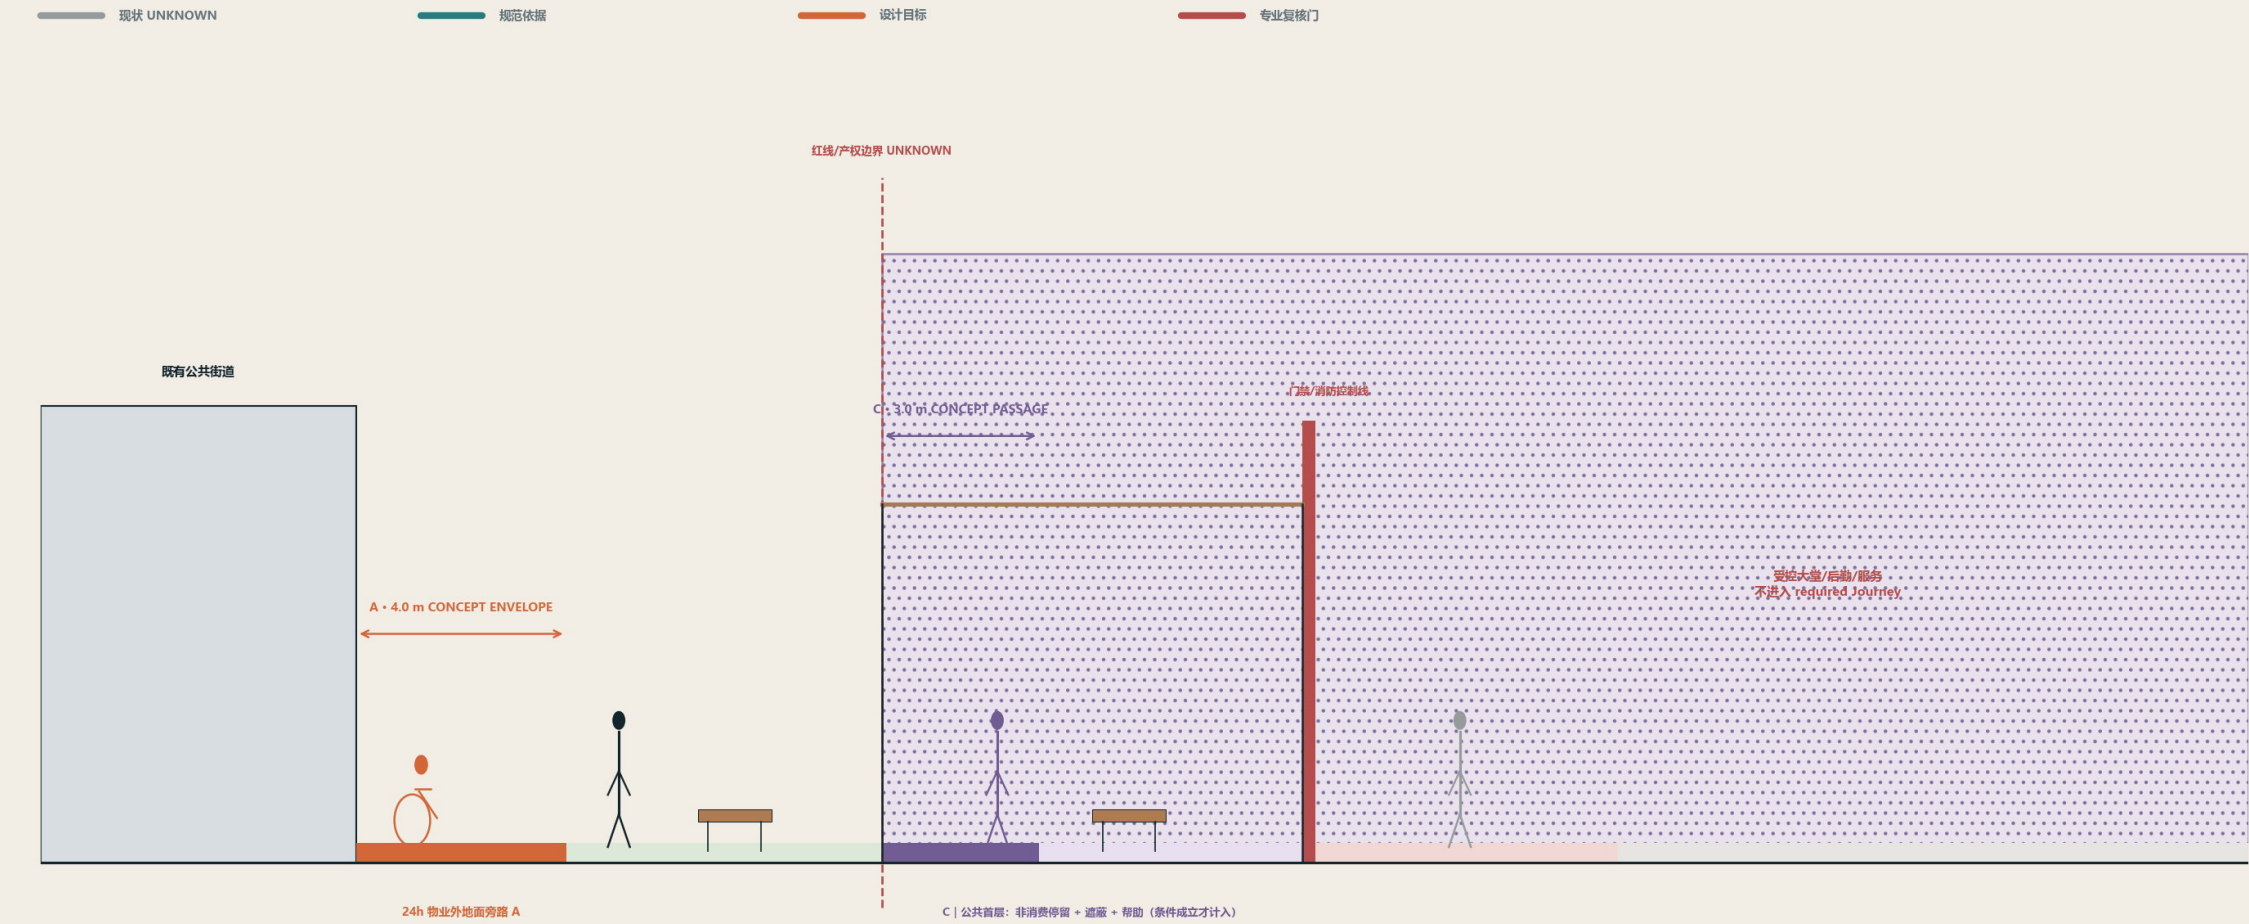

依据：GB 55019-2021 + 城市设计/控规/消防相关要求；本剖面不声明地块红线、层高、结构、消防分区、净高、桥隧或电梯可行性

概念设计表达 | 不是测绘、法定用地、官方红线或施工图

A 始终位于物业控制外

C 需要权利、时段、消防、无障碍与维护

C 关闭/电梯故障回到 A；B 继续 HOLD


概念体验图 | PRESENTATION_ONLY | 不是现场照片或批准效果图

08

人如何使用空间 | 日常、暴雨/设备不可用、夜间/物业关闭

同一概念空间、同一镜头：A 始终可用；C 只作条件增强；人的基本通行不依赖 AI、手机、单一电梯或营业时段

概念体验 | 非现场证据

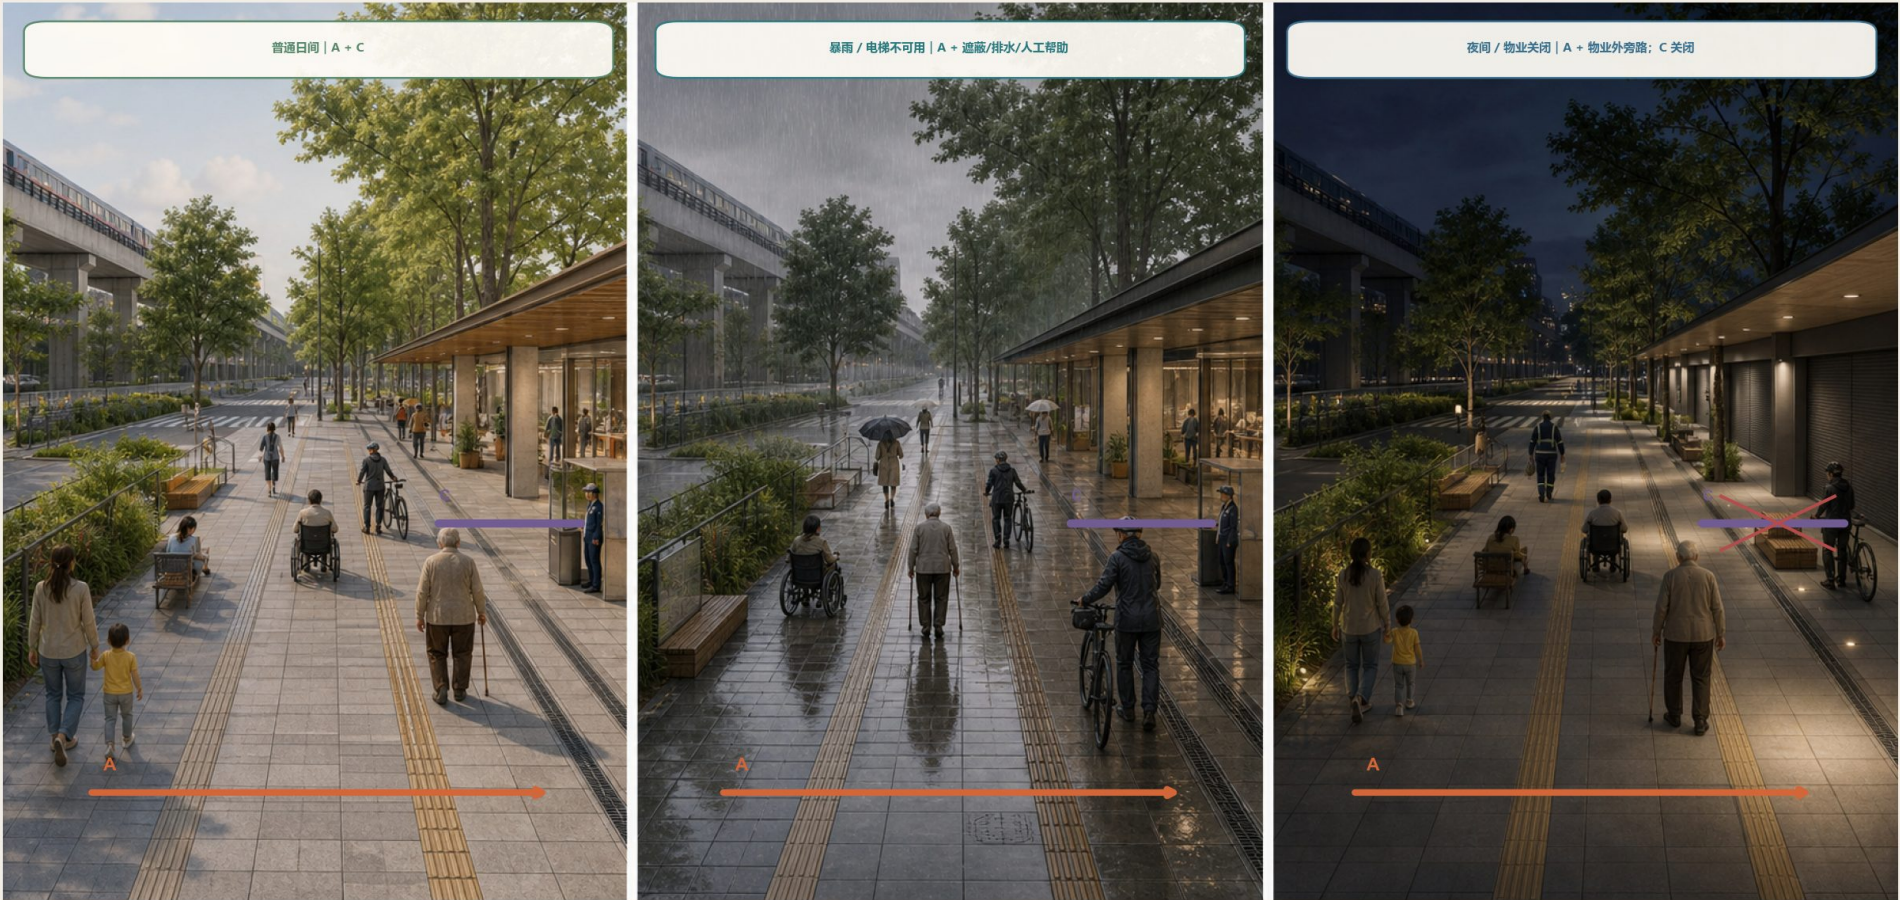

A | 全时、无台阶、物业外公共地面基线 C | 条件公共首层：遮蔽 + 非消费停留 + 帮助 雨热恢复：树荫/雨棚/排水/防滑 故障兜底：人工帮助 + 夜间旁路 + 骑行转换

AI 生成概念底图 (OpenAI built-in image generation, 2026-08-13) + 本地矢量标注；仅表达设计意图，不是现状照片、居民观察或获批工程效果图 概念设计表达 | 不是测绘、法定用地、官方红线或施工图

为什么

空间要在坏条件下仍服务人

空间在哪里

日常、暴雨/故障、夜间/关闭

证据

SCENARIO_SIMULATION，不是现场观察

仍不知道

真实客流、积水、照度、时段与维护

QH-A01 SELECTED_FOR_DEVELOPMENT | FIELD + APPROVAL UNKNOWN


QH-A01

清河 QH-A01 接收前场 | 工程端点必须被下一段接住


概念接口详图；不改变到达链几何，不声称竣工端点或现状故障

概念节点 · 非现状

节点平面 / PLAN

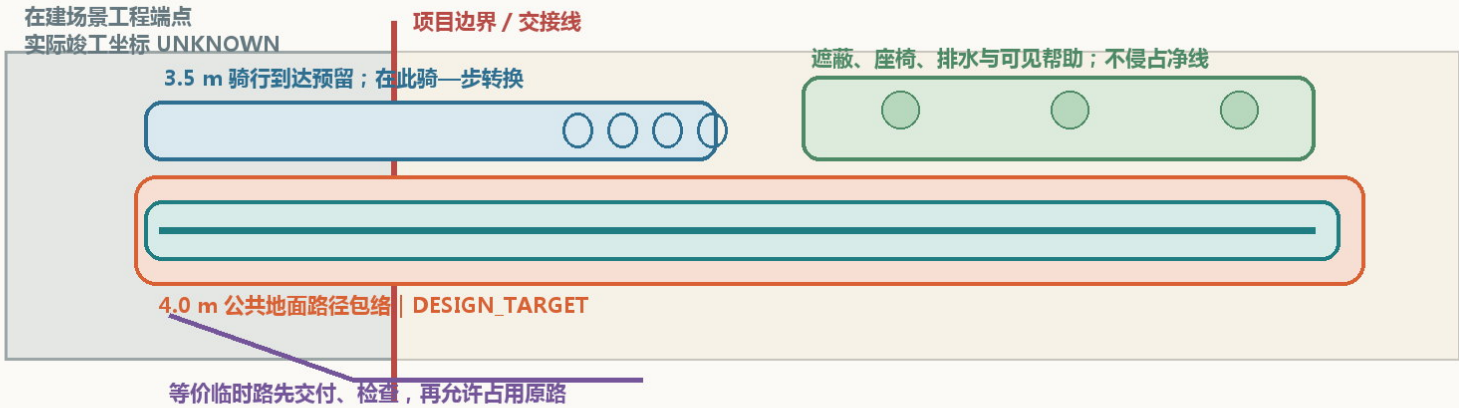

节点剖面 / SECTION

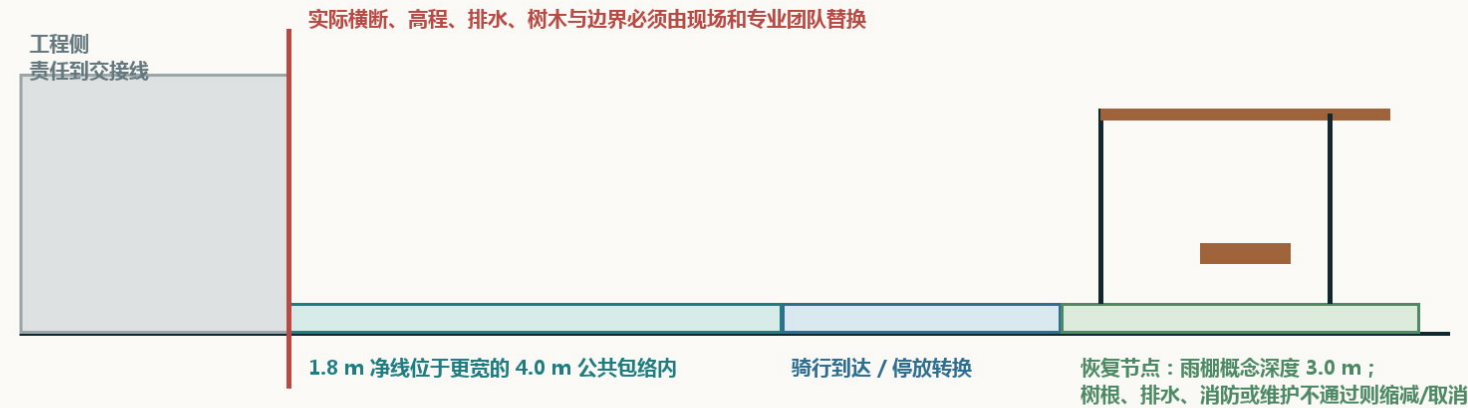

QH-A01 责任链

- interface from**
站区前场/出口门槛 IF-QH-02
- interface to**
在建场景工程边
- beneficiary**
成人、轮椅、老人/慢行、亲子、骑行者、夜班劳动者
- responsible role**
场景项目交付方 + 接收的站区公共空间维护方
- evidence**
IF-QH-01 / IF-QH-02 / QH-SCENE-PROGRESS
- approval_dependency**
竣工图、交接边界、站区/市政/无障碍验收、临时路检查
- maintenance_owner**
施工交接后的站区公共空间接收维护方
- stop_condition**
外部公共边缘、临时路或接收维护主体未核实，不得认定完整旅程完成

现场 + 审批仍 UNKNOWN

AI 原点 | No major intervention 是专业判断

Existing / Approved → PRESERVE → RE-AUDIT → TRIGGER

保留 → 重审 → 触发 → 可移除最小补丁



无可追溯剩余失败：NO NEW MAJOR INTERVENTION；重复已批工程或审批/维护门失败：HOLD / KILL

KEEP

保留现有/已批公共空间与直接 OD，不重复轴、桥、隧、地标或停车工程。

RE-AUDIT

交付后由六类人群在昼夜、雨热、施工和物业时段复核端到端可用性。

TRIGGER

只有可追溯的真实剩余失败才启动可移除、单接口的最小补丁。

STOP

无证据、重复官方工程、产权/消防/无障碍/维护任一失败即 HOLD 或 KILL。

六类人群与公共服务 | 平均改善不能抵消一人的不可达

正式图册

Design for people, not only for the validator.

08

人如何使用空间 | 日常、暴雨/设备不可用、夜间/物业关闭

同一概念空间、同一镜头：A 始终可用；C 只作条件增强；人的基本通行不依赖 AI、手机、单一电梯或营业时段

概念体验 | 非现场证据



A | 全时、无台阶、物业外公共地面基线
C | 条件公共首层：遮蔽 + 非消费停留 + 帮助
雨热依聚：树荫/雨棚/排水/防滑
故障兜底：人工帮助 + 夜间旁路 + 骑行转换

AI 生成概念图 (OpenAI built-in image generation, 2026-08-13) + 本地矢量标注：仅表达设计意图，不是现状照片、居民观察或获批工程效果图

概念设计表达 | 不是测绘、法定用地、官方红线或施工图

为什么

失败条件暴露最弱者

空间在哪里

A、恢复节点与物业外旁路

证据

六人群 + 雨/夜/故障

仍不知道

现场可用性与服务时段

公共服务接口：厕所、饮水、座椅、遮阴/避雨、排水防滑、低眩光照明与可见人工帮助
；实际位置与开放时段仍 UNKNOWN。



成人



轮椅



老人



亲子



骑行



夜班

日常

无台阶

休息


安全

骑一步

全时

文化进入日常空间 | 可读、可停、可到达，不做符号贴图

Verified movement + view + pause + interpretation

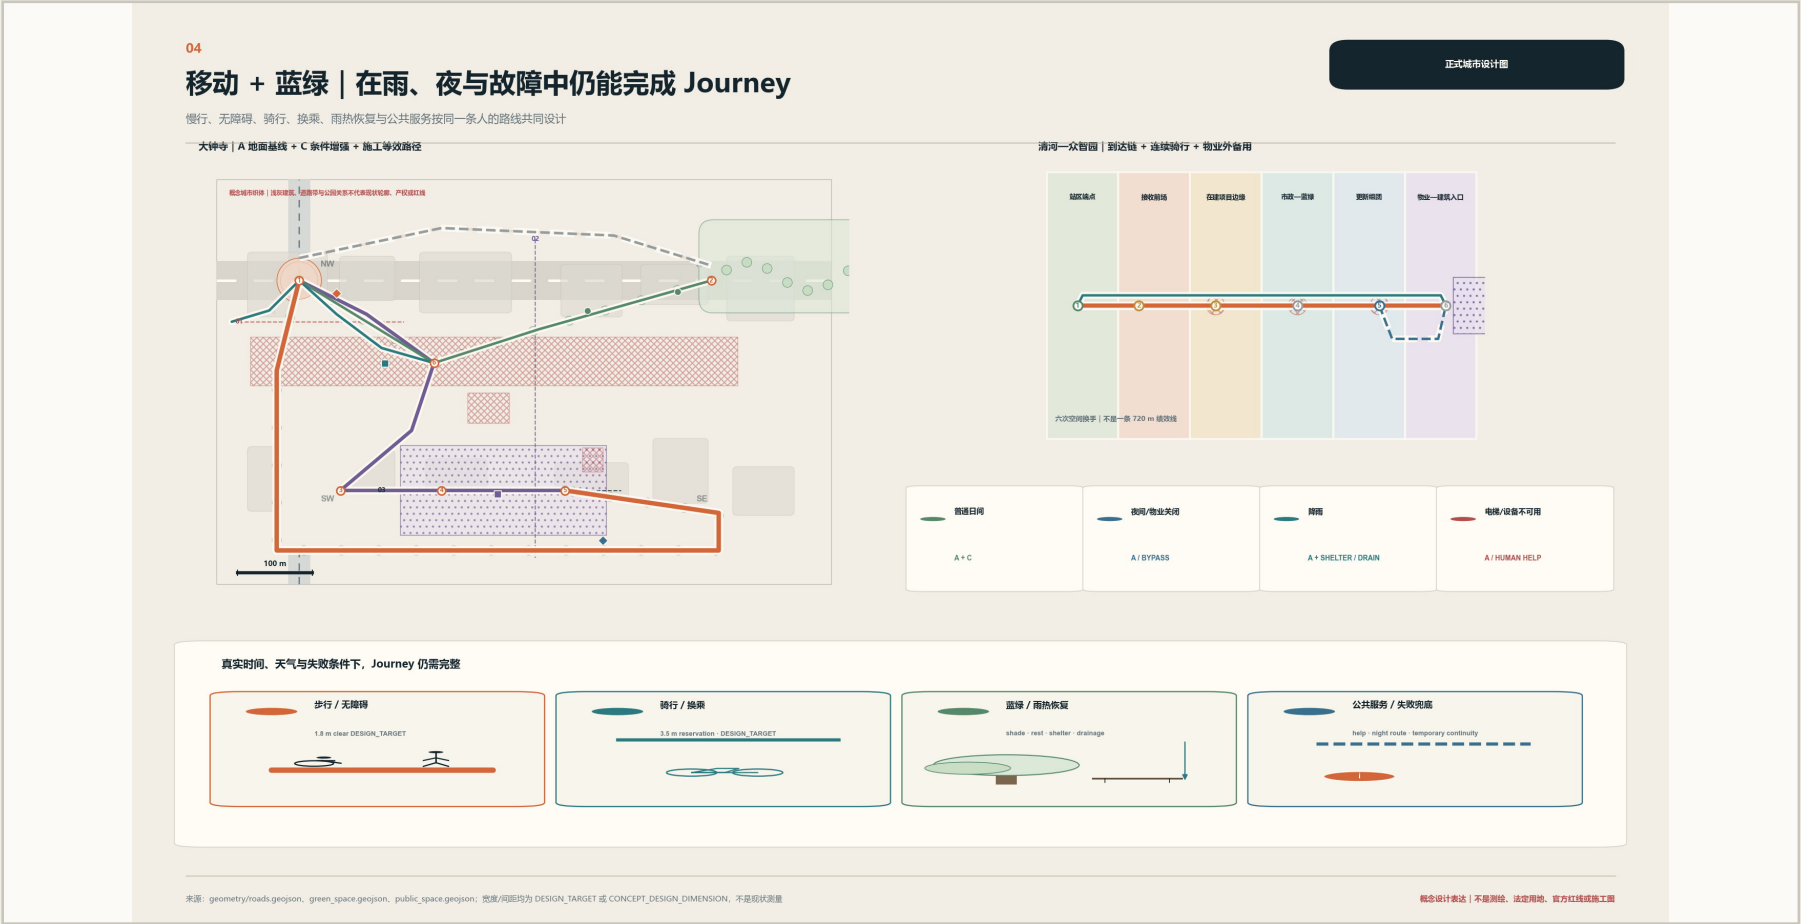

分期与责任链 | 先确认，后连续，再接口，最后条件性首层

空间动作 → 建议牵头角色 → 建议维护角色 → 启动证据 → STOP



阶段 / 空间动作	建议牵头角色	建议维护角色	启动证据	STOP
0 全案证据锁定	规划/测绘及相应专业复核角色	相应现有资产维护角色（待确认）	official 边界/控规/竣工图、现场、权属	来源不可追溯或专业条件未确认
1 大钟寺 A + 临时连续	市政公共地交付角色 + 轨道运营角色	按资产边界的公共地维护角色	测绘、交通/轨道、无障碍、应急复核	不能安全保留连续净线
2 顺馨园 / 清河接口	公园/市政 + 施工与接收公共资产角色	公园维护 / 接收公共资产角色	树木排水、竣工端点、交接边界	下一公共线、临时路或维护未确认
3 条件 C / AI原点补丁	未来开发/物业或现有资产/物业角色	外部公共地或现有资产维护角色	权利、消防、无障碍、时段、剩余失败	依赖营业/单一电梯、重复工程或无剩余失败

表中均为建议角色，不是已确认单位；下一段接收或维护未确认即 HOLD。

指标 + 证据 | 已知、设计、未知、重审不混用

OFFICIAL / OBSERVED / DERIVED / CONCEPTUAL_DERIVED / DESIGN_TARGET / SCENARIO_SIMULATION / UNKNOWN

05

指标 + 证据 | 知道、设计、未知、重审

不把 42 条血缘做成 KPI 排行；只保留评委判断空间设计可信用所需的信息

正式城市设计图

A | 我们确实知道

43.6 km²

统筹研究范围 | OFFICIAL published area

11.4 km²

总体设计范围 | OFFICIAL published area

3

重点区数量 | OFFICIAL

工程状态 (本次审计基线) :
BUILT / UNDER CONSTRUCTION / APPROVED / PLANNED 已有官方公开来源；它们不等于 Journey PASS

PROVISIONAL GEOMETRY

所有显示 polygon 仍为粗略临时约束。

B | 我们设计了什么

12

大钟寺 + 清河跨项目接口

11

Spatial Actions | 每条含 8 项责任字段

A + C

独立几何 | A 不依赖 C

0

AI 原点重大新增 | CONCEPTUAL_DERIVED

关键尺度语义

1.8 m

无障碍净线

DESIGN_TARGET

4.0 m

站区步道包络

DESIGN_TARGET

3.0 m

公共首层通道

CONCEPT_DIMENSION

50 m

恢复节点测试间距

DESIGN_TARGET

C | 仍然 UNKNOWN

官方 SITE / KEY_AREA polygon

UNKNOWN # FAIL # 0

大钟寺真实站口、过街与道路横断面

UNKNOWN # FAIL # 0

清河项目铺点与六次移交边界坐标

UNKNOWN # FAIL # 0

AI 原点官方工程后的剩余失败

UNKNOWN # FAIL # 0

开放时段、公共权利、产权与维护主体

UNKNOWN # FAIL # 0

六类人群日/夜/雨/故障现场通过结果

UNKNOWN # FAIL # 0

没有现场 OBSERVED 数值；没有“设计后提升率”；没有把概念中心线长度做成绩效。

D | 怎样重新核验

1

公开证据

2

人的 Journey

3

接口失败

4

空间动作

5

故障复测

GEOMETRY / DESIGN

PASS

FIELD

UNKNOWN

APPROVAL

UNKNOWN

AI Auditor 仅占低注意力复核层。

来源: metrics.json, spatial_actions.json, journey_auditor_v4.json；所有数值保留 OFFICIAL / DERIVED / CONCEPTUAL_DERIVED / DESIGN_TARGET / UNKNOWN 语义

概念设计表达 | 不是测绘、法定用地、官方红线或施工图

为什么

指标服务判断，不制造确定性

空间在哪里

面积、路线、接口、状态与复审门

证据

可复算 geometry/metrics/source mapping

仍不知道

现场、竣工、权属、审批与维护 PASS

概念城市设计 | 非测绘、红线、产权或批准工程图

19/20

删掉 AI 术语后，城市设计仍然成立

Design for people, not only for the validator.

