

One small site, one ordinary path

Qinghe civic interface: obtain a human explanation and handoff for a step-free transfer to Line 13 without a smartphone

This iteration no longer substitutes a large narrative for site evidence. The line stops outside fare and security control; AI is optional support only.

one real small site

one ordinary civic-service task

complete N0-N5 non-AI path

evidence-backed
ground-underground relationship

Evidence base and what remains unknown

Public records support functional relationships, not an exact route, scale or engineering placement.

VERIFIABLE

Official station diagrams and records confirm surface walking, underpasses, B1 services and transfer-related elements.

TO VERIFY

Exact entrance, turns, gradient, level change, clear width, opening state, public boundary and staffed point.

DESIGN RESPONSE

Fixed overview, paper route card and handoff marker; all reversible and outside fare or security control.

Core sources: QH-STATION-MAP-2026 · QH-UNDERGROUND-WALK-2026 · QH-STATION-FLOORS-2019 · QH-B1-SERVICE-HALL-2024 · QH-ACCESS-AUDIT-2025 · QH-HUMAN-HANDOFF-2026

QINGHE CIVIC HANDOFF · GROUND-UNDERGROUND NTS SECTION


NTS · NOT SURVEYED
NOT FOR IMPLEMENTATION

Only publicly supported functional relationships are shown; exact entrance, route, dimensions and opening status require verification

SURFACE PUBLIC LEVEL



UNDERGROUND PUBLIC LEVEL

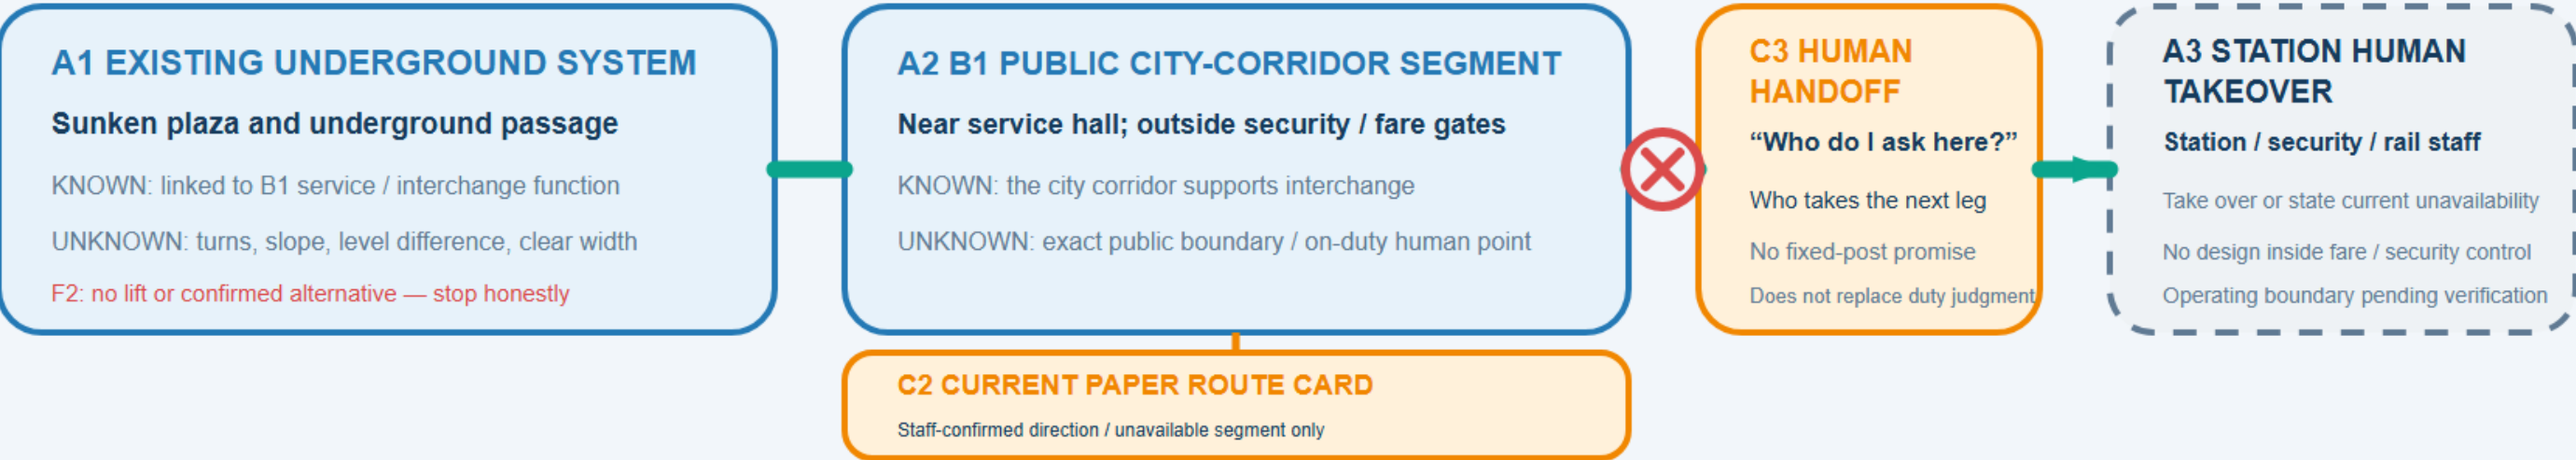

CURRENT SPATIAL DECISION: NON-AI MAIN CHAIN FIRST; WITHOUT ON-DUTY HUMAN CONFIRMATION, DO NOT DRAW AN UNKNOWN ROUTE — STOP HONESTLY.

N0 FIXED OVERVIEW → N1 EXISTING UNDERGROUND SYSTEM → N2 HUMAN EXPLANATION → N3 PAPER CARD → N4 EXISTING SIGN / LIFT → N5 HUMAN TAKEOVER

— Evidence-supported function - - - Facility exists; exact relation unknown — Reversible proposal component ⊗ Stop; do not invent an alternative

EVIDENCE BOUNDARY: no claim of exact underground route, scale, ownership, utilities, fire, civil defence, metro boundary, footfall, cost, fixed post or delivery.


Complete non-AI path and failure branches

The ordinary chain needs no network, AI, account or scan. A person explains interruption or stops honestly.

“Transfer without a smartphone” • complete non-AI flow

NTS • NON-SURVEY • NON-IMPLEMENTATION

One ordinary task: ask for and reach the human handoff for a step-free route to Line 13

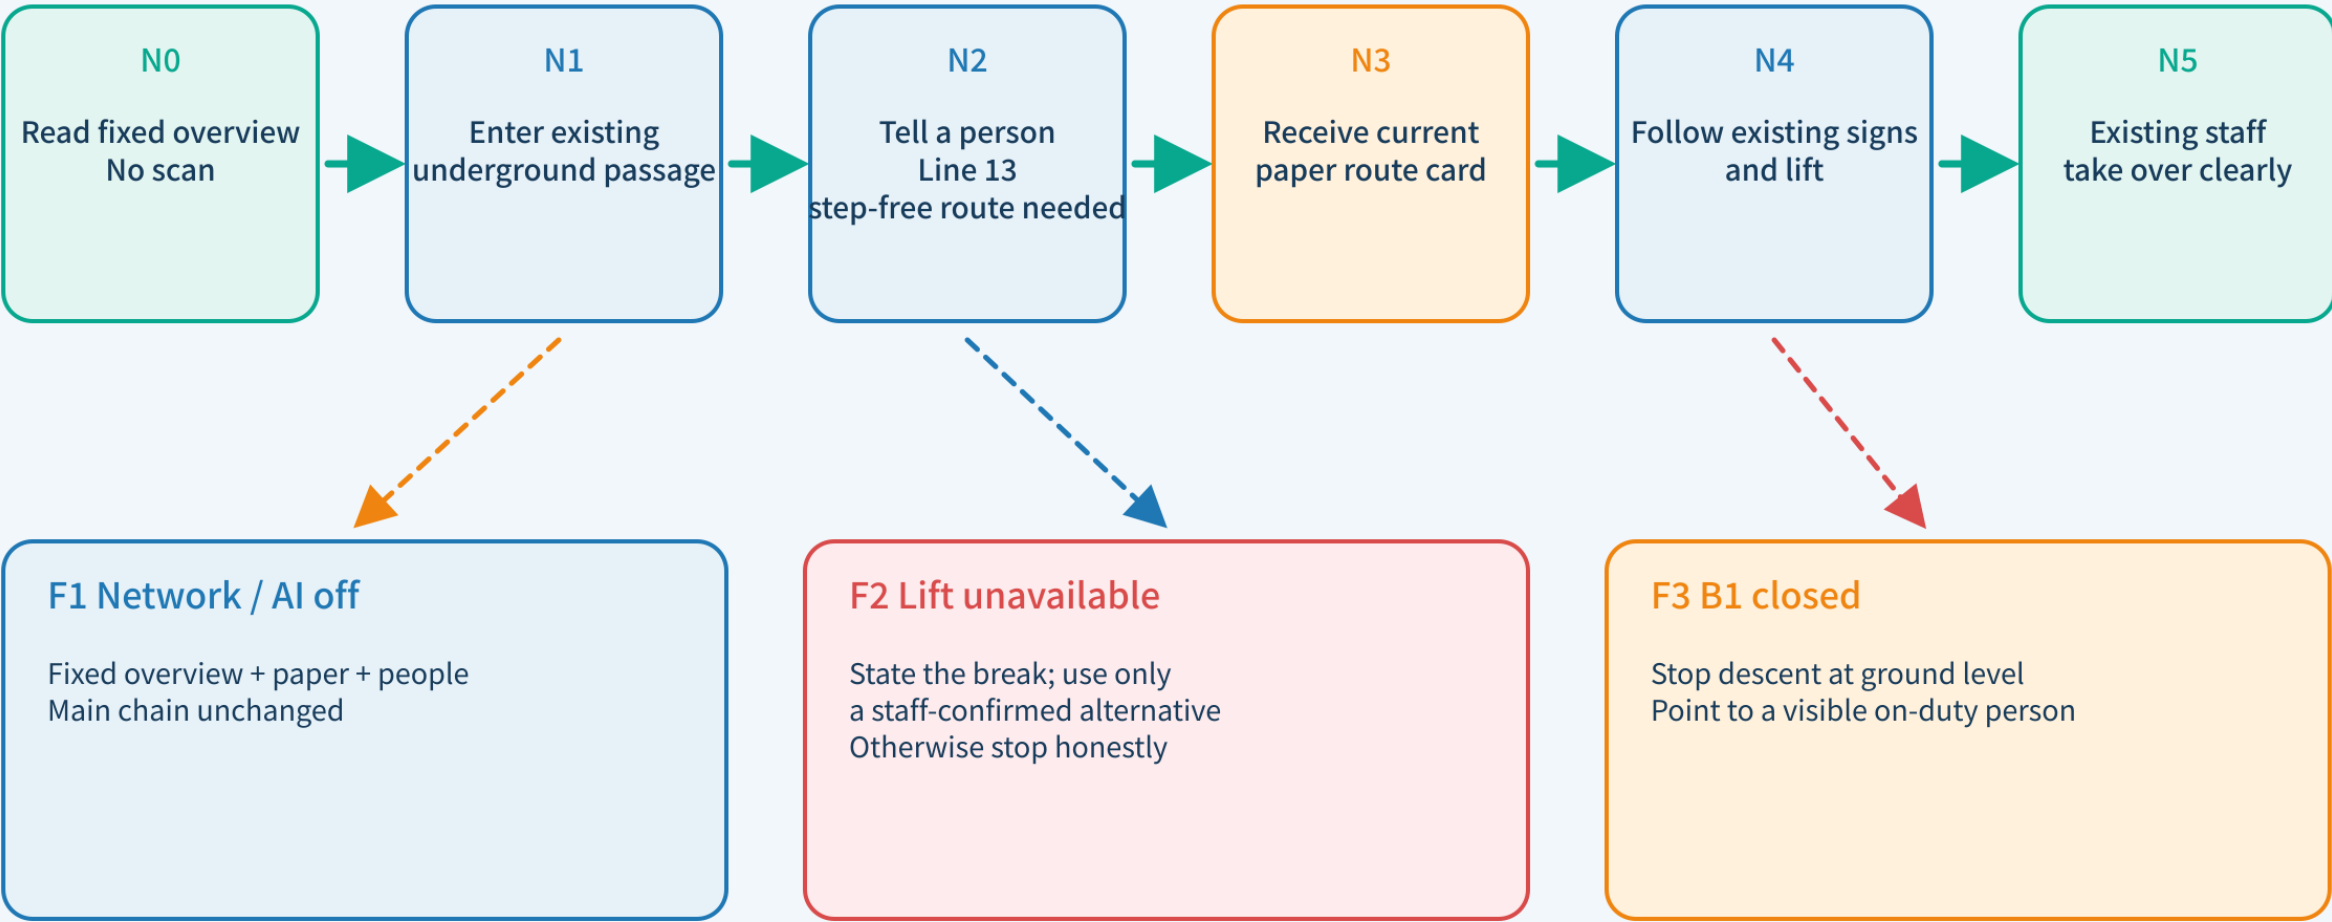

Complete = a person takes over, or states the limitation and real alternative; AI never fills an unknown route

Three reversible components; continuous human responsibility


AI may translate, read aloud or prompt only. It may not confirm lift status or fill an unknown route.

Three reversible components • continuous human responsibility

AI is optional translation / read-aloud support; switching it off leaves the ordinary service chain intact

NTS • NON-SURVEY • NON-IMPLEMENTATION

SOLE TASK: without a phone or AI, obtain a human explanation and handoff for a step-free route to Line 13

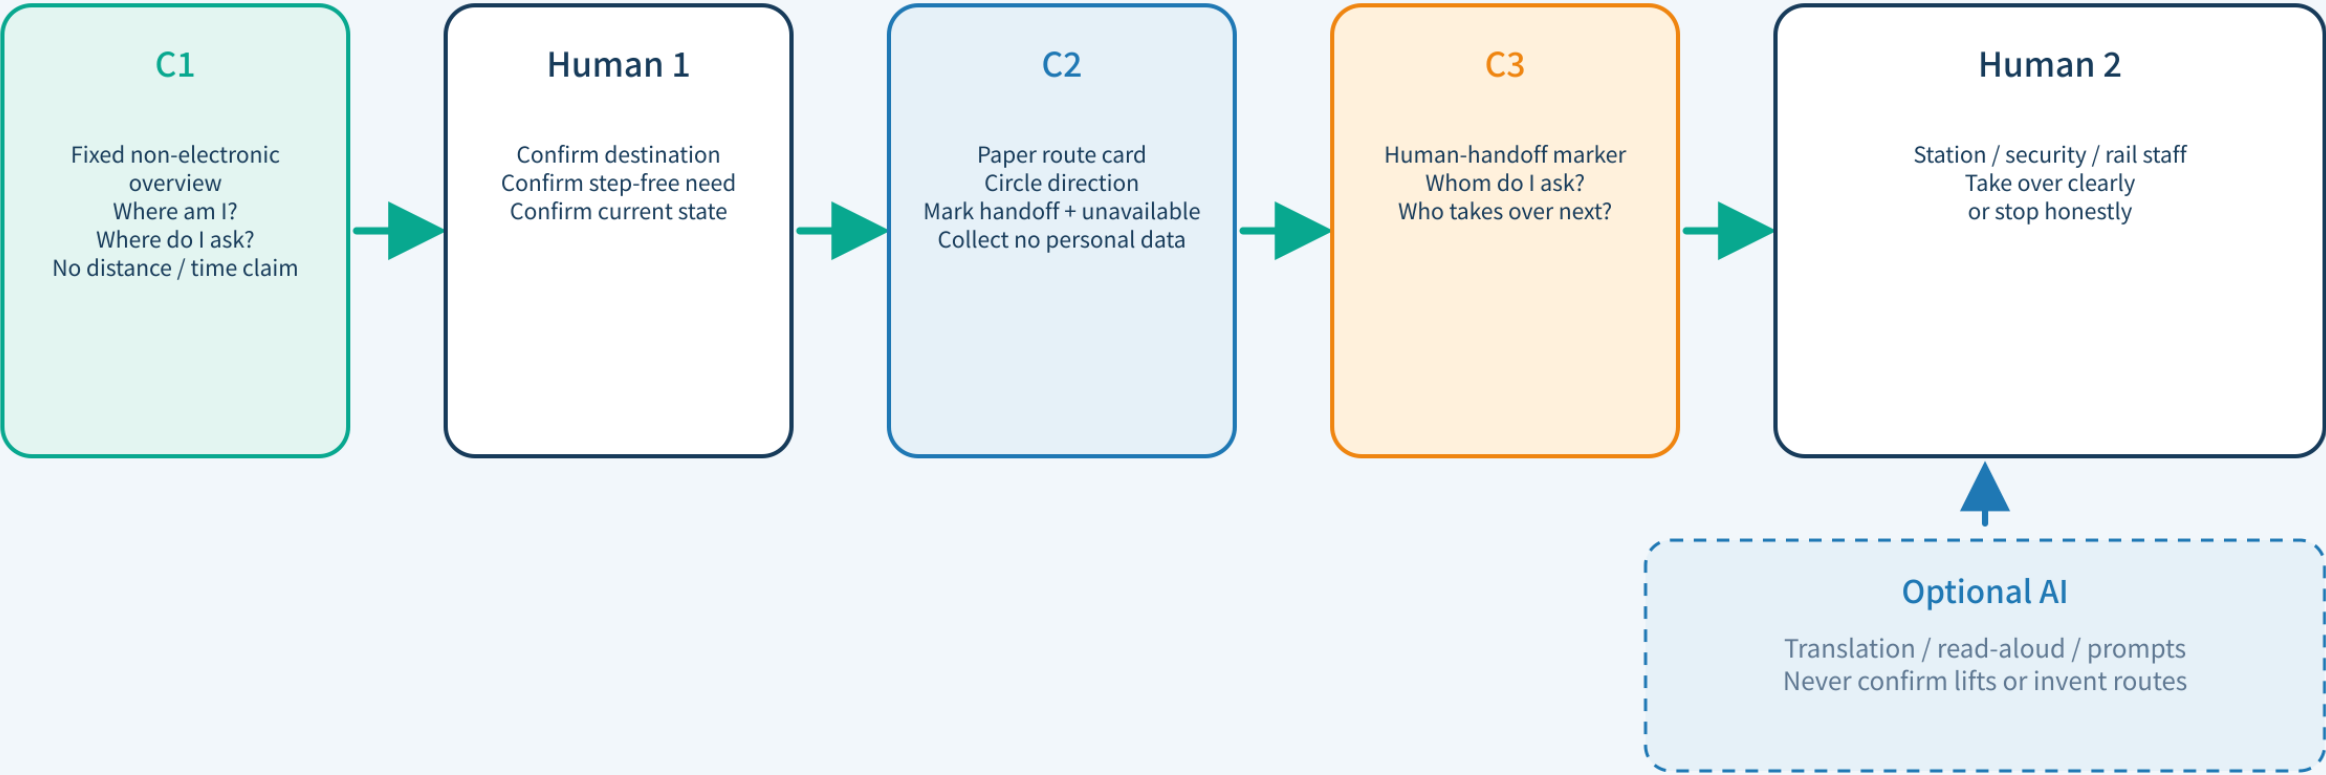

EXCLUDED: inside fare / security control • ticketing or gates • identity / face / voice / trail collection • staffing or delivery promise

Stop conditions matter more than smart features

A smooth demonstration must not conceal a real interruption.

F1 Network / AI off

Fixed overview, paper and people continue; the main chain is unchanged.

F2 Lift unavailable

State the break; use only a current staff-confirmed alternative, otherwise stop.


F3 B1 unavailable

Stop descent at ground level and point to a visible on-duty person.

No claim of: exact underground route, scale or dimensions, title, utilities, fire, civil defence, metro operating boundary, footfall or capacity, cost, staffing or delivery.

Relation to the wider urban design

The Jing-Zhang corridor remains the coordinated study frame. The Qinghe prototype neither replaces statutory boundaries nor derives engineering placement from the overall diagram.

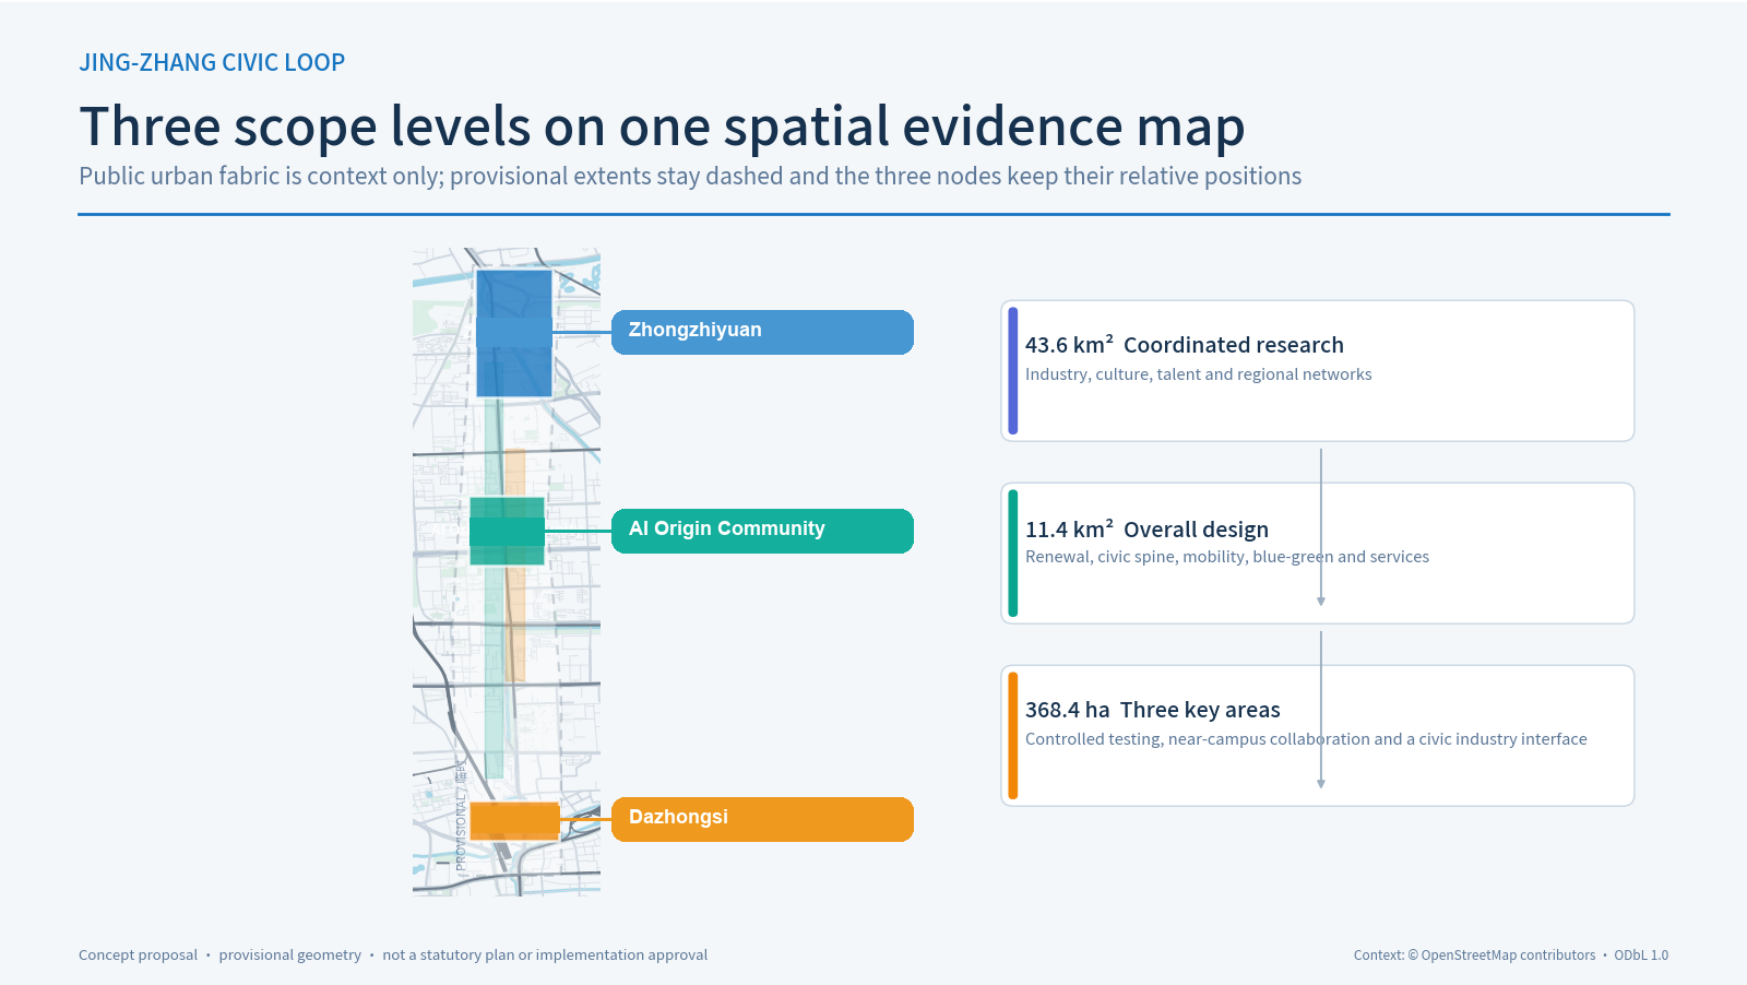

The 11.4 km², green ratio and public-space ratio belong to provisional overall-design geometry, not the Qinghe site or its performance. Dazhongsi and other key areas remain conceptual; AI Origin is a historical lead only.

Next stage: add evidence, not promises

A review loop that remains possible without official cooperation.

1 Visible-site check

Record only public entrances, signs, visible on-duty people and current opening state; infer no title.

2 Accessibility walk-through

Real users or proxies record interruption points; do not pre-claim distance or time.

3 Paper-card mock-up


Test whether the question is understood and a person can hand over; collect no identity, voice or trail.

4 Professional gate

Fire, civil defence, metro, structure, MEP or construction questions go to professionals and authorities.

Belt-wide components, visual identities and operating interfaces

CONCEPT RULE BOARD · ORDINARY SERVICE BEFORE AI · NTS · NO EXISTING-STATE, PARTNERSHIP OR DELIVERY CLAIM

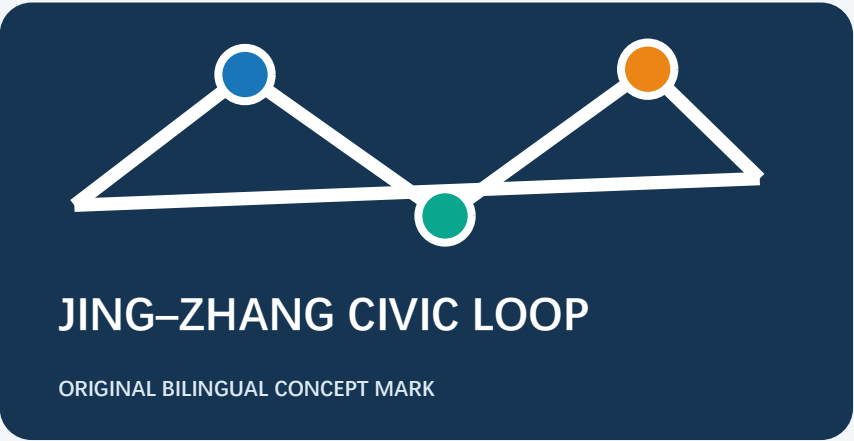

Belt mark

Identifies the overall method; original sample, not a registered mark, approved sign or existing railway identity.

Cultural wayfinding

Verified history and sources only; heritage overlay, content rights and accessible readability first.

Activity brand

One confirmed event only; gate organiser, site, data, brand and ordinary participation each time.

Honours display

One revocable evidence record only; issuer, subject, status, expiry, source and rights all required.

Rights boundary: original inline geometric sample; system-font fallback; no third-party logo, photograph or railway image. Production still requires font embedding, name/mark registration and itemised third-party clearance.

B01—B04

B01 Civic-service baseline

Fixed overview, paper card and human handoff run first. AI is switchable translation/read-aloud only. Remove it if route, role or authority fails; retain ordinary service.

B02 Cultural wayfinding

Movable, low-impact, traceable. Open after heritage, rights and readability gates; remove on failed source, withdrawn rights or control conflict.

B03 Activity interface

Confirm organiser, authority, ordinary access and quiet-day baseline per event. Remove temporary material afterwards; annual concepts grant nothing.

B04 Honours display

No paid ranking, unverified logo or generated endorsement. Remove on source failure, expiry, withdrawal, objection or broken audit continuity.

OPERATING INTERFACES / 运营接口

Developer clinic: reproducible issue → issue card/test protocol | Open scenario: ordinary task + non-AI chain → P1/P2 brief | International explanation: verified case + limits → bilingual evidence card | Talent/company handoff: consented enquiry → minimal human referral | Regional exchange: party-confirmed question + evidence → de-branded reuse card. Each gates receiver, rights, ordinary access, professional review, retention/withdrawal and feedback cycle; otherwise it remains P0 and claims no existing community, event, partner or conversion result.

Full-stack ecosystem, Xiaoyue ten-card map and four gates

CONCEPT OPERATING MAP · CARRIERS PENDING · NO EQUIPMENT, EVENT, FUNDING, STAFFING OR PERFORMANCE PROMISE

FULL-STACK CAPABILITY–CARRIER–RETURN

Research / open source Origin, Zhongzhiyuan, movable release point paper issue card first reusable method returned; team, programme and IP pending.	Model / compute / recovery Pending authorised isolation only no device in public green space no placement without compute, energy, network and responsibility.	Data / rights / audit Reversible Dazhongsi interface human rights note + cleared synthetic data stop on unclear source, licence or withdrawal.
Talent / community Service wing, Origin and ordinary points human enquiry + paper referral no post, housing, volume or employment inference.	Capital / professional Public directory + human consultation no automated decision no funding, fee, finance, patent or transfer promise.	Everyday / international Xiaoyue wing and spine return bilingual evidence and failure no programme, partner, frequency, footfall or stable-resource claim.

XIAOYUE WING × TEN SCENARIO CARDS

S01–02 Release / test Cleared cards may enter; Zhongzhiyuan returns status only and the sandbox stays out of green space.	S03–04 Compute / Qinghe No device without an authorised indoor node; Qinghe returns "ordinary chain first; stop on unknown."	S05–06 Heritage / low carbon Clear stories first; no performance without measurement; return source cards and observation method.	S07–08 Transfer / data Human referral + synthetic-data rights note; no finance, patent, transfer or recruitment result.	S09–10 Community / route Paper/human completion first; confirm node, organiser and authority each time, or do not start.
---	--	---	---	--

The Xiaoyue wing translates and returns scenarios; it is not one physical placement and grants no building, equipment or event authority.

R1 / G1 / M1 / L1

R1 Responsibility Name body, scope, stop right, ordinary receiver, complaint/withdrawal, expiry and exit; nobody currently accepts by implication.	G1 Entry Boundary/title, ordinary path, accessibility/professional advice, content/data rights, human handoff, appeal and restoration all required.	M1 Measurement After authority define task, denominator, period, strata and failure record; currently no completion, delay or threshold claim.	L1 Resource Paper, human service, clearance, maintenance, funding, renewal, retirement and archive stay blank; no amount, staff or cost.
--	---	--	--