

京张对开 THE TWO-WAY LINE

让百年走廊双向运行的AI创新带城市设计



标识 · 双箭同轨

两条平行轨线以轨枕横杠相连，上端北向、下端南向；轨线与横杠围出的负空间即「开」字骨架。绿电绿+上行的能源与算力，隧道深盖=地下暗线，站旁砖红=遗产与轨枕。

总体概念板

京张对开 · 总体概念结构


明线+暗线 · 三站一门 · 两台八口 · 双河冷环 — 11.4 km² 总体设计范围



京张对开走廊(概念示意)



明线 / 暗线 双层剖面(概念示意, 非工程剖面)

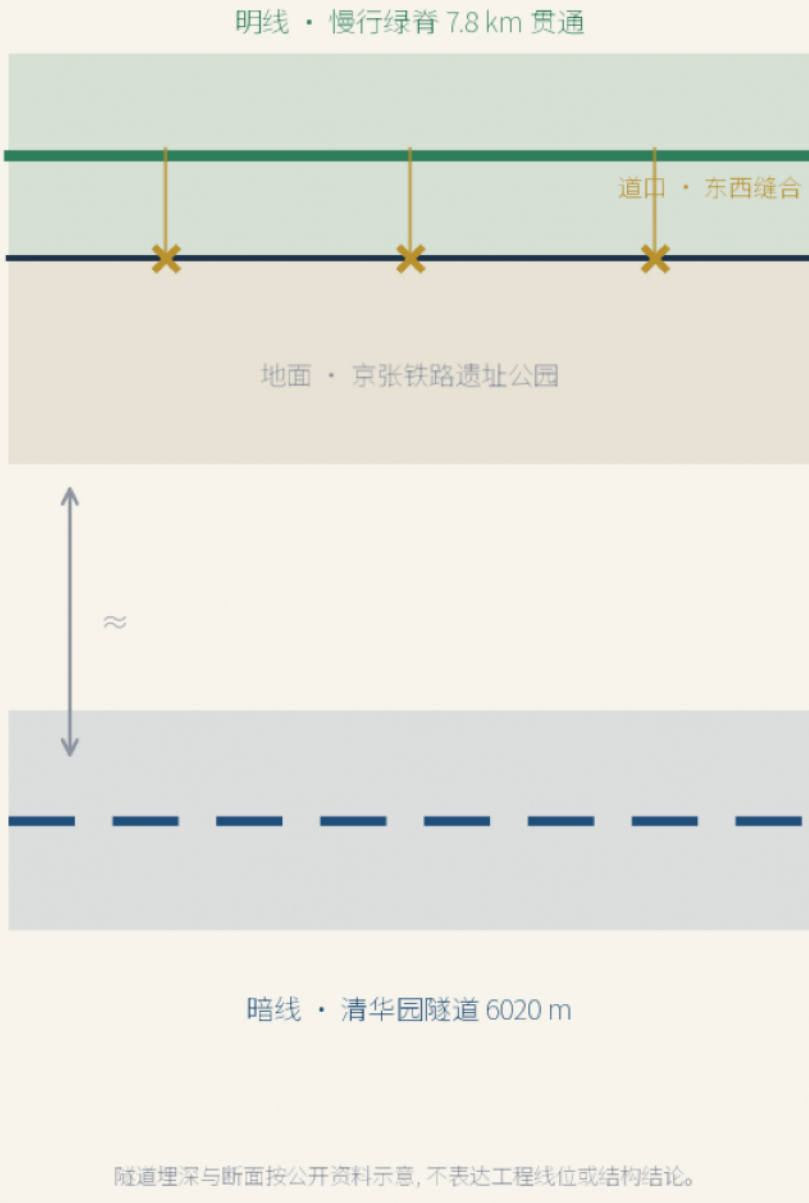

三站一门 · 节点定位

众智站	192.1 ha
众智站	众智站与标准治理 · 机务段
原点站	104.3 ha
原点站	松城胡同 · 孵化转化
大钟站	72.0 ha
大钟站	智能原生消费 · 下行终点
对开门	门户节点
对开门	北京北站门户 · 到达序列

八口 · 东西缝合点与基正交道路

K1	学院南路	次干路
K2	北三环中路	快速路
K3	知春路	主干路
K4	北四环中路	快速路
K5	成府路	次干路
K6	清华东路	主干路
K7	月泉路	支路
K8	清河湾	水渠 · 范围约85m

节点位置由正负空间逻辑决定, 两条快速路是串联的两点, 知春、成府、清华东路是串联的人流串联中的三站。K8 位于总体设计范围北缘之外约85米, 属于非设计范围北缘之外约85米, 属于非设计范围北缘之外约85米。

边界状态: 临时规划范围(provisional) — 依据公开文字四至的ODM标准中线自行推导出并标注面积权重, 非官方过线, 不得用于审批、行属/精确面积; 官方polygon发布后整合重置。图源: © OpenStreetMap contributors (ODBL), 本图由国内 GeoJSON 与 metrics 派生, 属概念建筑: w943 / jingzhang-two-way-line · 2026-08

三处重点区 · 由北到南的密度梯度

重点区	面积	概念建筑	概念建面	概念毛容积率	首位用地	空间性格
众智站 · 众智园	192.1 ha	47 栋	144.8 万m²	0.75	科研 43.1%	院区型
原点站 · AI原点社区	104.3 ha	49 栋	100.5 万m²	0.96	社区服务 35.7%	街区型
大钟站 · 大钟寺	72.0 ha	38 栋	120.8 万m²	1.68	科研 59.3%	城市型



概念毛容积率由包内概念建筑除以重点区面积得出, 非法定容积率; 用地构成为 EPSG:4548 下逐块与重点区求交后的累算值, 三区均恰好覆盖各自面积。

两处范围事实 · 主动披露

①八处渡口中的清河清道口位于总体设计范围北缘之外约85米——该处任务正是把明线引出边界碰到清河水平, 跨界为功能所必需, 其用地不计入范围内复算。②清华园车站旧址位于范围以西约389米, 在统筹研究范围内, 故班次S8为跨范围仪式性场所。两处均由本包复算发现并登记于 assumptions.json。

三层范围与用地结构

43.6 km² 统筹研究 · 11.4 km² 总体设计 · 368.4 ha 重点区 — 189 块全覆盖分区

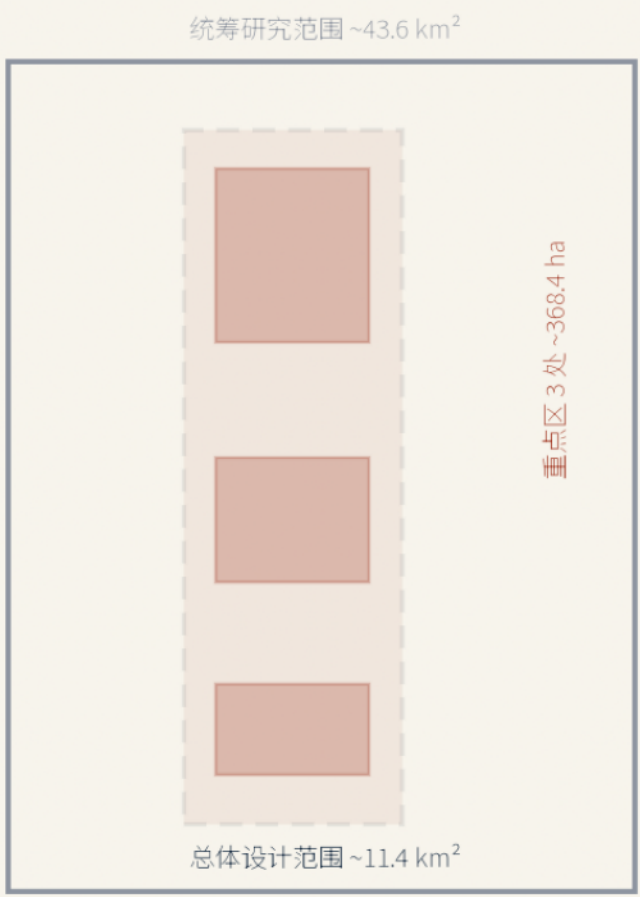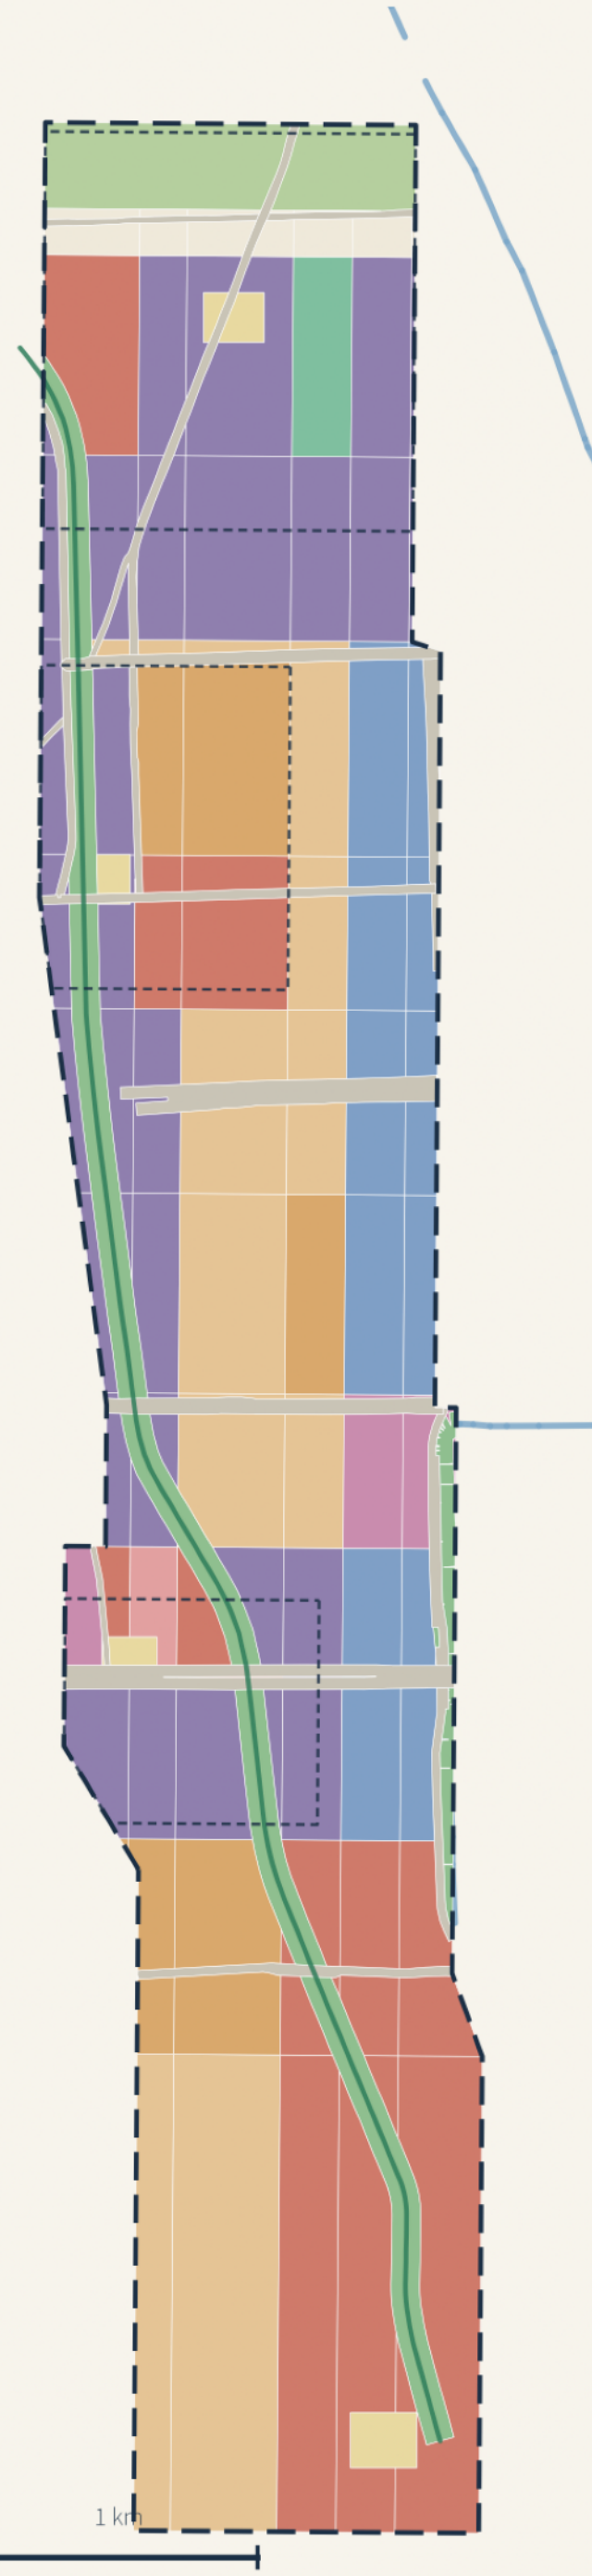

科研	258.0 × 10³ m² 22.6%
城镇住宅	209.3 × 10³ m² 18.4%
商业服务业	203.5 × 10³ m² 17.9%
教育	111.5 × 10³ m² 9.8%
社区服务	88.9 × 10³ m² 7.9%
公园绿地	80.3 × 10³ m² 7.0%
道路	74.1 × 10³ m² 6.5%
防护绿地	40.6 × 10³ m² 3.6%
文化	20.8 × 10³ m² 1.8%
留白(机动储备)	18.6 × 10³ m² 1.6%
体育	15.4 × 10³ m² 1.4%
广场	11.7 × 10³ m² 1.0%
医疗卫生	6.3 × 10³ m² 0.6%

核心命题

把「京张」读完整——这条走廊有两端。1909年京张铁路把能源与工程自信运进京; 2019年京张高铁在遗址公园正下方的清华园隧道里继续飞驰; 2022年国家「东数西算」把训练算力放到张家口绿电基地。创新带不是9公里的自恋, 而是200公里对开关系在城市里的南端场站: 绿电与算力上行进京, 模型、人才与场景下行出塞。

空间结构 · 明线+暗线 / 三站一门 / 两台八口 / 双河冷环

明线=7.8公里遗址公园慢行绿带, 走人与文化; 暗线=清华园隧道高铁, 走速度与联通。三站=众智站(训练与标准)、原点站(校城换向)、大钟站(内容与数据资产); 一门=北京北站「对开门」。西台=中关村科技服务翼(要素上车), 东台=小月河场景赋能翼(场景上车); 八口=八处东西缝合渡口。双河冷环=清河+小月河蓝绿系统与端侧算力余热回用。

制度内核 · 对开协议




每一次AI场景部署都是一对班次: 上行班次采集数据、消耗算力, 必须配下行班次交付服务与公共回馈; 谁能叫停、如何退出, 写进每张场景卡。只取不还的部署不排图。场景发布采用年度「运行图」制度。

京张对开 THE TWO-WAY LINE

系统与实施板

三处重点区域详细设计


众智站(192.1 ha) · 原点站(104.3 ha) · 大钟站(72.0 ha) — 规划综合实施方案深度(概念)

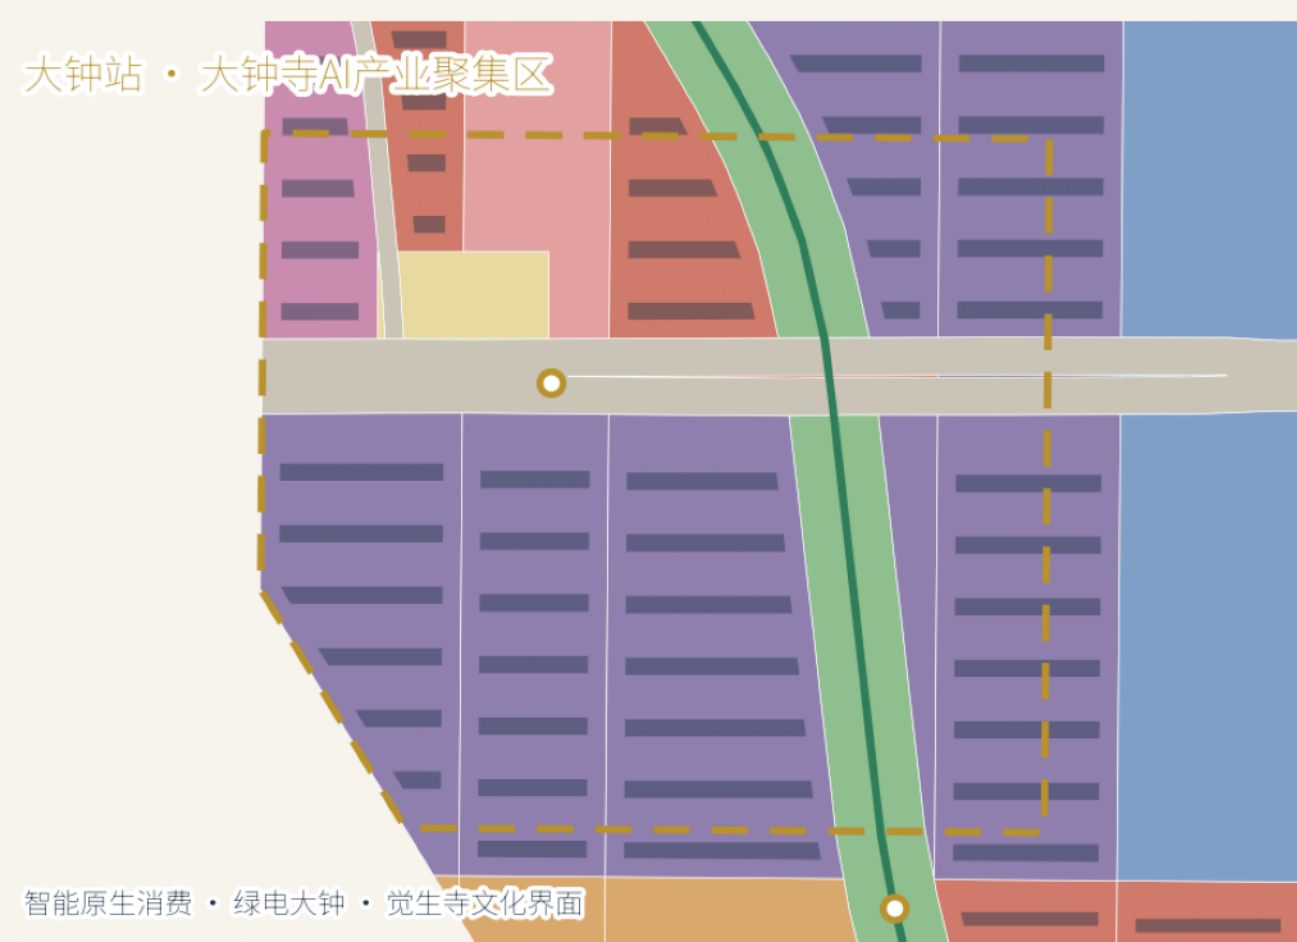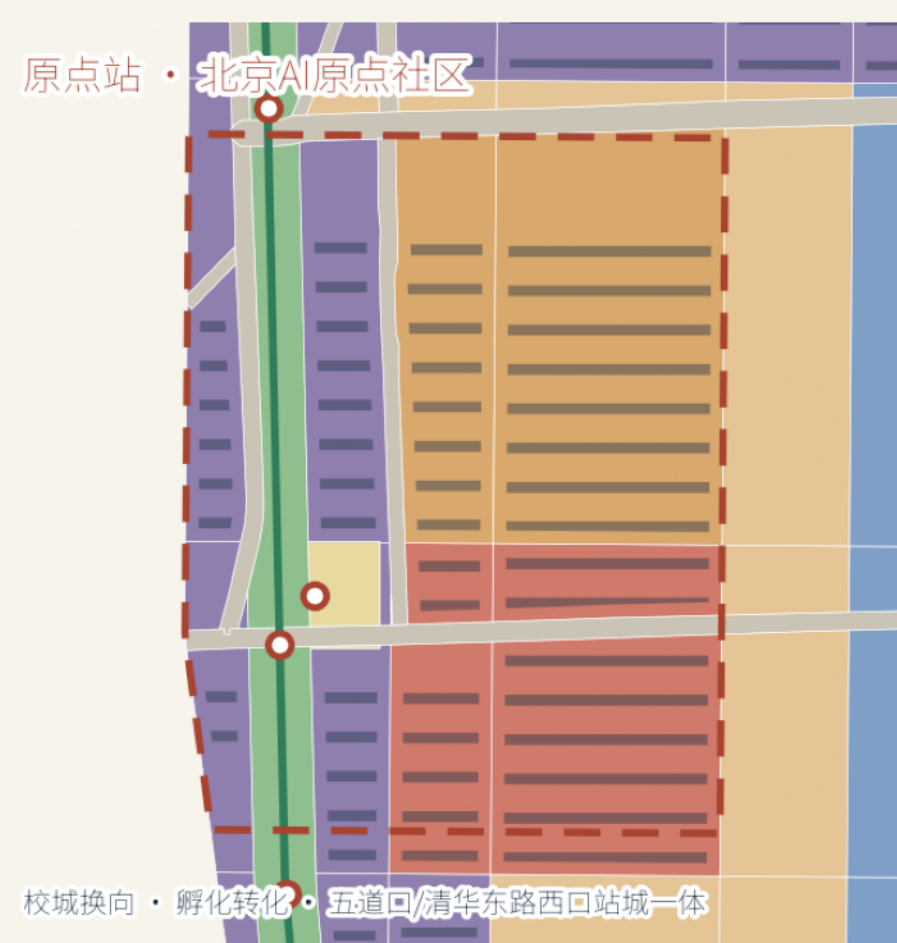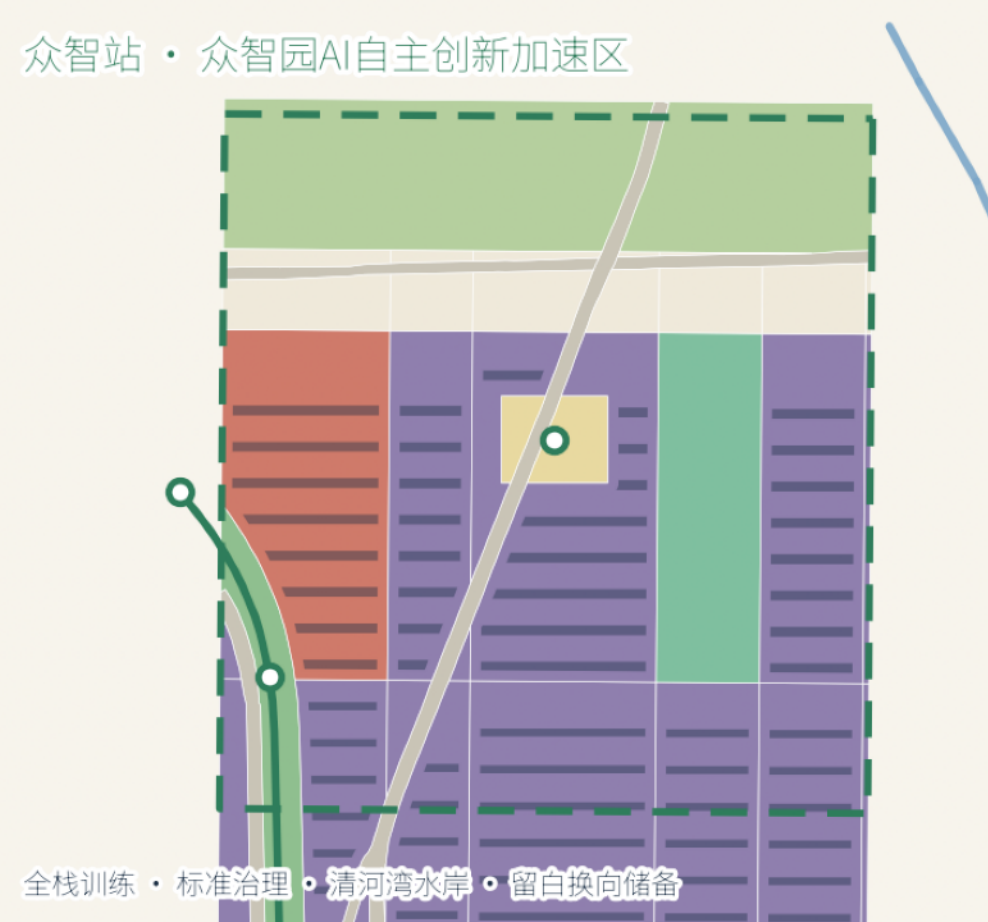

边界状态: 临时勘测范围 (provisional) — 依据公告文字描述的OSM街道中线行线并按公告面积和精度, 非官方红线, 不得用于审批/权属/精确面积, 官方polygon发布后整包重算。底图: © OpenStreetMap contributors (ODbL)。本图由包内 GeoJSON 与 metrics 派生, 属概念建议。x843/jingzhang-two-way-line · 2026-08

交通慢行与蓝绿公共空间系统


14条微循环道路 · 明线贯通 · 八口缝合 · 双河冷环 · 四站一体化

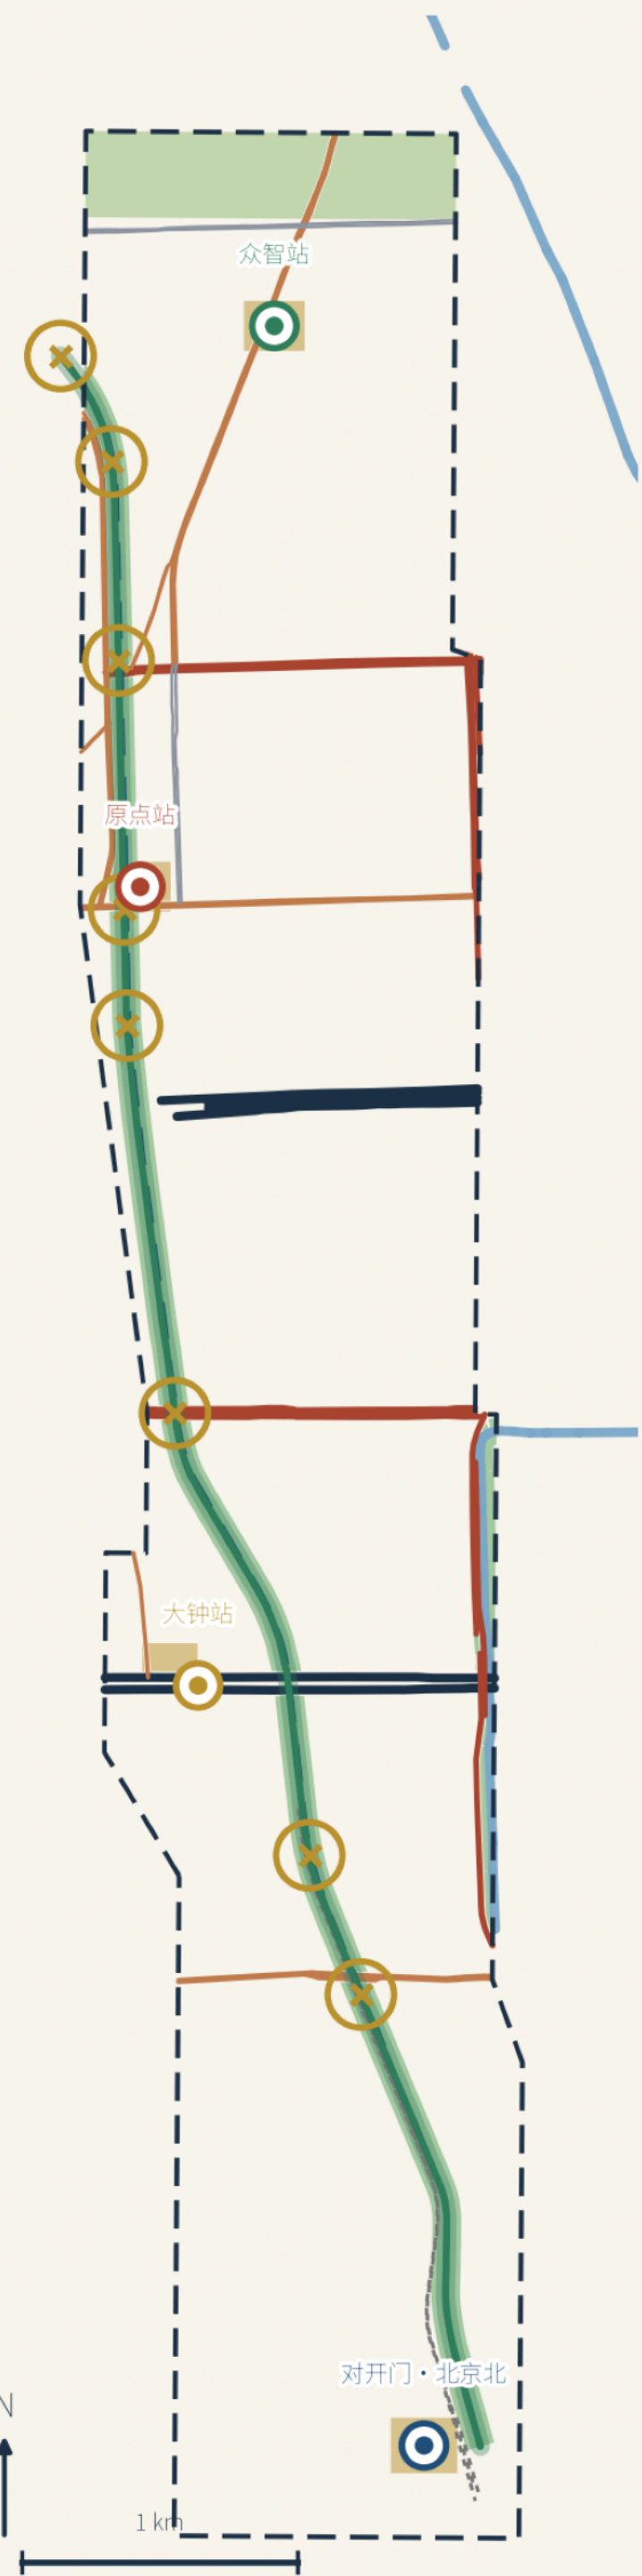

边界状态: 临时船位范围 (provisional) -- 依据公告文字四至的OSM街道中线自行推导并按公告坐标标注, 非官方红线, 不得用于审批、权属/精确定量; 官方polygon发布后整型重置。底图: © OpenStreetMap contributors (ODBL), 本图由包内 GeoJSON 与 metrics 派生, 属概念建议。x843/jingzhang-two-way-line - 2026-08

对开协议 · 可复算的准入契约

六条规则逐条取自本方案正文，写成机读契约与桌面推演；评审者可自行运行复算，不必采信本文结论。


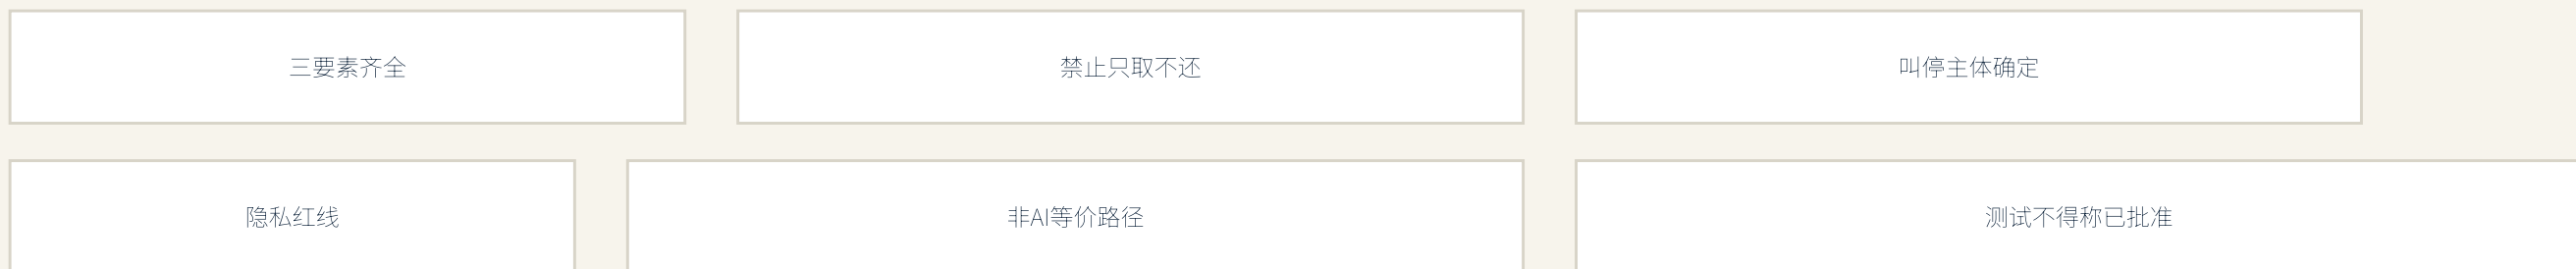


12 / 12 可排图

6 / 6 被对应规则拦下

核心指标复算与证据链

全部空间指标由包内GeoJSON在EPSG:4548复算 · spatial review PASS
用地结构(全覆盖 11,399,407 m²)

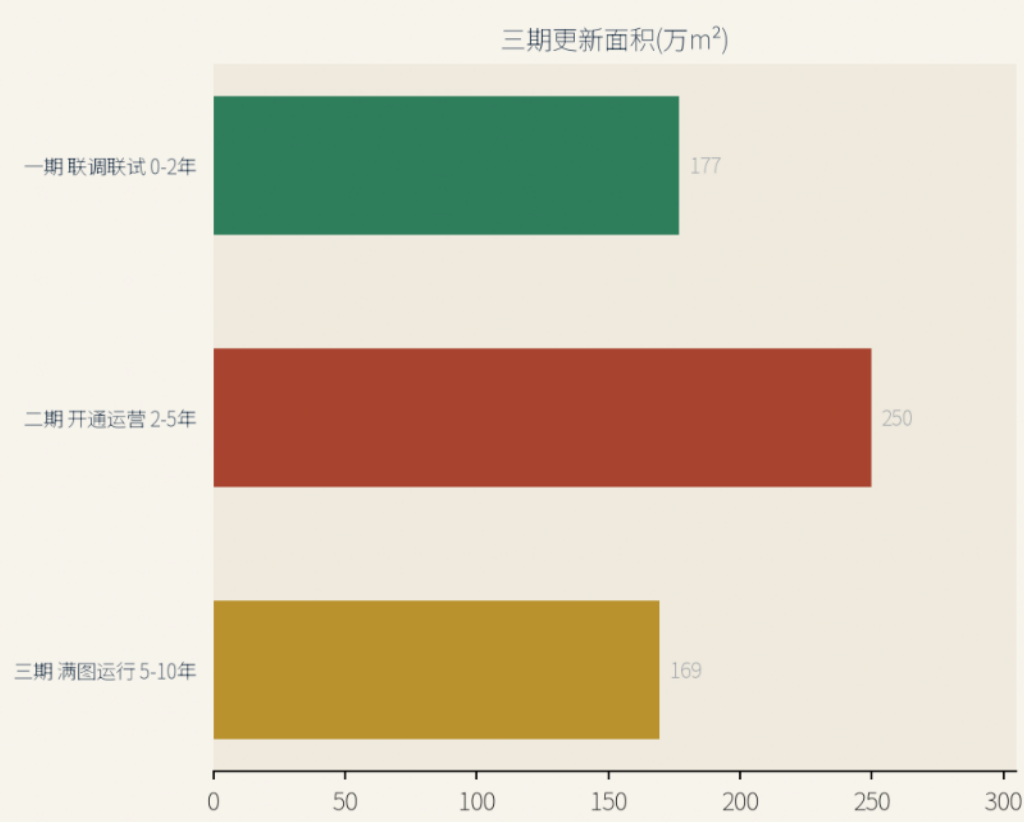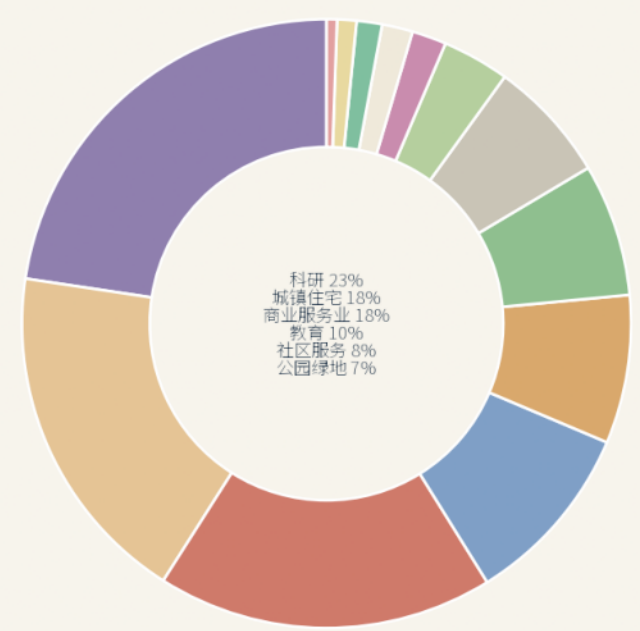

证据链: 每个判断可回到图层与指标



待正式数据补齐(如实登记,不虚构):容积率、最高建筑高度、AI创新指数基线、人才密度基线

边界状态: 临时轮廓范围(provisional) — 依据公开官方认定的OGM数据自行计算并公开给公众和学者, 非官方认证, 不得用于商业, 红黑/绿黄面积, 官方polygon图例和颜色最真。数据 © OpenStreetMap contributors (OSM)。本图由软件 GeoJSON 与 mdx 生成, 保留意见。w543/jingzhang-two-way-line · 2025-05

十二班次场景卡(对开协议格式: 上行采集什么 · 下行回报什么 · 谁能叫停)

任务	场景	节点	上行	下行	复核与退出
T1	低密王人配流检测测试	黄河湾	检测运行数据	检测延迟时段	检测急停/下线
T2	AI交通银行调度测试	知春/后厂路口	匿名流量	等待时间公示	信号人工回退
T3	企业智能体验沙盘	大钟站	授权工作	中小企业数据	人工客服可切换
S4	多态文化等驾	望京碑道	匿名热力	四清洪麟	内网人工审核
S5	健康服务导航	学院路社区	信息咨询	老年陪护	医生复核类型
S6	公共安全运行复盘	对开门	事件复盘	演练公示	仪器启停控制
S7	算力舱冷热调度	双闭环环	设备故障	冬季维保	热网人工旁路
S8	开源社区开发日	发车厅	发布登记	模型半公开	社区评审前置
S9	无障得步行代理	八处路口	设备状态	视障领航	志愿员结束流
S10	校园成果展览	原市报告厅	授权清单	收益公示	技术经理复核
S11	街区微气候感知	明珠金线	温度风光	高温预警	点位公示可关停
S12	绿电报时	绿电大钟	绿电占比	整点报时	数据来源审计